
실제 Unity 객체 기준 · 1층 / 2층 도면 정합

두 도면을 각각 실제 객체 좌표에 독립적으로 변형했습니다. 객체 좌표는 이동하지 않았습니다.

고정 실물: 공식 메시 단면 58개 객체(짙은 회색) · 배치 기둥 96개(초록)

변형 도면: 1층 파랑 · 2층 주황 | 각 도면 기둥 57점 고정 + 공식 구조 추정 8/7점 약한 제약 | 1층 하단 별도 위치도 제외

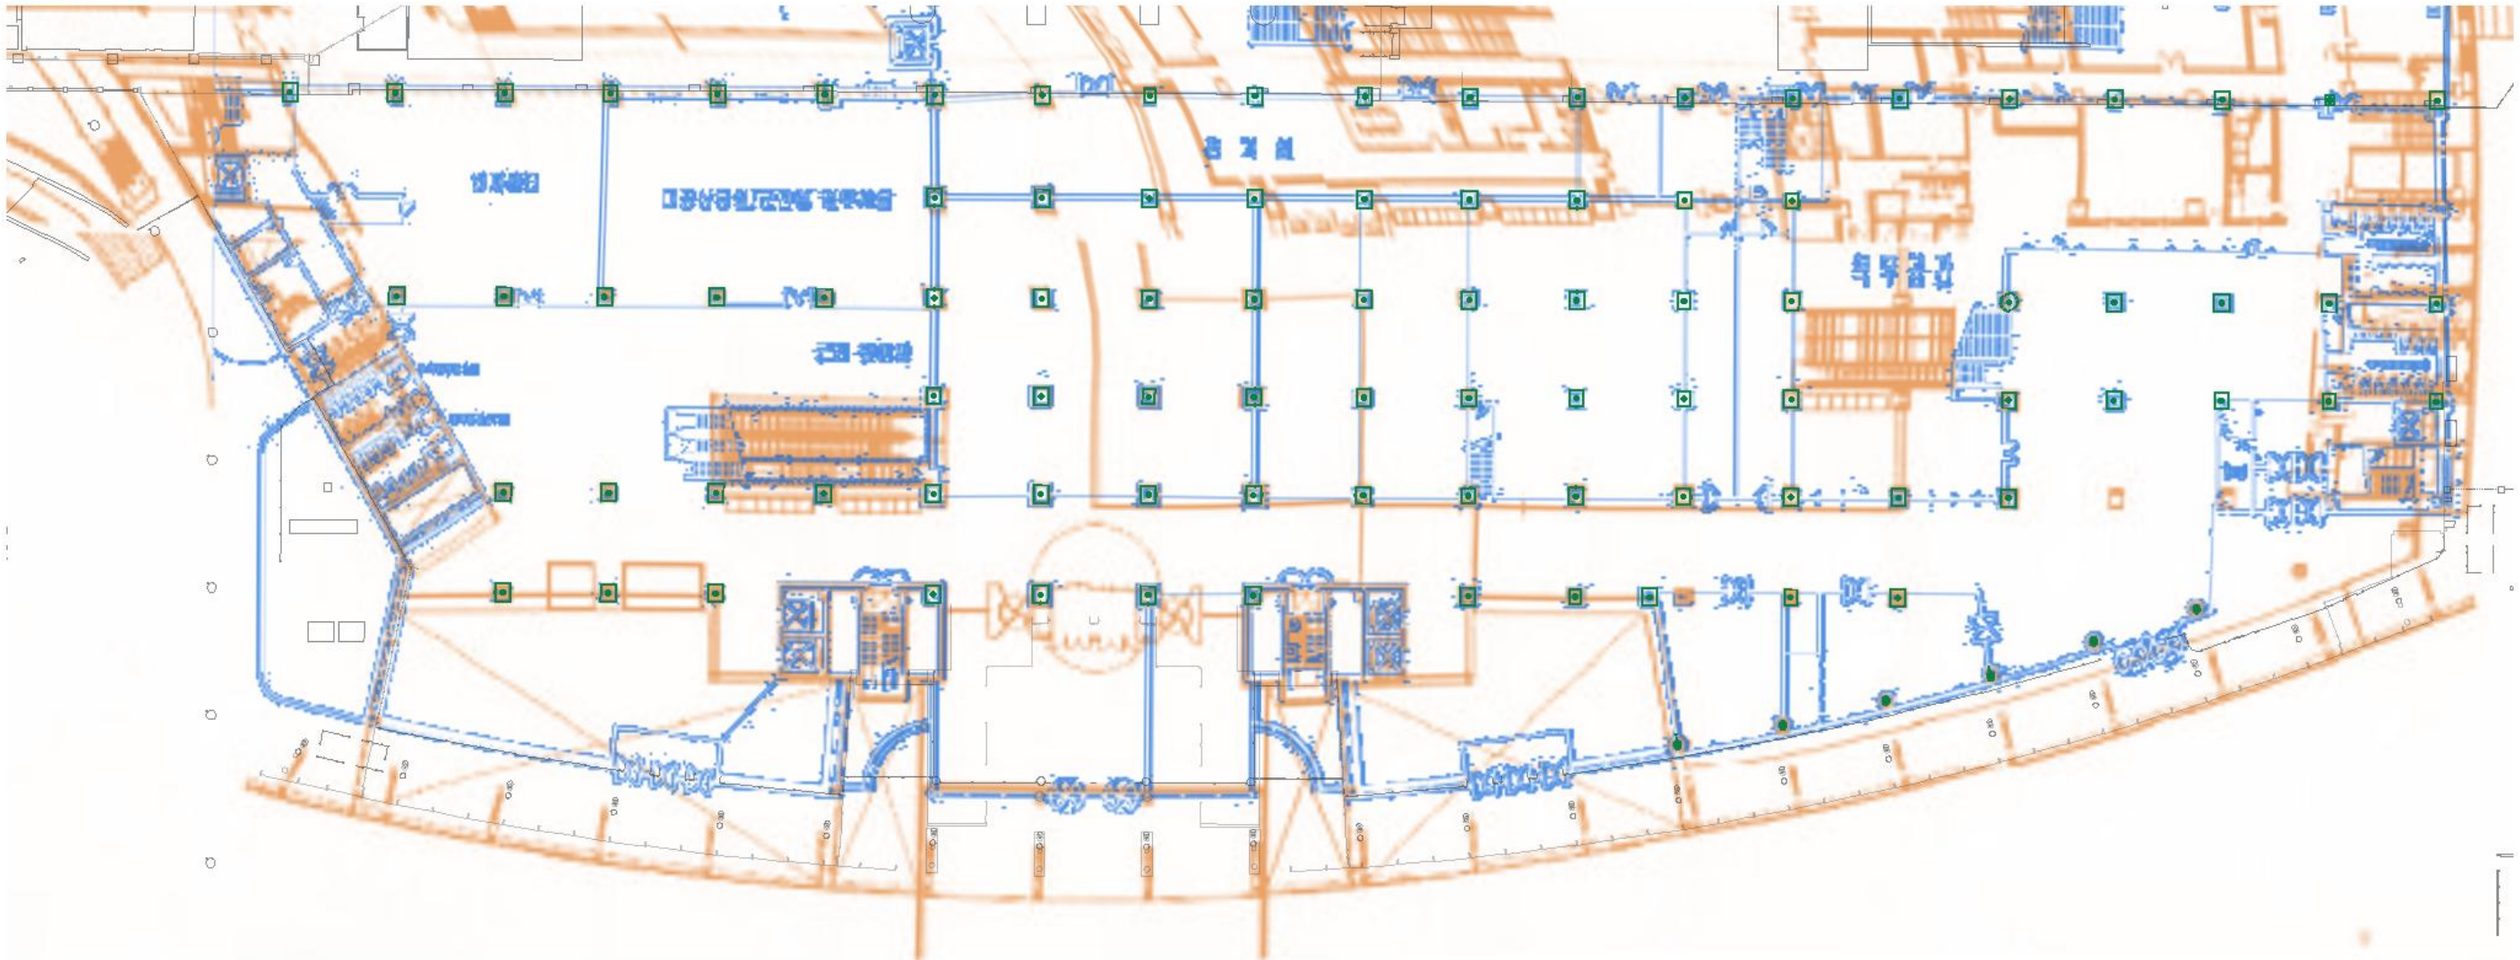


WEST 상세 · 실제 기둥과 공식 구조에 맞춘 두 도면

도면의 서측 코어·벽선은 각각 표시합니다. 서로 다른 층의 실 배치와 추정 구조 대응은 동일성 증명이 아닙니다.

고정 실물: 공식 메시 단면 58개 객체(짙은 회색) · 배치 기둥 96개(초록)

변형 도면: 1층 파랑 · 2층 주황 | 각 도면 기둥 57점 고정 + 공식 구조 추정 8/7점 약한 제약 | 1층 하단 별도 위치도 제외

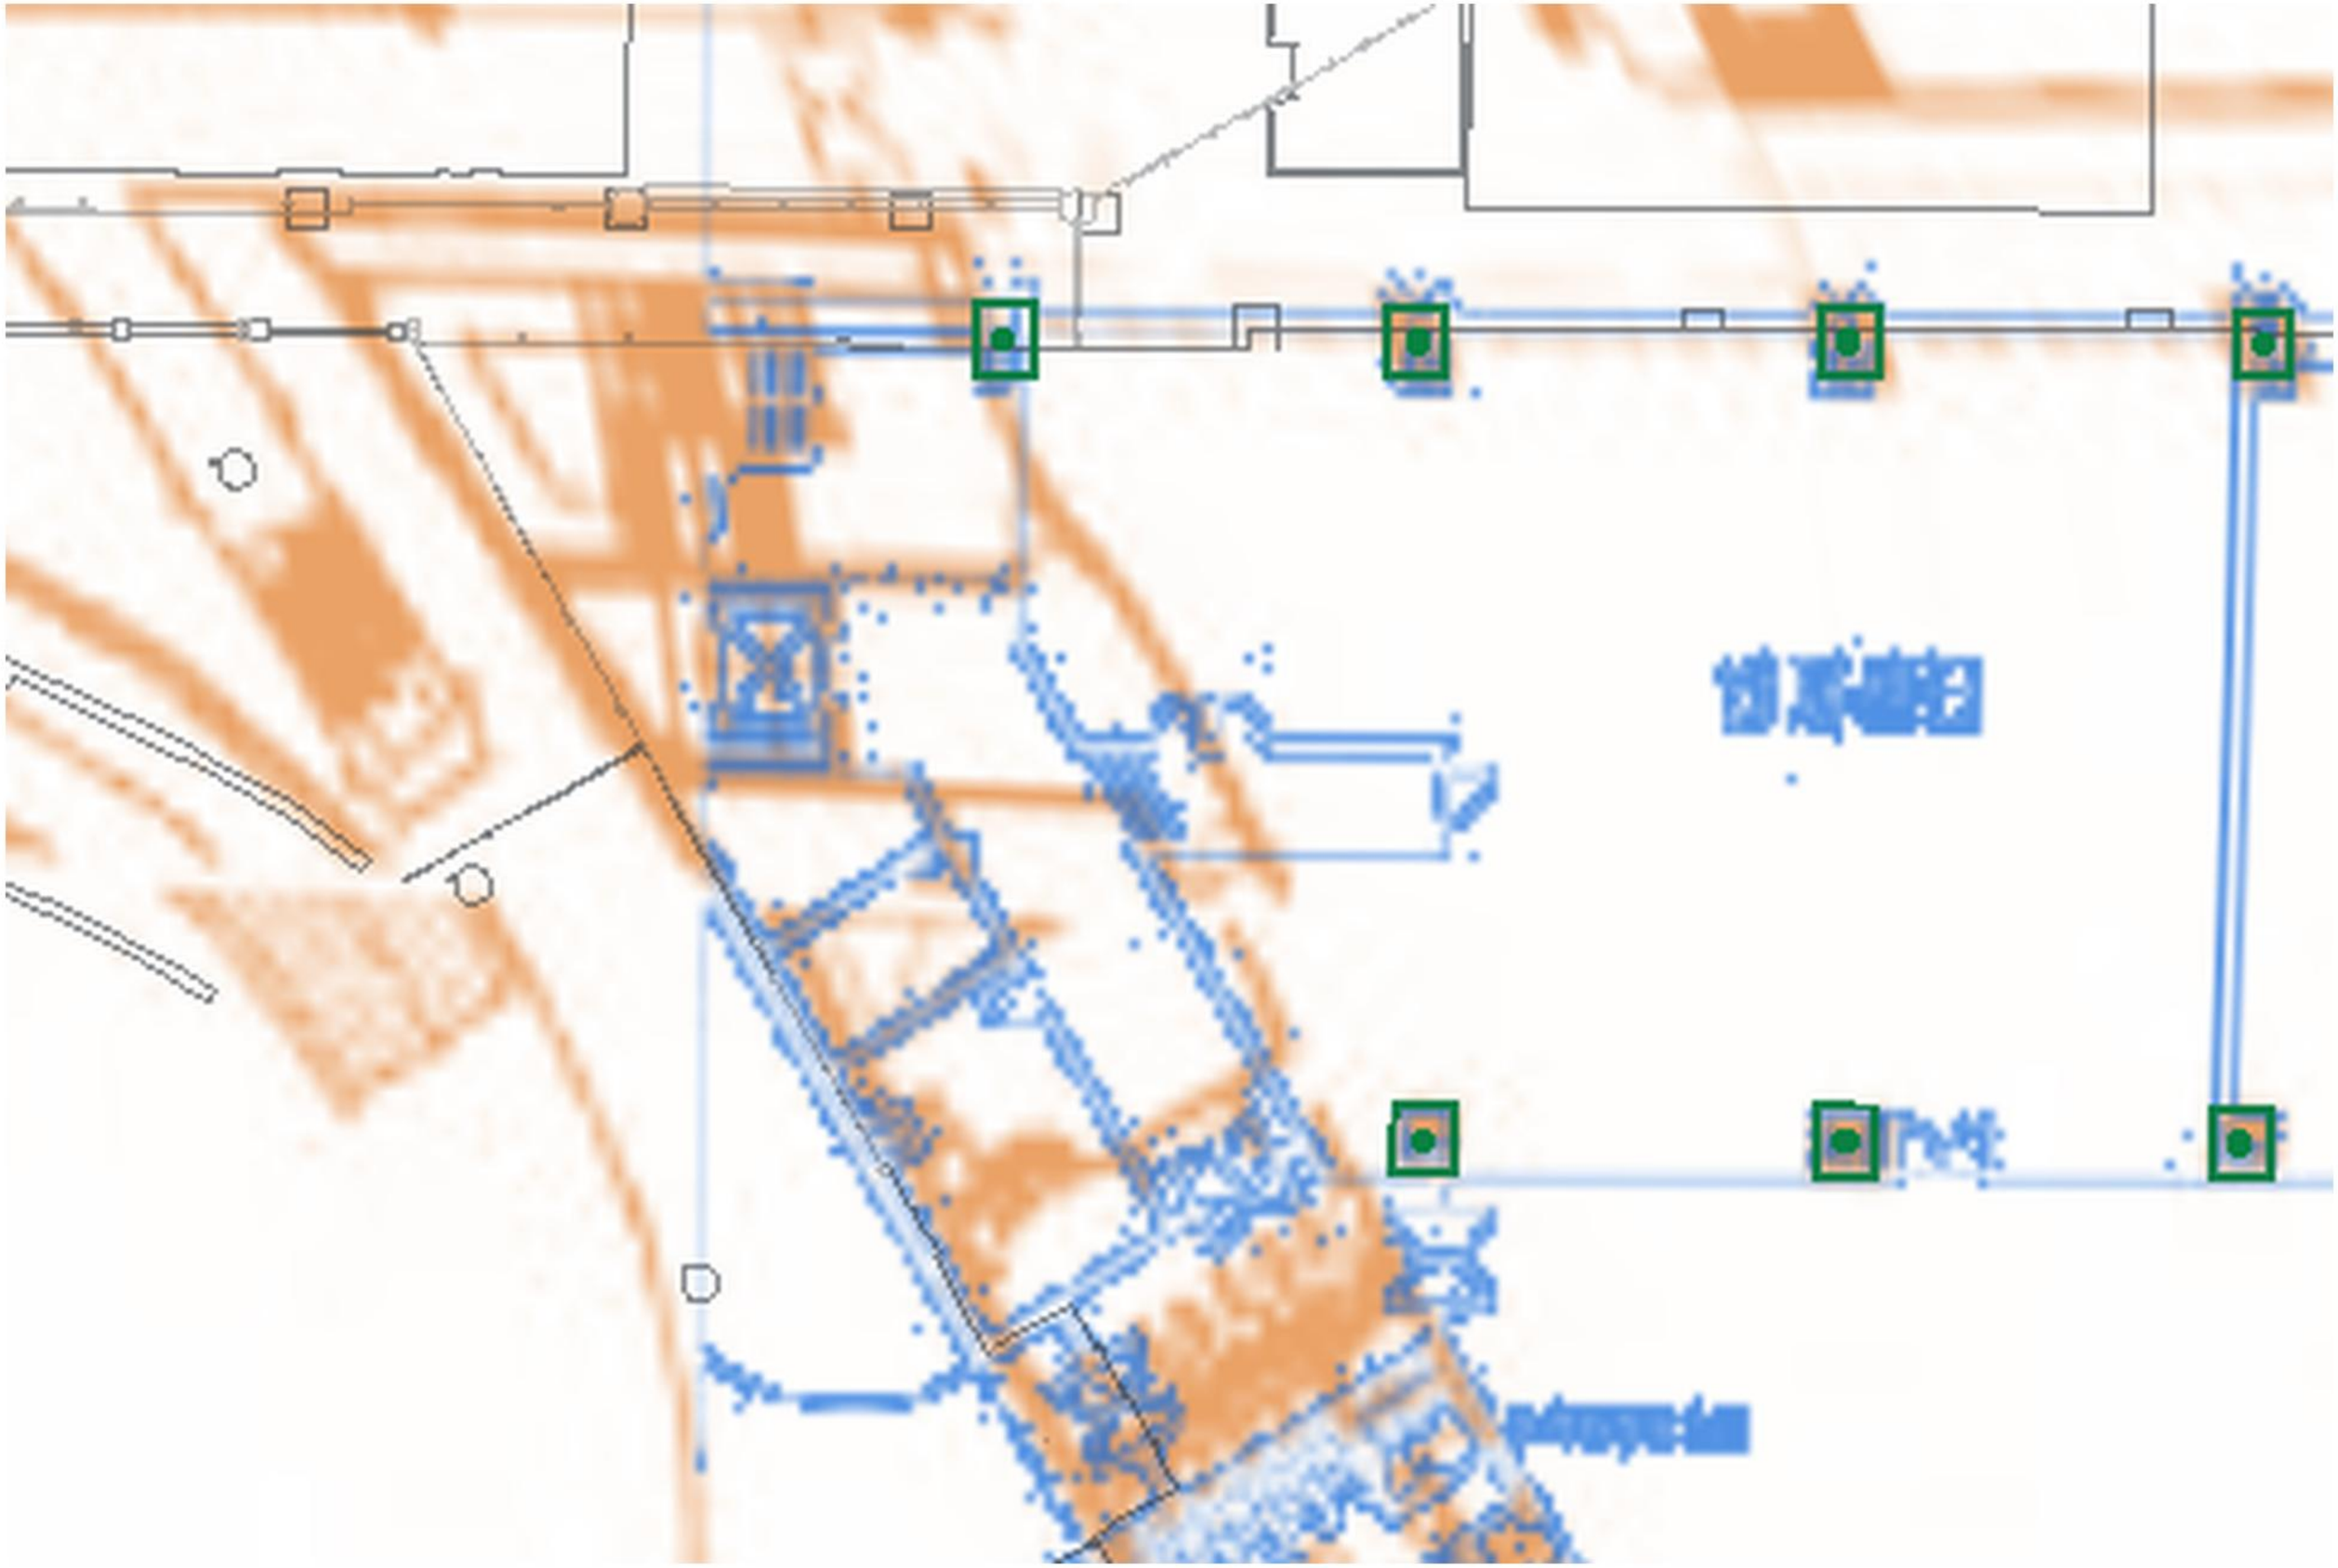

2층 전체 문맥 · 공식 메시 / 실제 기둥 / 두 도면

상부 홀 구조 대응은 약한 MODEL 제약입니다. 도면 비율을 변형하며 실제 공식 구조와 기둥을 고정합니다.

고정 실물: 공식 메시 단면 58개 객체(짙은 회색) · 배치 기둥 96개(초록)

변형 도면: 1층 파랑 · 2층 주황 | 각 도면 기둥 57점 고정 + 공식 구조 추정 8/7점 약한 제약 | 1층 하단 별도 위치도 제외

