
KORAIL RETAIL

부산역 5층 회의실 신축공사

2018 . 12.

코레일유통(주)

Greco DESIGNGROUP

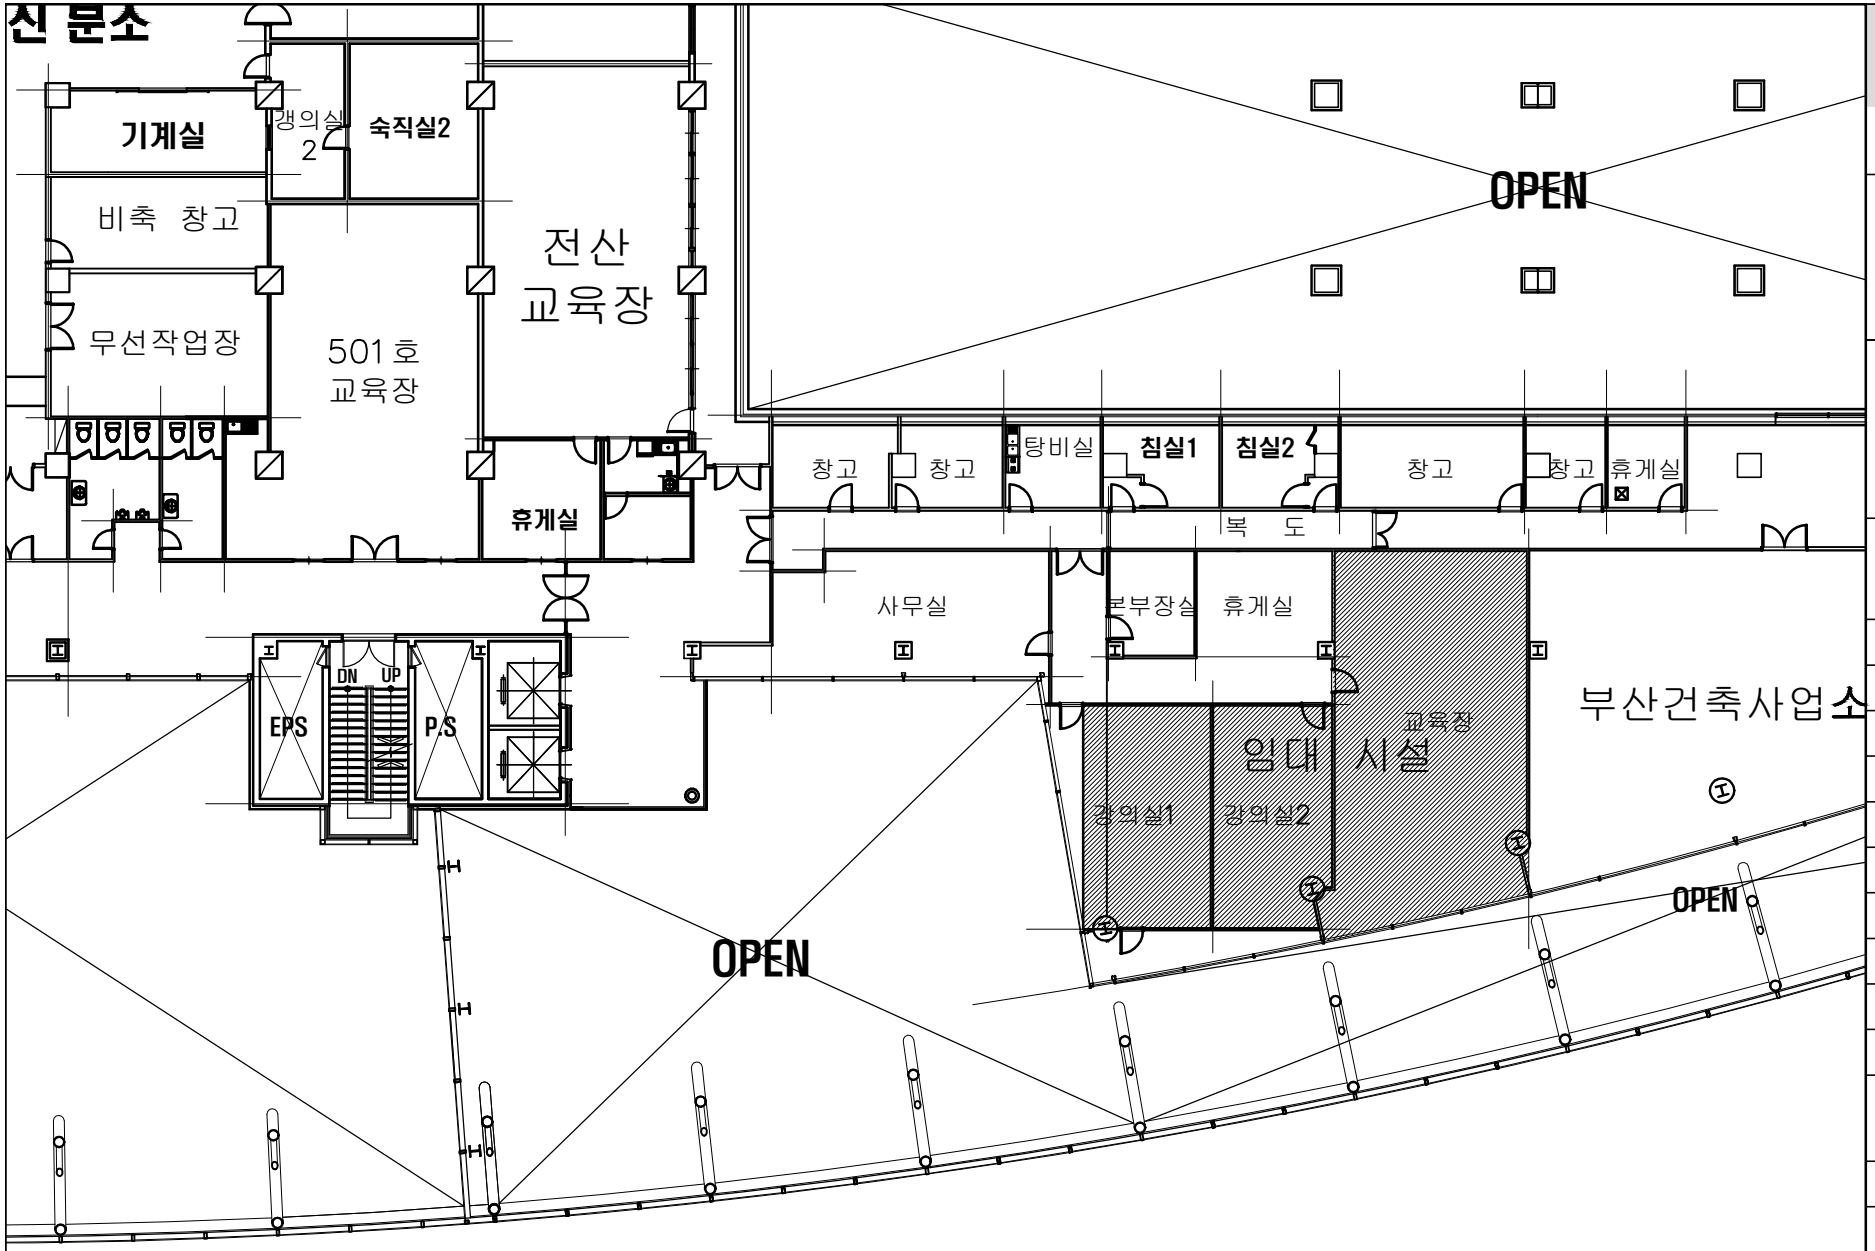

1 BASE PLAN (전체 배치도)

SCALE 1/200

KORAIL RETAIL

서울시 영등포구 당산3가 2-7
TEL / 02) 2630-8945
FAX / 02) 2630-8926

StoryWay

NOTE / REVISION

역무원실 : 49.50㎡/14.98PY
전문점 : 163.27㎡/49.39PY

CH: 3,985

NAME OF PROJECT

부산역 5F 회의실 1,2

ARCHITECTURE

STRUCTURE

MECHANIC

ELECTRIC

APPROVED BY

DESIGNED BY

DRAWING BY
Park, H. R.

CHECKED BY
Kim, S.C.

DATE
2018. 11.


SCALE
1 / 100

DRAWING TITLE
BASE PLAN (전체 배치도)

PROJECT NO.

SHEET NO.	DRAWING NO.
101	P-101

Greco
Sukjung Bldg. 2F
203-3 Donggyo-dong,
Mapo-gu, Seoul, Korea. 03992
www.grecodesign.co.kr
T.+82-2-336-2082 F.+82-2-336-2297

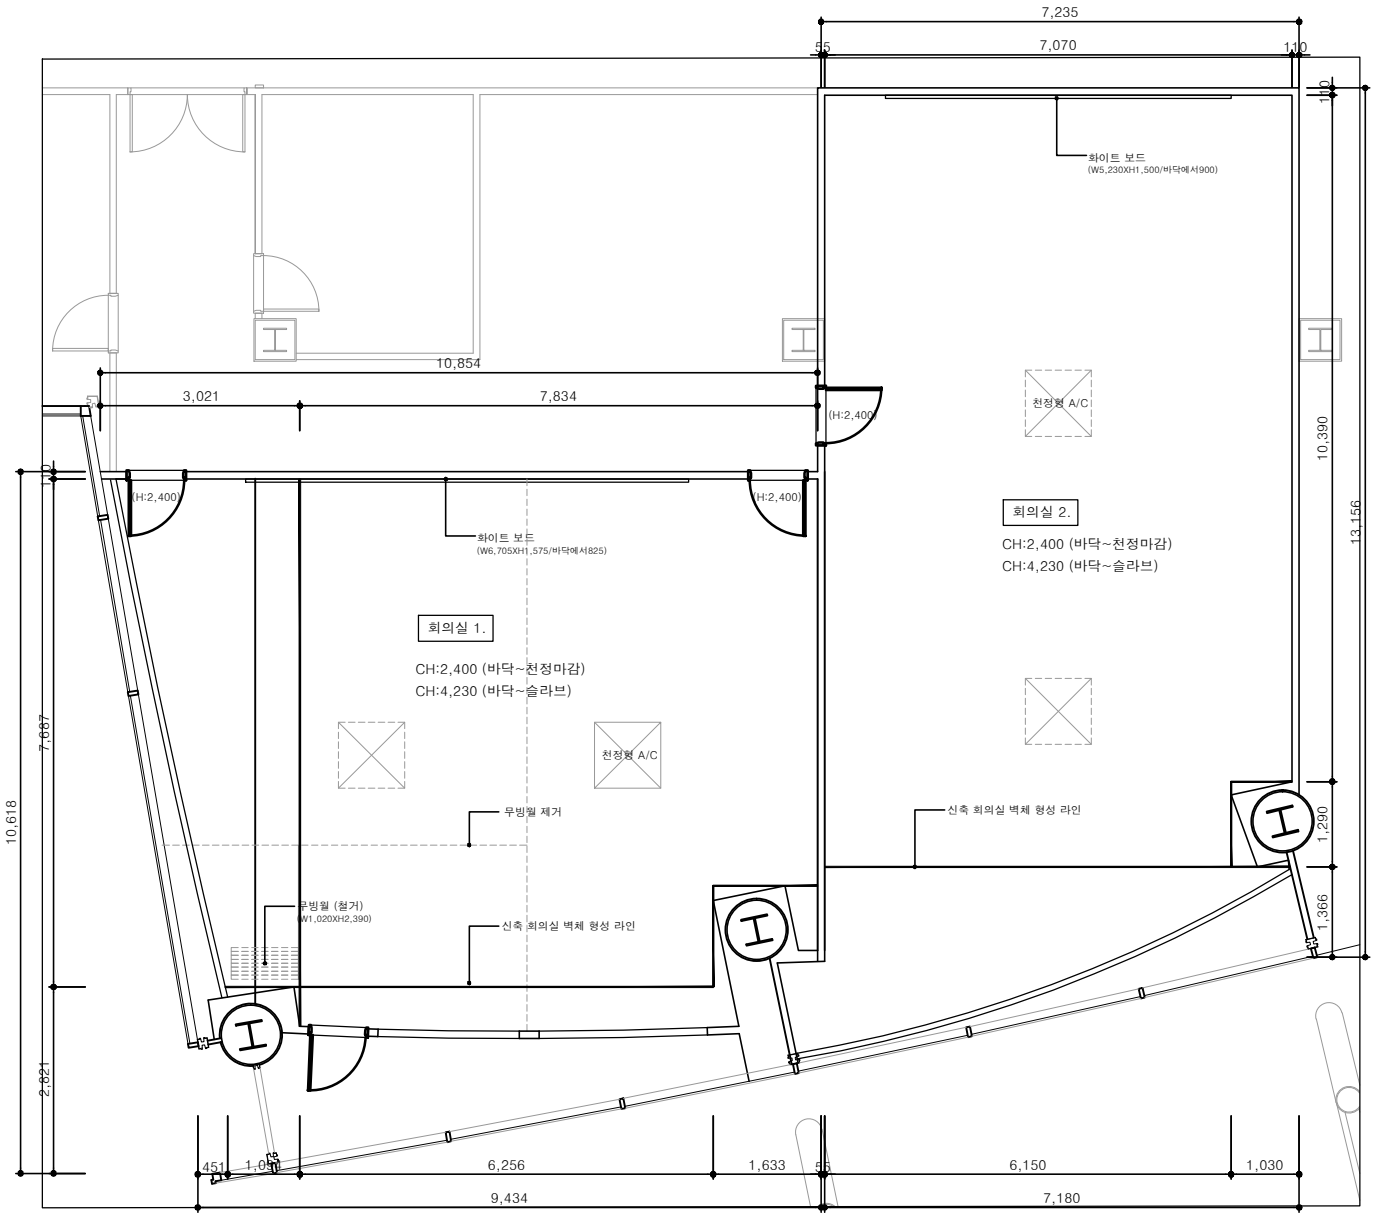

※ 소회의실1 기존 집기 :

- 선반장 1ea (800*410*1880)
- 스탠드 회의 테이블 1ea (700*500*950)
- 책상 14ea (1800*450*730)
- 의자 38ea
- 화이트보드 1ea (w:1500)
- 빔 프로젝트, 스크린 1ea (w:2520)
- 랙 1ea (600*600*h900)
- 정수기 1ea, 쓰레기통 1ea, 책꽂이 1ea,
- 스피커 4ea

※ 소회의실2 기존 집기 :

- 선반장 1ea (800*410*1880)
- 스탠드 회의 테이블 1ea (700*500*950)
- 책상 14ea (1800*450*730)
- 의자 41ea
- 화이트보드 1ea (w:1500)
- 빔 프로젝트, 스크린 1ea (w:2520)
- 랙 1ea (600*600*h900)
- 정수기 1ea, 쓰레기통 1ea, 책꽂이 1ea, 서큘레이터 1ea
- 스피커 4ea

■ NOTES

3.

4.

5.

6.

1 BASE FLOOR PLAN

SCALE 1/80

KORAIL RETAIL

서울시 영등포구 당산3가 2-7
TEL / 02) 2630-8945
FAX / 02) 2630-8926

StoryWay

NOTE / REVISION

총면적(철거공사) : 201.52㎡
회의실1 : 63.09㎡
회의실2 : 86.02㎡
CH(내부): 2,400 (간접 2,600)

NAME OF PROJECT

부산역 5F 회의실

ARCHITECTURE

STRUCTURE

MECHANIC

ELECTRIC

APPROVED BY

DESIGNED BY

DRAWING BY
Park, H. R.

CHECKED BY
Kim, S.C.

DATE
2018. 08.


SCALE
1 / 80

DRAWING TITLE
BASE FLOOR PLAN

PROJECT NO.

SHEET NO.	DRAWING NO.
102	P-102

Greco DESIGN GROUP
Sukjung Bldg. 2F
203-3 Donggyo-dong,
Mapo-gu, Seoul, Korea. 03992
www.grecodesign.co.kr
T.+82-2-336-2082 F.+82-2-336-2297

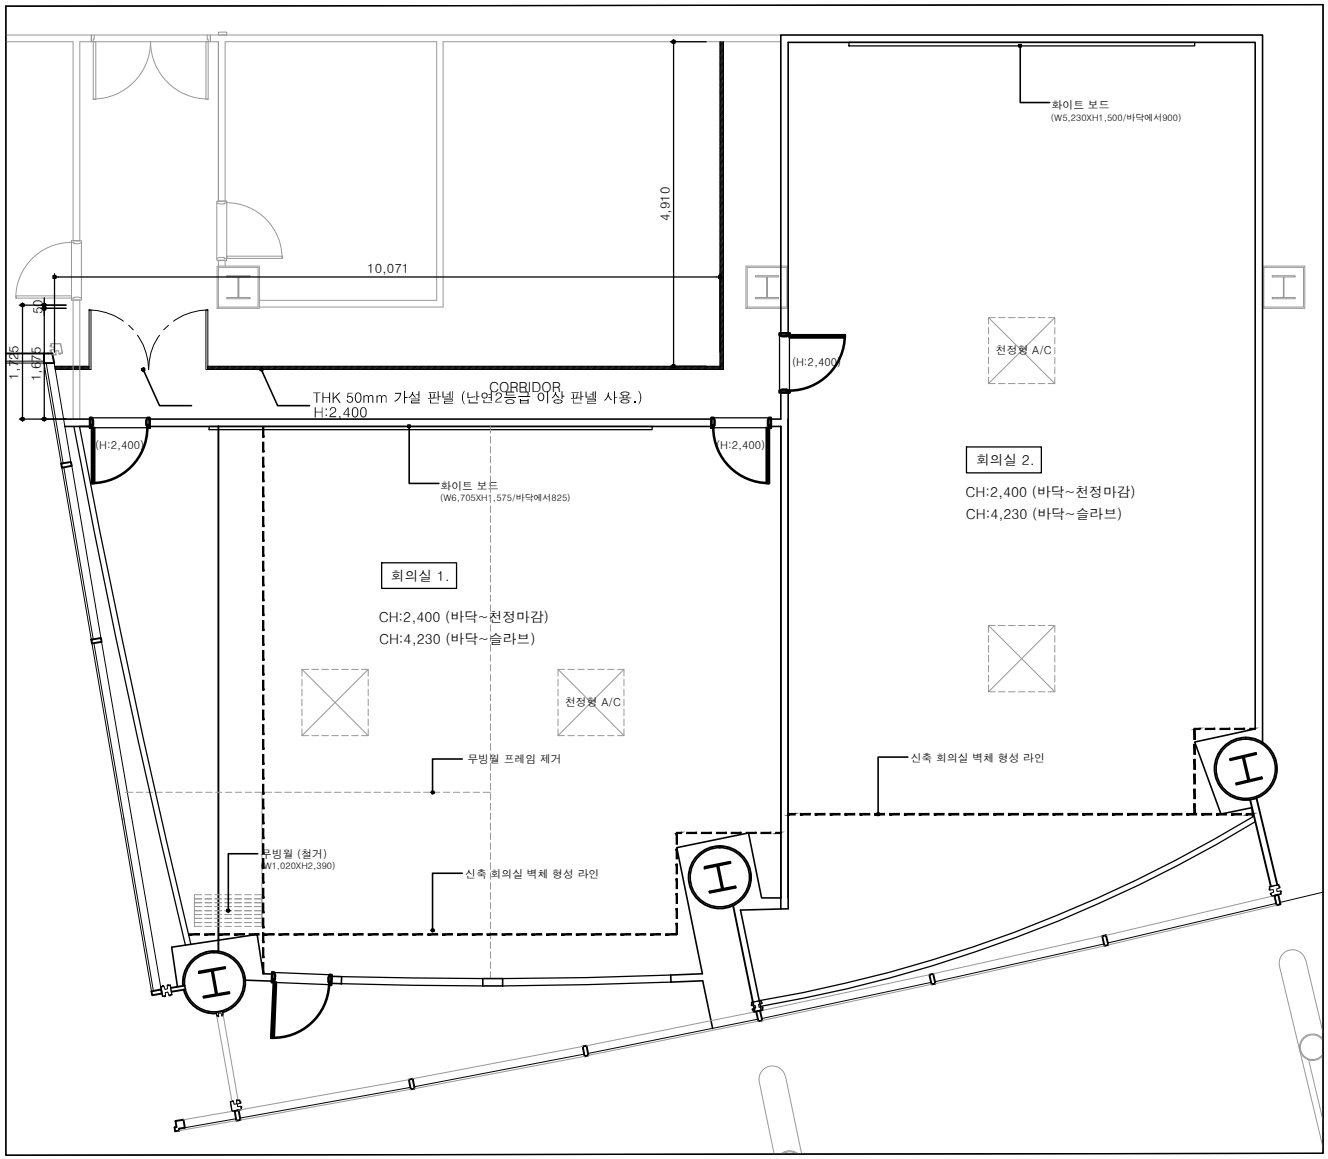

■ NOTES

1. 복도 기존 데코타일 SPEC 확인 후 손상부위 보수 요!
2. 재료 분리대
3. 바닥 흡음재 제외 : 기존 데코타일 철거 후 바닥 시공
4. 복도 : 공사범위 제외

1 TEMPORARY FLOOR PLAN (가설 계획도)

SCALE 1/80

KORAIL RETAIL

서울시 영등포구 당산3가 2-7
TEL / 02) 2630-8945
FAX / 02) 2630-8926

StoryWay

NOTE / REVISION

총면적(철거공사) : 201.52㎡
회의실1 : 63.09㎡
회의실2 : 86.02㎡
CH: 2,400

NAME OF PROJECT

부산역 5F 회의실

ARCHITECTURE

STRUCTURE

MECHANIC

ELECTRIC

APPROVED BY

DESIGNED BY

DRAWING BY
Park, H. R.

CHECKED BY
Kim, S.C.

DATE
2018. 08.


SCALE
1 / 80

DRAWING TITLE
TEMPORARY FLOOR PLAN
(가설 계획도)

PROJECT NO.

SHEET NO.	DRAWING NO.
103	P-103

Greco DESIGN GROUP
Sukjung Bldg. 2F
203-3 Donggyo-dong,
Mapo-gu, Seoul, Korea. 03992
www.grecodesign.co.kr
T.+82-2-336-2082 F.+82-2-336-2297

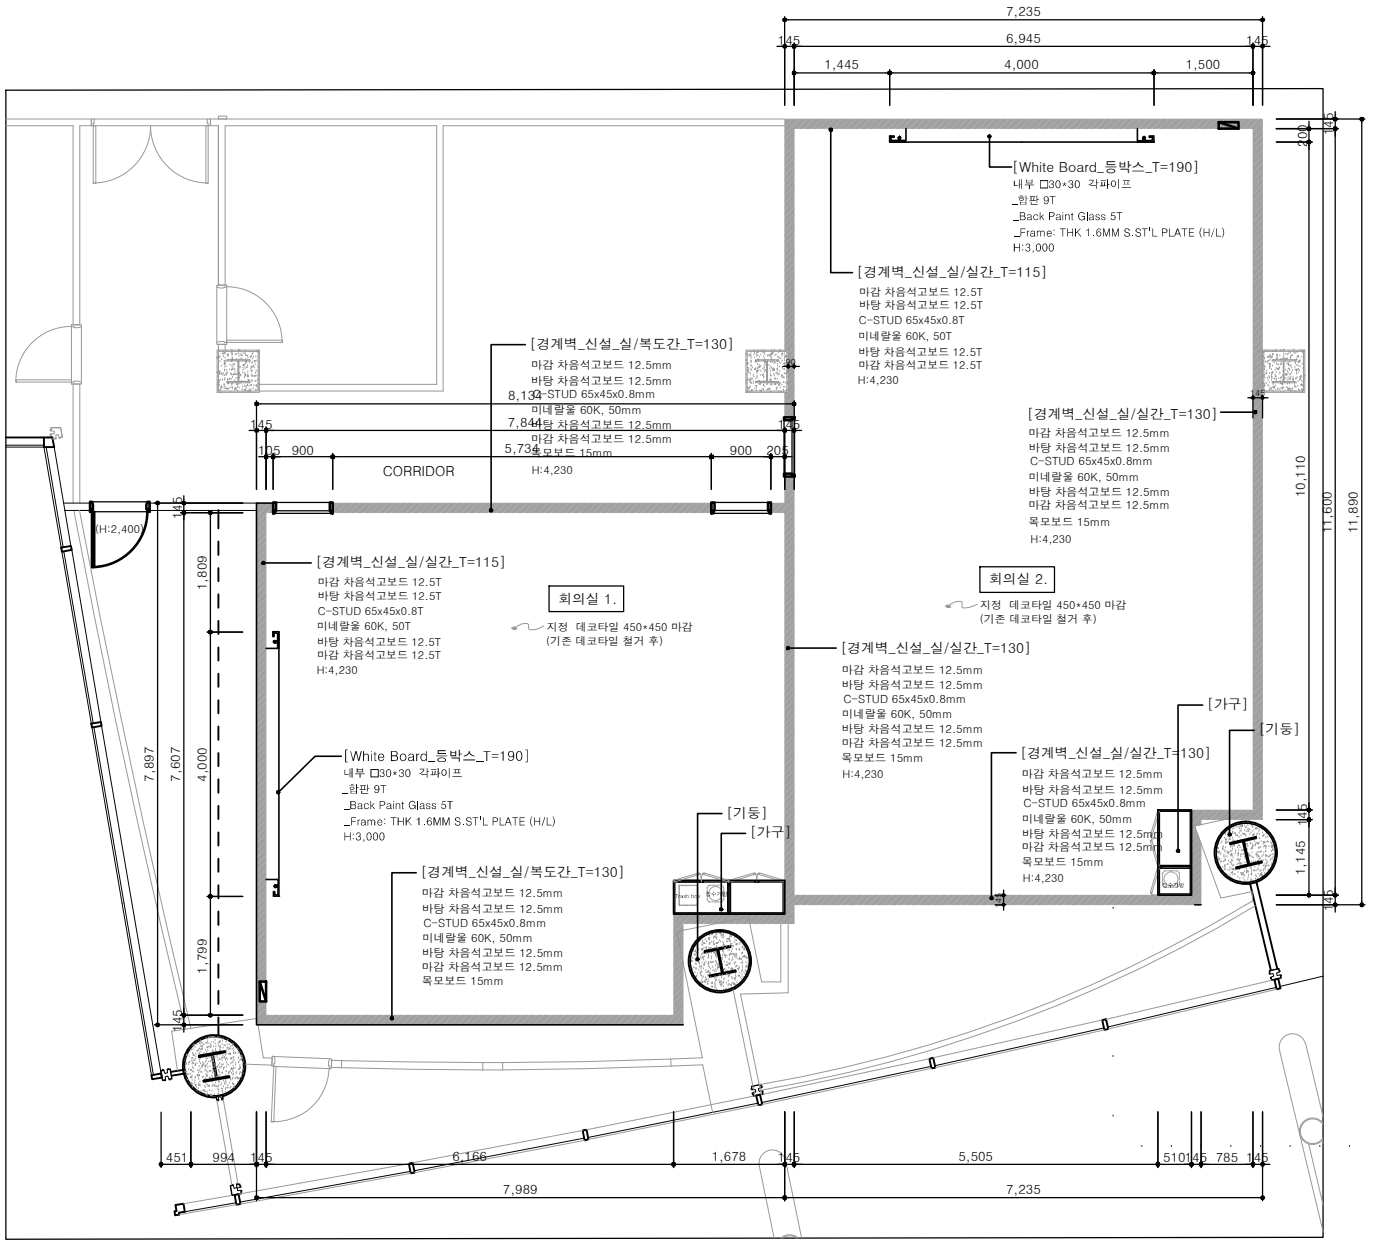

■ NOTES

1. 외벽_벽체 검토 요!
2. 기존 슬라브 벽체 및 철거 부위 체크 요!

1 STRUCTURE PLAN

SCALE 1/80

KORAIL RETAIL

서울시 영등포구 당산3가 2-7
TEL / 02) 2630-8945
FAX / 02) 2630-8926

StoryWay

NOTE / REVISION


총면적(철거공사) : 201.52㎡
회의실1 : 63.09㎡
회의실2 : 86.02㎡
CH: 2,400

NAME OF PROJECT

부산역 5F 회의실

ARCHITECTURE	
STRUCTURE	
MECHANIC	
ELECTRIC	
APPROVED BY	
DESIGNED BY	
DRAWING BY	Park, H. R.
CHECKED BY	Kim, S.C.
DATE	2018. 08.
SCALE	1 / 80
DRAWING TITLE	STRUCTURE PLAN
PROJECT NO.	
SHEET NO.	104
DRAWING NO.	P-104

Greco DESIGN GROUP
Sukjung Bldg. 2F
203-3 Donggyo-dong,
Mapo-gu, Seoul, Korea. 03992
www.grecodesign.co.kr
T.+82-2-336-2082 F.+82-2-336-2297

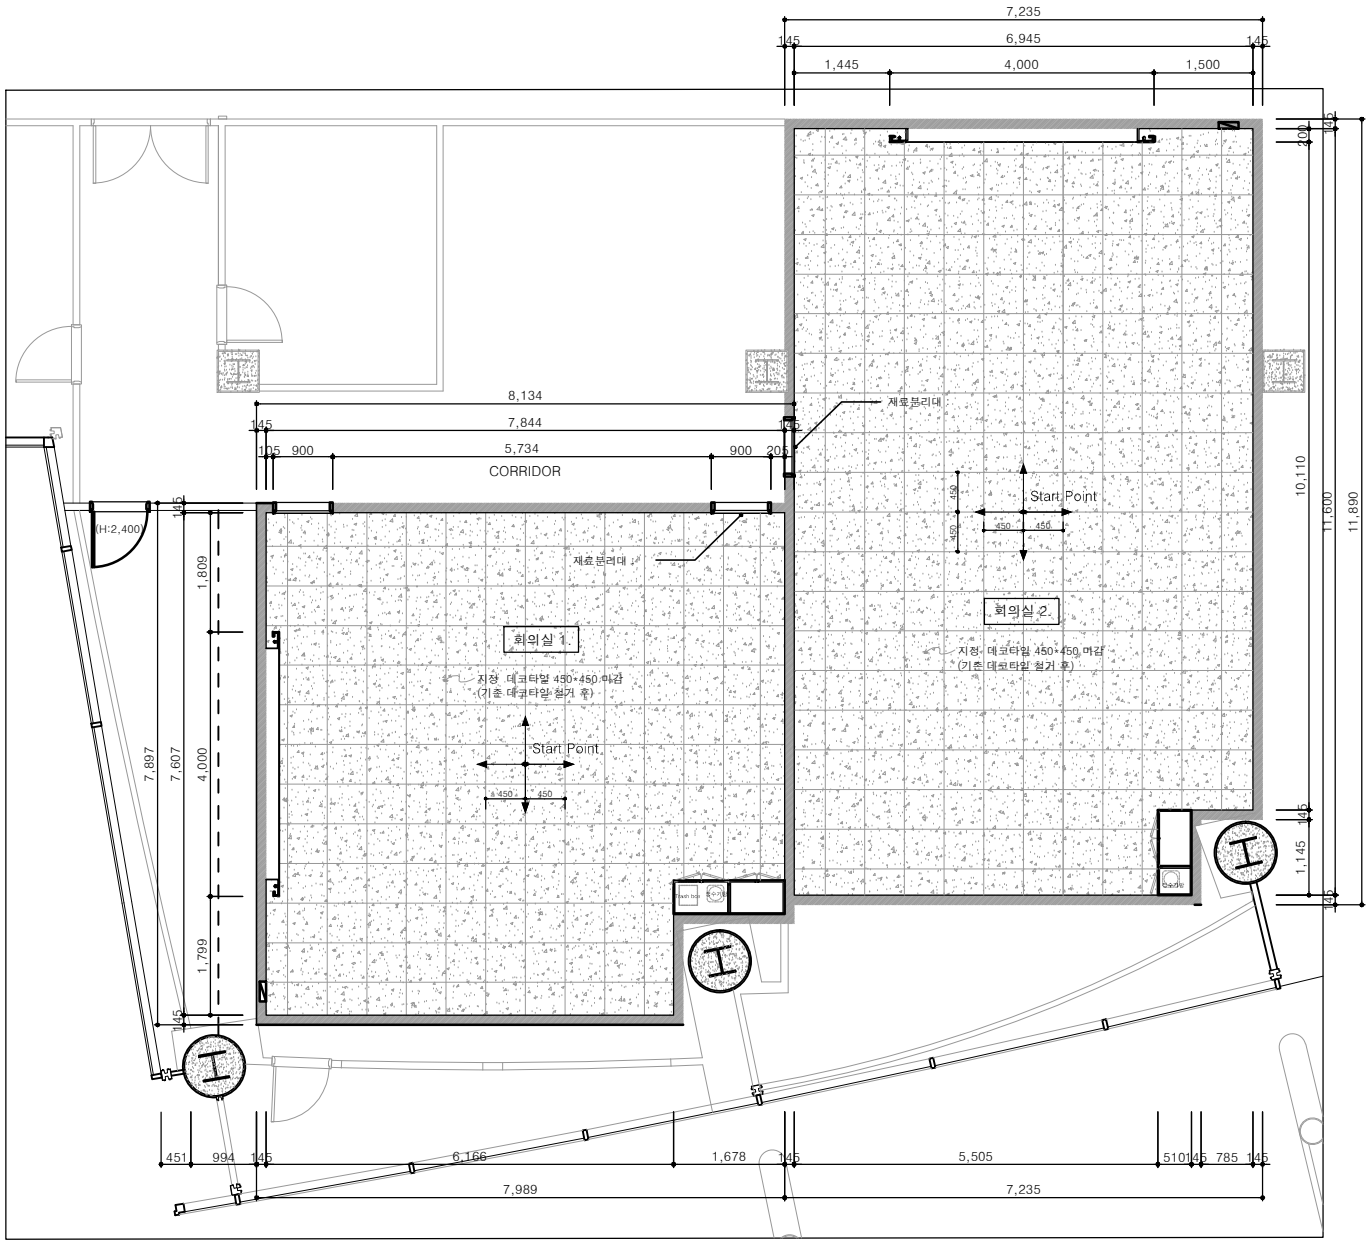

■ NOTES

1. 복도 기존 데코타일 SPEC 확인 후 손상부위 보수 요!
2. 재료 분리대
3. 바닥 흡음재 제외 : 기존 데코타일 철거 후 바닥 시공
4. 복도 : 공사범위 제외

① PATTERN PLAN

SCALE 1/80

KORAIL RETAIL
서울시 영등포구 당산3가 2-7
TEL / 02) 2630-8945
FAX / 02) 2630-8926

StoryWay

NOTE / REVISION

총면적(철거공사) : 201.52㎡
회의실1 : 63.09㎡
회의실2 : 86.02㎡
CH: 2,400

NAME OF PROJECT
부산역 5F 회의실

ARCHITECTURE

STRUCTURE

MECHANIC

ELECTRIC

APPROVED BY

DESIGNED BY

DRAWING BY
Park, H. R.

CHECKED BY
Kim, S.C.

DATE
2018. 08.


SCALE
1 / 80

DRAWING TITLE
PATTERN PLAN

PROJECT NO.

SHEET NO.	DRAWING NO.
105	P-105

Greco DESIGN GROUP
Sukjung Bldg. 2F
203-3 Donggyo-dong,
Mapo-gu, Seoul, Korea. 03992
www.grecodesign.co.kr
T.+82-2-336-2082 F.+82-2-336-2297

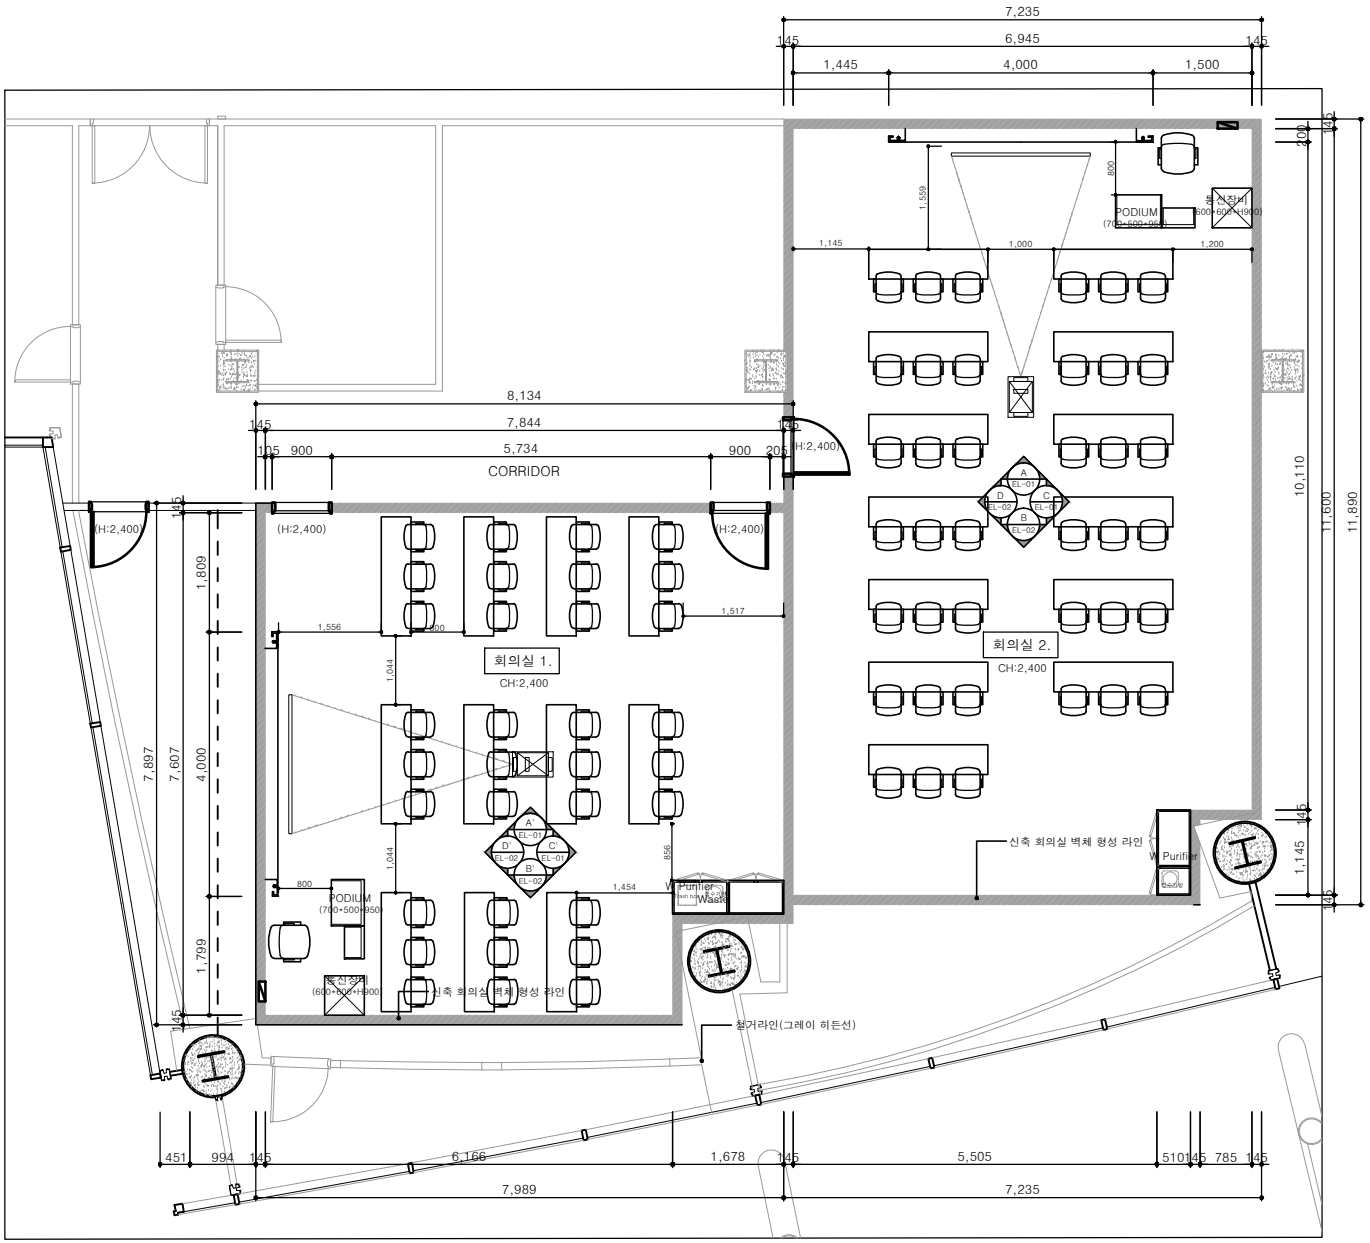

■ NOTES

1. 공조관련 협의 요!(공사범위 제외)
2. 커튼월 (건축기기) 점검도어 위치 체크 요! (회의실 1/2 도어 없음)
3. 경계벽체 형성 위치 (기둥 직선 위치 확인, 벽체 형성 위치 재확인 요!)

1 FLOOR PLAN

SCALE 1/80

KORAIL RETAIL
서울시 영등포구 당산3가 2-7
TEL / 02) 2630-8945
FAX / 02) 2630-8926

StoryWay

NOTE / REVISION

총면적(철거공사) : 201.52㎡
회의실1 : 63.09㎡
회의실2 : 86.02㎡
CH: 2,400

NAME OF PROJECT
부산역 5F 회의실

ARCHITECTURE

STRUCTURE

MECHANIC

ELECTRIC

APPROVED BY

DESIGNED BY

DRAWING BY
Park, H. R.

CHECKED BY
Kim, S.C.

DATE
2018. 08.


SCALE
1 / 80

DRAWING TITLE
FLOOR PLAN

PROJECT NO.

SHEET NO.	DRAWING NO.
106	P-106

Greco DESIGN GROUP
Sukjung Bldg. 2F
203-3 Donggyo-dong,
Mapo-gu, Seoul, Korea. 03992
www.grecodesign.co.kr
T.+82-2-336-2082 F.+82-2-336-2297

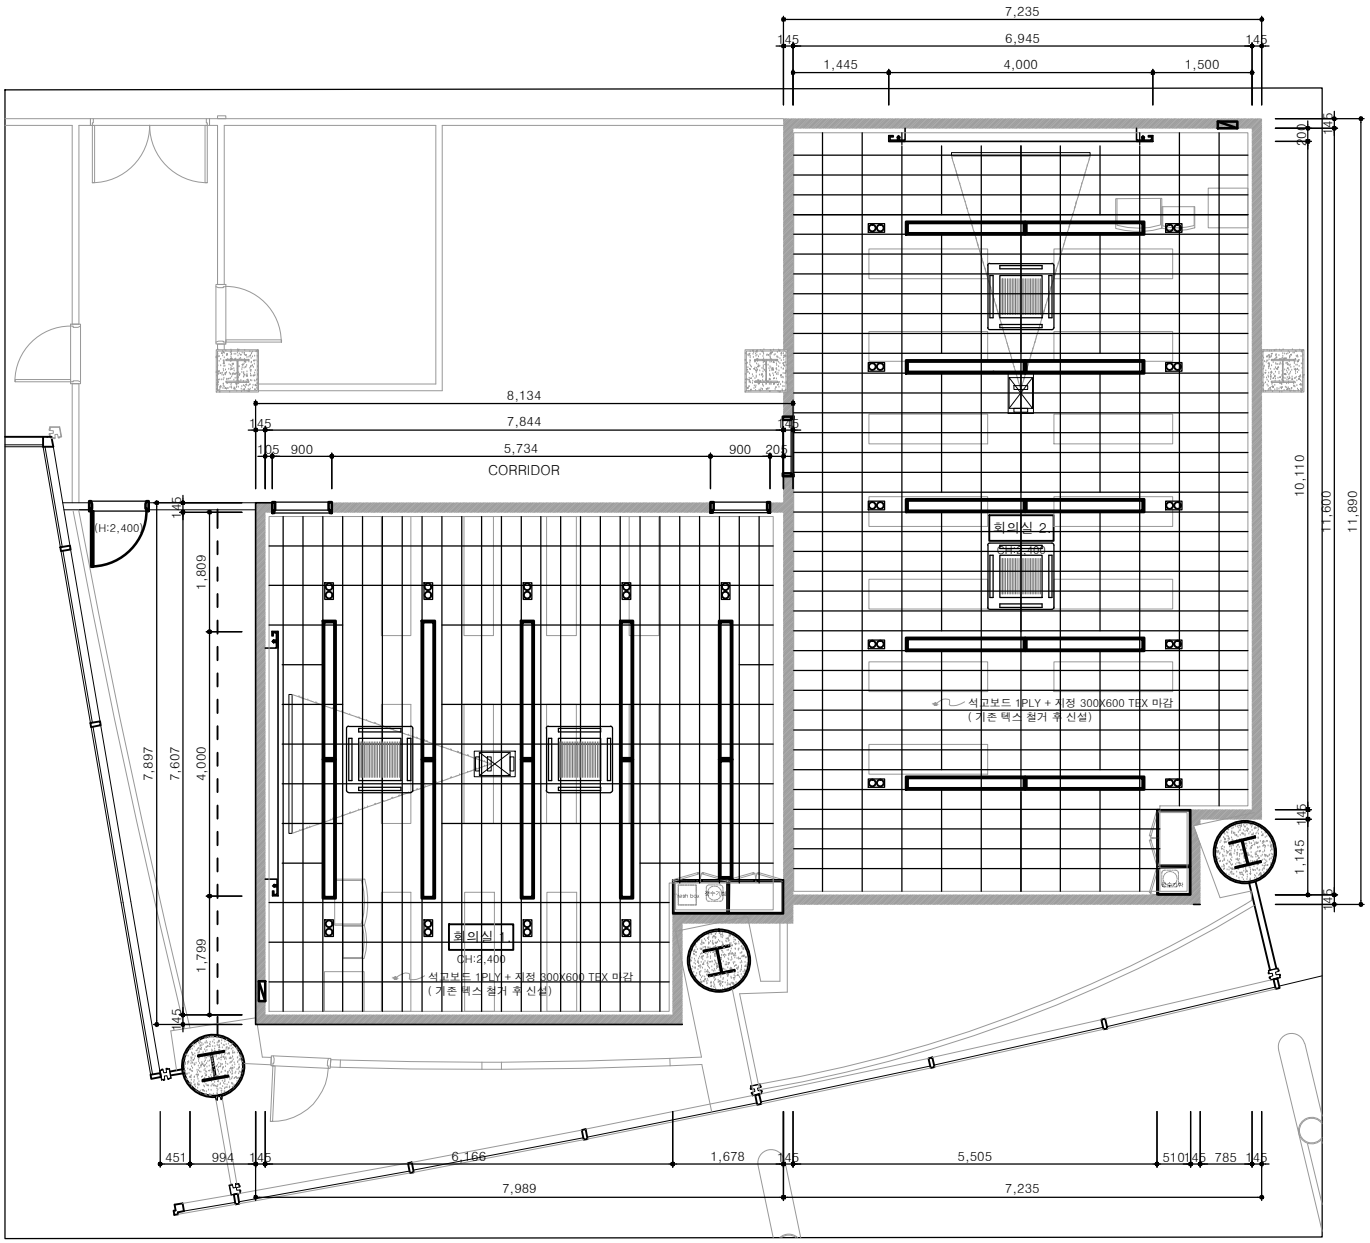

1 CEILING PLAN

SCALE 1/80

KORAIL RETAIL

서울시 영등포구 당산3가 2-7
TEL / 02) 2630-8945
FAX / 02) 2630-8926

StoryWay

NOTE / REVISION

총면적(철거공사) : 201.52㎡
회의실1 : 63.09㎡
회의실2 : 86.02㎡
CH: 2,400

NAME OF PROJECT

부산역 5F 회의실

ARCHITECTURE

STRUCTURE

MECHANIC

ELECTRIC

APPROVED BY

DESIGNED BY

DRAWING BY
Park, H. R.

CHECKED BY
Kim, S.C.

DATE
2018. 08.


SCALE
1 / 80

DRAWING TITLE
CEILING PLAN

PROJECT NO.


SHEET NO.	DRAWING NO.
107	P-107

Greco DESIGN GROUP
Sukjung Bldg. 2F
203-3 Donggyo-dong,
Mapo-gu, Seoul, Korea. 03992
www.grecodesign.co.kr
T.+82-2-336-2082 F.+82-2-336-2297

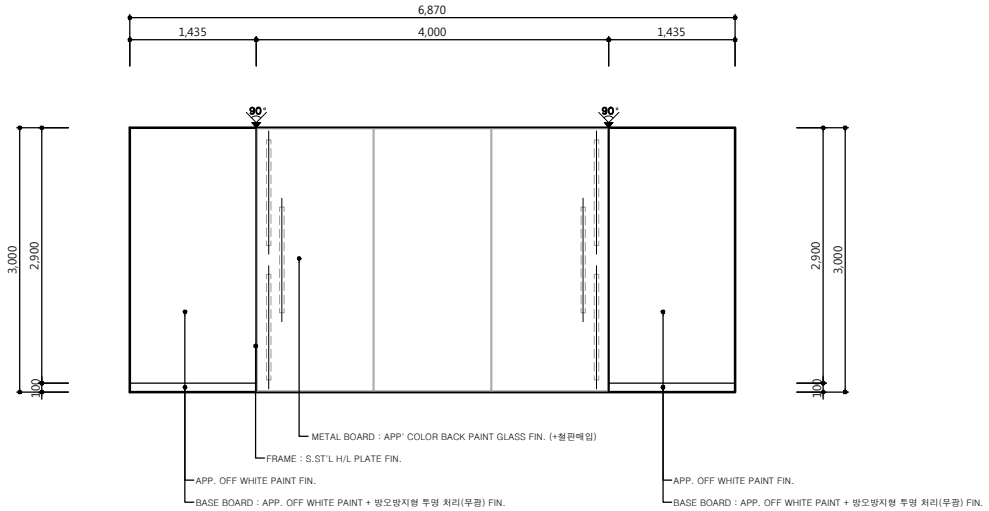

1 ELEVATION A

SCALE 1/60

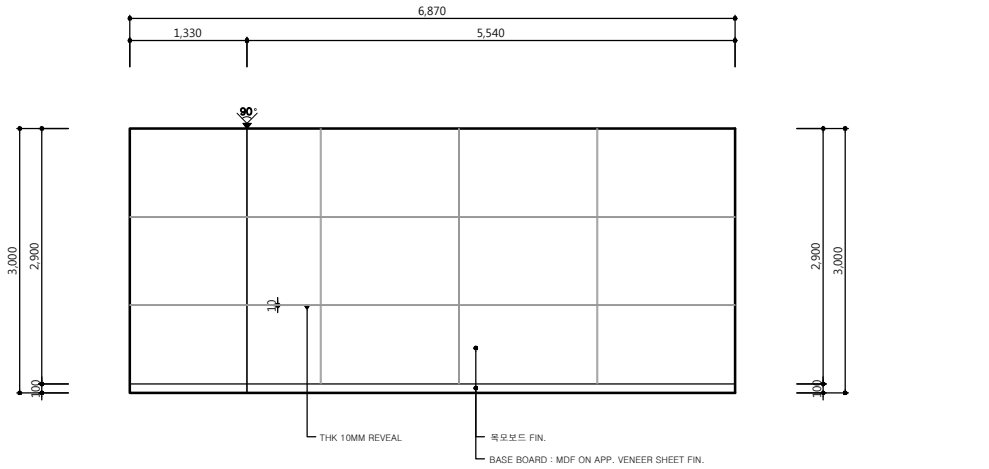

2 ELEVATION B

SCALE 1/60

KORAIL RETAIL
서울시 영등포구 당산3가 2-7
TEL / 02) 2630-8945
FAX / 02) 2630-8926
StoryWay

NOTE / REVISION

NAME OF PROJECT
부산역 5F 회의실

ARCHITECTURE

STRUCTURE

MECHANIC

ELECTRIC

APPROVED BY

DESIGNED BY

DRAWING BY
Park, H. R.

CHECKED BY
Kim, S.C.

DATE
2018. 08.


SCALE
1 / 60

DRAWING TITLE
ELEVATION 01 (회의실 2)

PROJECT NO.


SHEET NO.	DRAWING NO.
201	E-201

Greco DESIGN GROUP
Sukjung Bldg. 2F
203-3 Donggyo-dong,
Mapo-gu, Seoul, Korea. 03992
www.grecodesign.co.kr
T.+82-2-336-2082 F.+82-2-336-2297

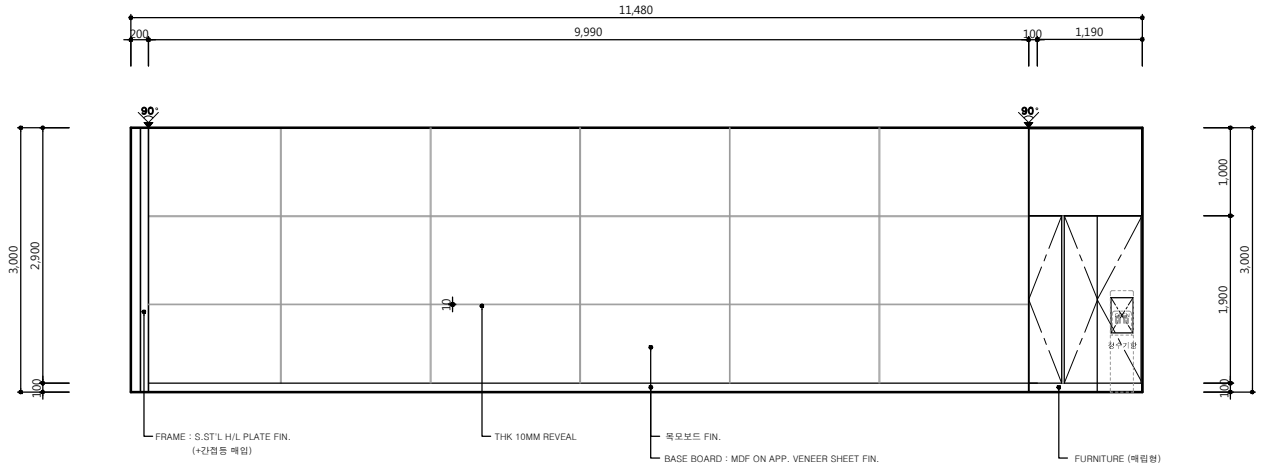

3 ELEVATION C

SCALE 1/60

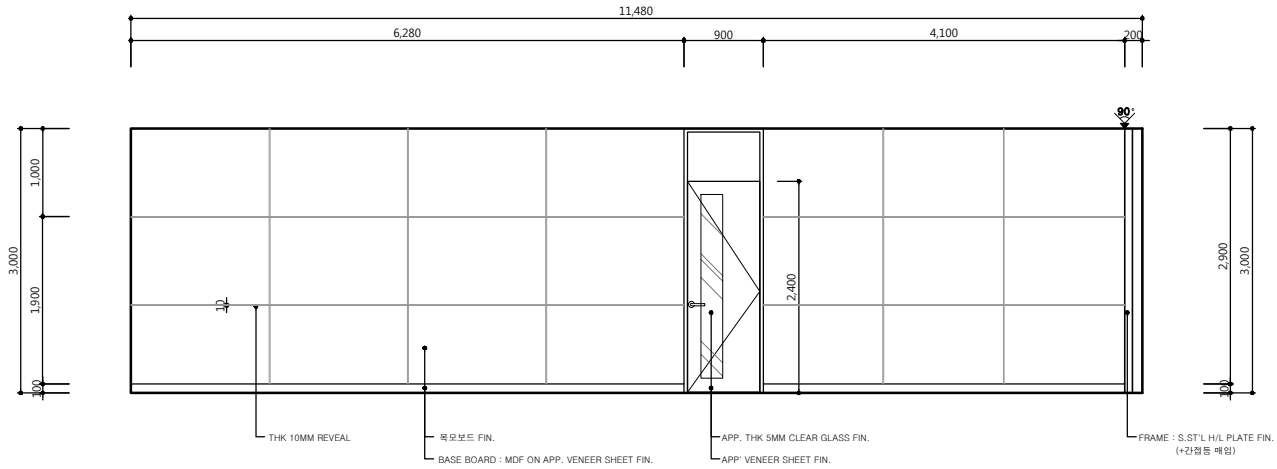

4 ELEVATION D

SCALE 1/60

KORAIL RETAIL

서울시 영등포구 당산3가 2-7
TEL / 02) 2630-8945
FAX / 02) 2630-8926

StoryWay

NOTE / REVISION

NAME OF PROJECT

부산역 5F 회의실

ARCHITECTURE

STRUCTURE

MECHANIC

ELECTRIC

APPROVED BY

DESIGNED BY

DRAWING BY
Park, H. R.

CHECKED BY
Kim, S.C.

DATE
2018. 08.


SCALE
1 / 60

DRAWING TITLE
ELEVATION 02 (회의실 2)

PROJECT NO.


SHEET NO.	DRAWING NO.
202	E-202

Greco DESIGN GROUP
Sukjung Bldg. 2F
203-3 Donggyo-dong,
Mapo-gu, Seoul, Korea. 03992
www.grecodesign.co.kr
T.+82-2-336-2082 F.+82-2-336-2297

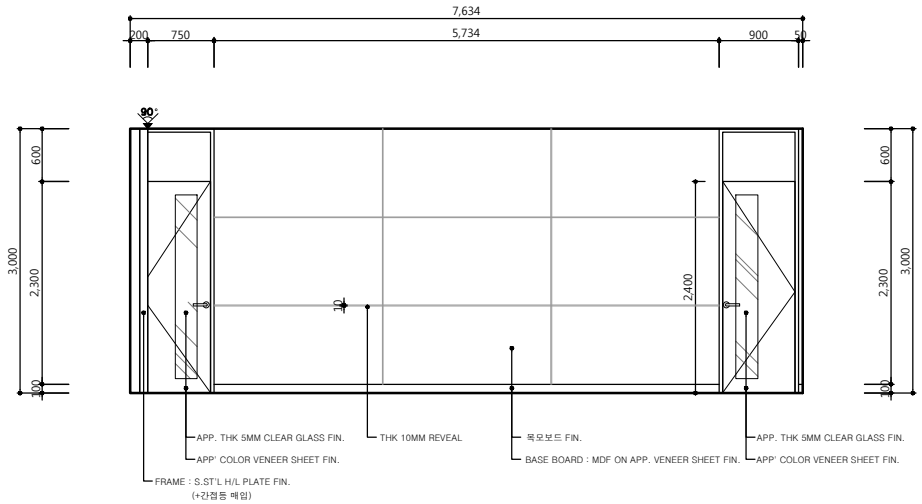

1 ELEVATION A'

SCALE 1/60

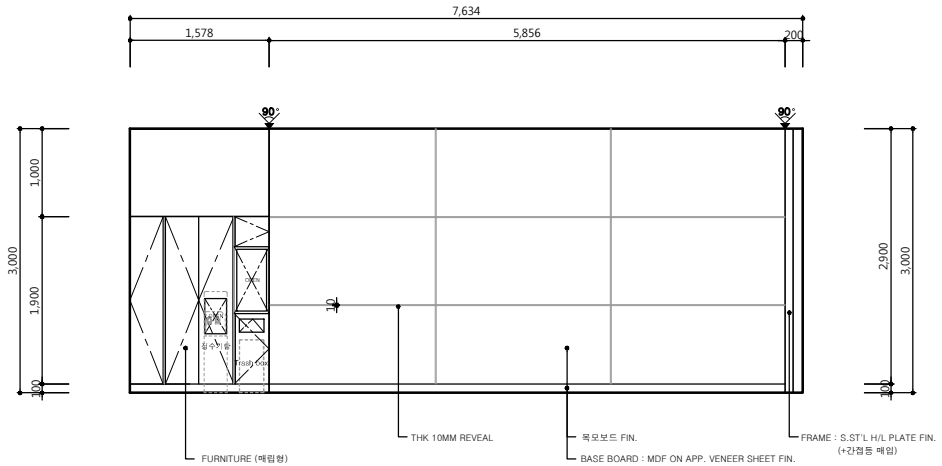

2 ELEVATION B'

SCALE 1/60

KORAIL RETAIL
서울시 영등포구 당산3가 2-7
TEL / 02) 2630-8945
FAX / 02) 2630-8926

StoryWay

NOTE / REVISION

NAME OF PROJECT
부산역 5F 회의실

ARCHITECTURE

STRUCTURE

MECHANIC

ELECTRIC

APPROVED BY

DESIGNED BY

DRAWING BY
Park, H. R.

CHECKED BY
Kim, S.C.

DATE
2018. 08.


SCALE
1 / 60

DRAWING TITLE
ELEVATION 03 (회의실 1)

PROJECT NO.


SHEET NO.	DRAWING NO.
203	E-203

Greco DESIGN GROUP
Sukjung Bldg. 2F
203-3 Donggyo-dong,
Mapo-gu, Seoul, Korea. 03992
www.grecodesign.co.kr
T.+82-2-336-2082 F.+82-2-336-2297

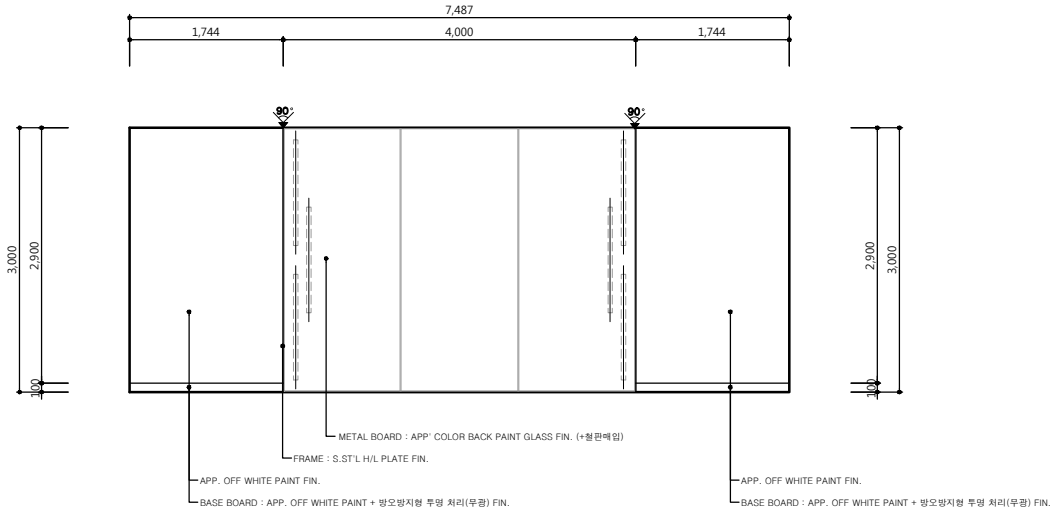

3 ELEVATION C'

SCALE 1/60

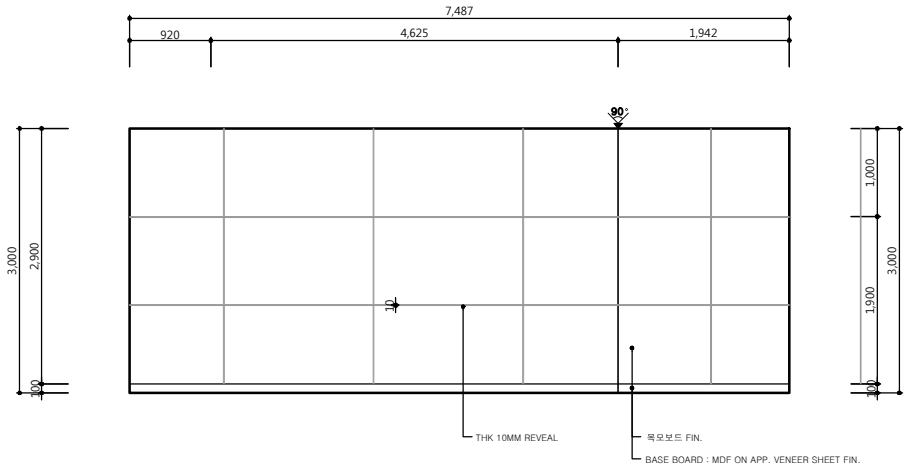

4 ELEVATION D'

SCALE 1/60

KORAIL RETAIL
서울시 영등포구 당산3가 2-7
TEL / 02) 2630-8945
FAX / 02) 2630-8926

StoryWay

NOTE / REVISION

NAME OF PROJECT
부산역 5F 회의실

ARCHITECTURE

STRUCTURE

MECHANIC

ELECTRIC

APPROVED BY

DESIGNED BY

DRAWING BY
Park, H. R.

CHECKED BY
Kim, S.C.

DATE
2018. 08.


SCALE
1 / 60

DRAWING TITLE
ELEVATION 04 (회의실 1)

PROJECT NO.

SHEET NO.	DRAWING NO.
204	E-204

Greco DESIGN GROUP
Sukjung Bldg. 2F
203-3 Donggyo-dong,
Mapo-gu, Seoul, Korea. 03992
www.grecodesign.co.kr
T.+82-2-336-2082 F.+82-2-336-2297

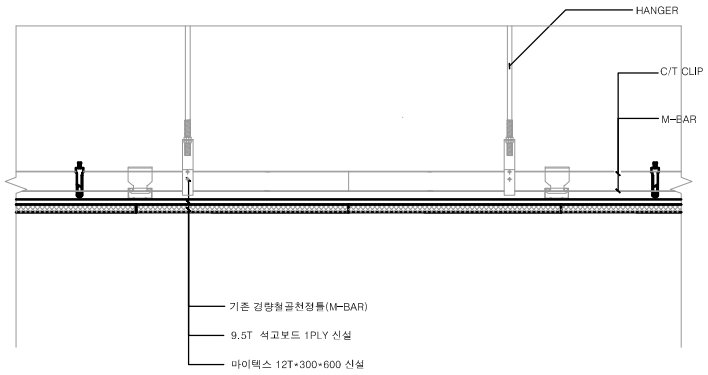

1 LIGHTING BOX (ALT 1._ACRYL BOX TYPE) SCALE 1/10

SCALE 1/10

KORAIL RETAIL
서울시 영등포구 당산3가 2-7
TEL / 02) 2630-8945
FAX / 02) 2630-8926

StoryWay

NOTE / REVISION

NAME OF PROJECT
부산역 5F 회의실 1,2

ARCHITECTURE

STRUCTURE

MECHANIC

ELECTRIC

APPROVED BY

DESIGNED BY

DRAWING BY
Park, H. R.

CHECKED BY
Kim, S.C.

DATE
2018. 11.

SCALE
1 / 10

DRAWING TITLE
LIGHITING BOX (DETAIL)

PROJECT NO.


SHEET NO.
501

DRAWING NO.
D-501

Greco DESIGNGROUP
Sukjung Bldg. 2F
203-3 Donggyo-dong,
Mapo-gu, Seoul, Korea. 03992
www.grecodesign.co.kr
T.+82-2-336-2082 F.+82-2-336-2297

벽체높이 : 2,535

WALL

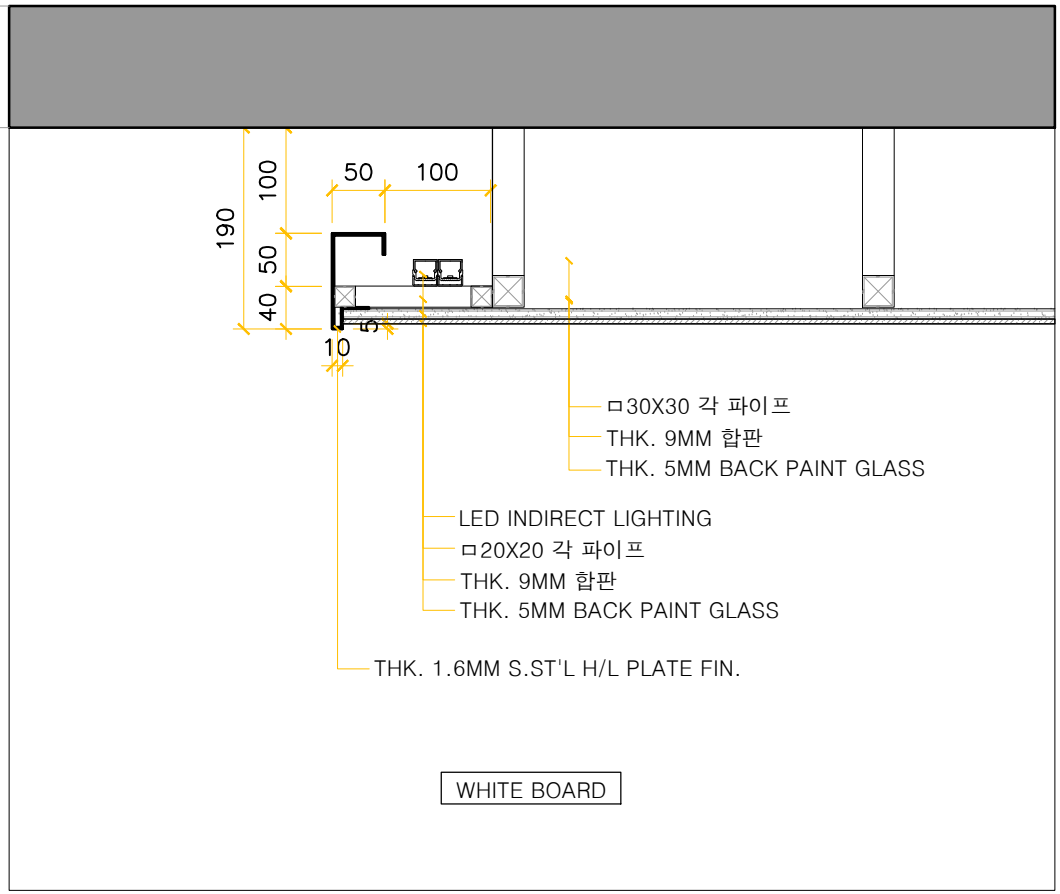

1 화이트 보드 (간접 등박스/FRAME)

SCALE 1/5

KORAIL RETAIL
서울시 영등포구 당산3가 2-7
TEL / 02) 2630-8945
FAX / 02) 2630-8926

StoryWay

NOTE / REVISION

NAME OF PROJECT
부산역 5F 회의실 1,2

ARCHITECTURE

STRUCTURE

MECHANIC

ELECTRIC

APPROVED BY

DESIGNED BY

DRAWING BY
Park, H. R.

CHECKED BY
Kim, S.C.

DATE
2018. 11.

SCALE
1 / 5

DRAWING TITLE
화이트 보드
(간접 등박스, FRAME DETAIL)

PROJECT NO.


SHEET NO.
502

DRAWING NO.
D-502


Greco DESIGN GROUP
Sukjung Bldg. 2F
203-3 Donggyo-dong,
Mapo-gu, Seoul, Korea. 03992
www.grecodesign.co.kr
T.+82-2-336-2082 F.+82-2-336-2297

벽체높이 : 4,230

[평면]

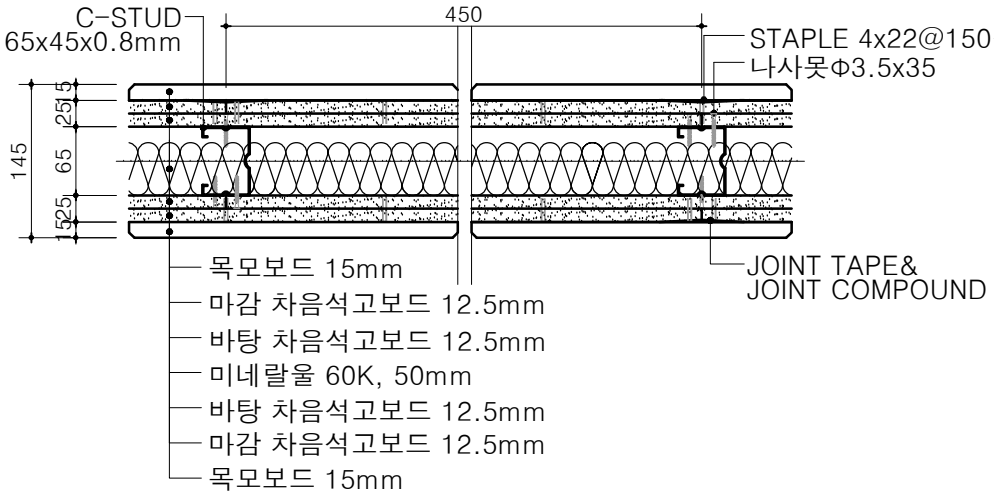

[단면]

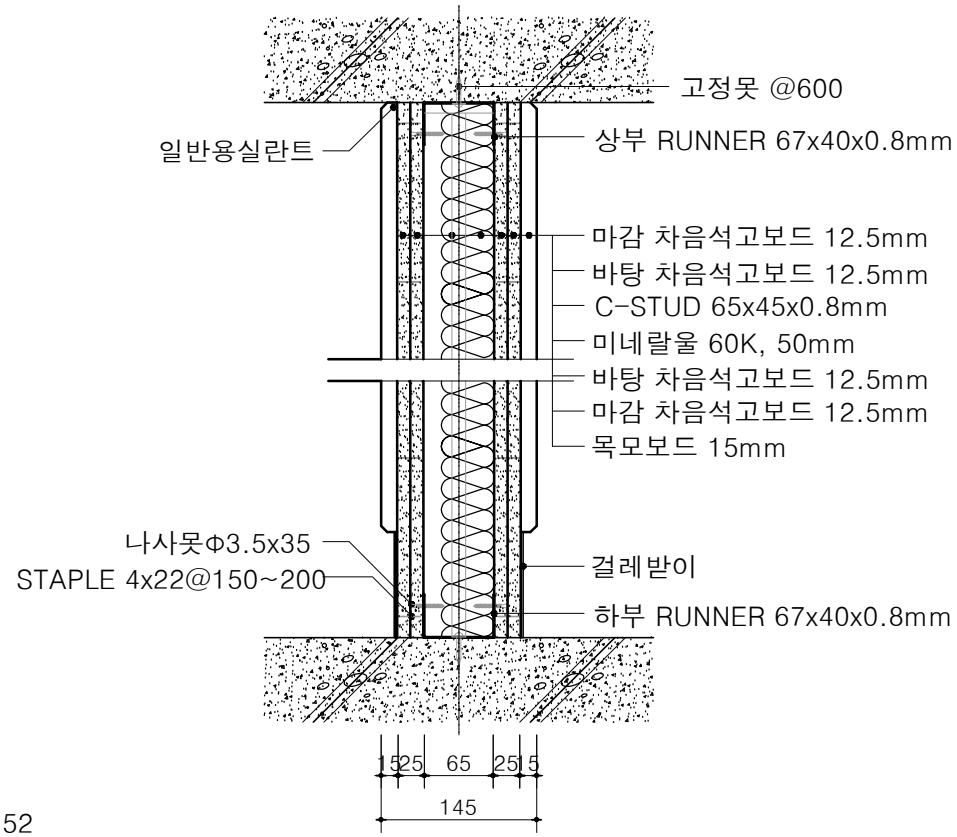

T=115 KCC 차음석고보드 시스템 STC:52

1 차음 석고보드 WALL (회의실)

SCALE 1/5

KORAIL RETAIL
서울시 영등포구 당산3가 2-7
TEL / 02) 2630-8945
FAX / 02) 2630-8926

StoryWay

NOTE / REVISION

NAME OF PROJECT
부산역 5F 회의실 1,2

ARCHITECTURE

STRUCTURE

MECHANIC

ELECTRIC

APPROVED BY

DESIGNED BY

DRAWING BY
Park, H. R.

CHECKED BY
Kim, S.C.

DATE
2018. 11.


SCALE
1 / 5

DRAWING TITLE
차음 석고보드 WALL (회의실)

PROJECT NO.

SHEET NO.	DRAWING NO.
503	D-503

Greco DESIGN GROUP
Sukjung Bldg. 2F
203-3 Donggyo-dong,
Mapo-gu, Seoul, Korea. 03992
www.grecodesign.co.kr
T.+82-2-336-2082 F.+82-2-336-2297

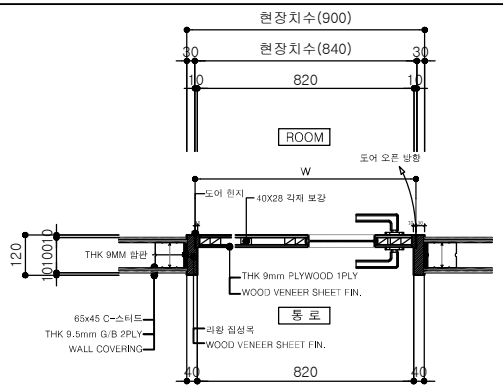


1 TOP VIEW

SCALE 1/20

SYM.	LOCATION	SIZE	DOOR FINISH	HARDWARE (SPEC 참고)
2 WD	회의실 도어	900 x 3000 x 45	APP' COLOR SHEET FIN.	BUTT HINGE-6EA HANDLE-2SET DOOR STOPPER-2EA
		수량	FRAME FINISH	
		2 EA	APP' COLOR SHEET FIN.	


4 LIST

SCALE NONE

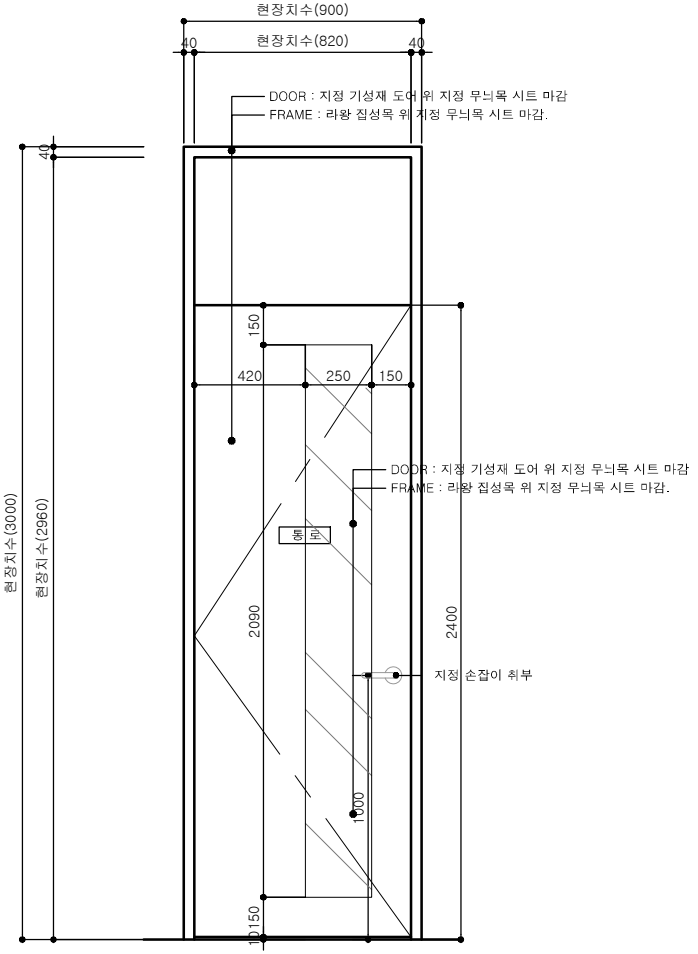

2 FRONT VIEW

SCALE 1/20

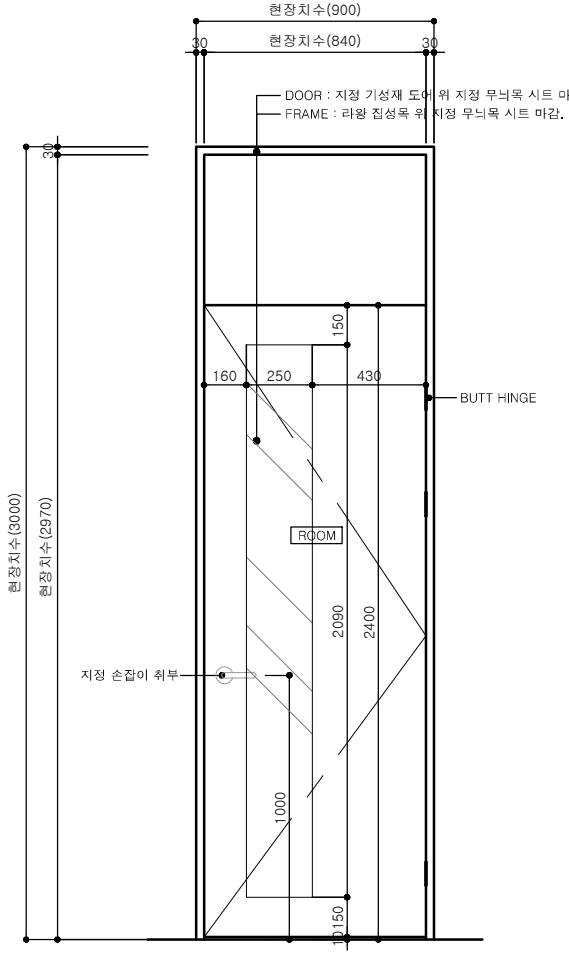

3 INSIDE VIEW

SCALE 1/20

KORAIL RETAIL
서울시 영등포구 당산3가 2-7
TEL / 02) 2630-8945
FAX / 02) 2630-8926
StoryWay

NOTE / REVISION

NAME OF PROJECT
부산역 5F 회의실 1,2

ARCHITECTURE

STRUCTURE

MECHANIC

ELECTRIC

APPROVED BY

DESIGNED BY

DRAWING BY
Park, H. R.

CHECKED BY
Kim, S.C.

DATE
2018. 11.

SCALE
1 / 20

DRAWING TITLE
DOOR DETAIL (회의실 DOOR)


PROJECT NO.


SHEET NO.
504

DRAWING NO.
D-504

Greco DESIGN GROUP
Sukjung Bldg. 2F
203-3 Donggyo-dong,
Mapo-gu, Seoul, Korea. 03992
www.grecodesign.co.kr
T.+82-2-336-2082 F.+82-2-336-2297


※ 기기 사이즈 확인 후 집기 제작 요!

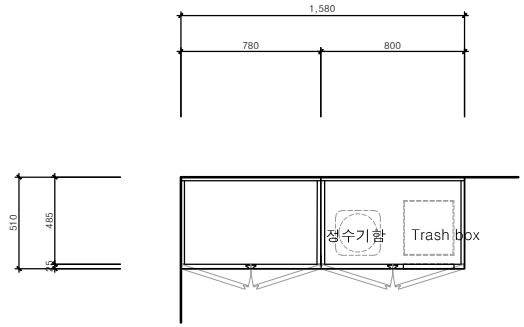

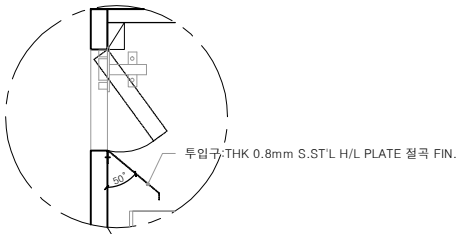


1 TOPVIEW

SCALE 1/30

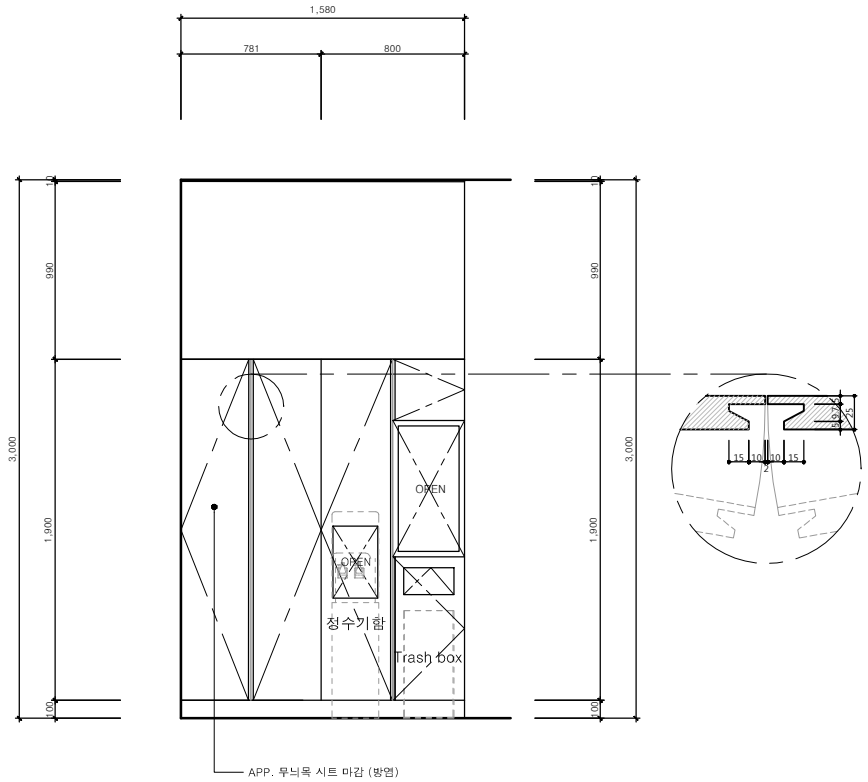

2 FRONTVIEW

SCALE 1/30

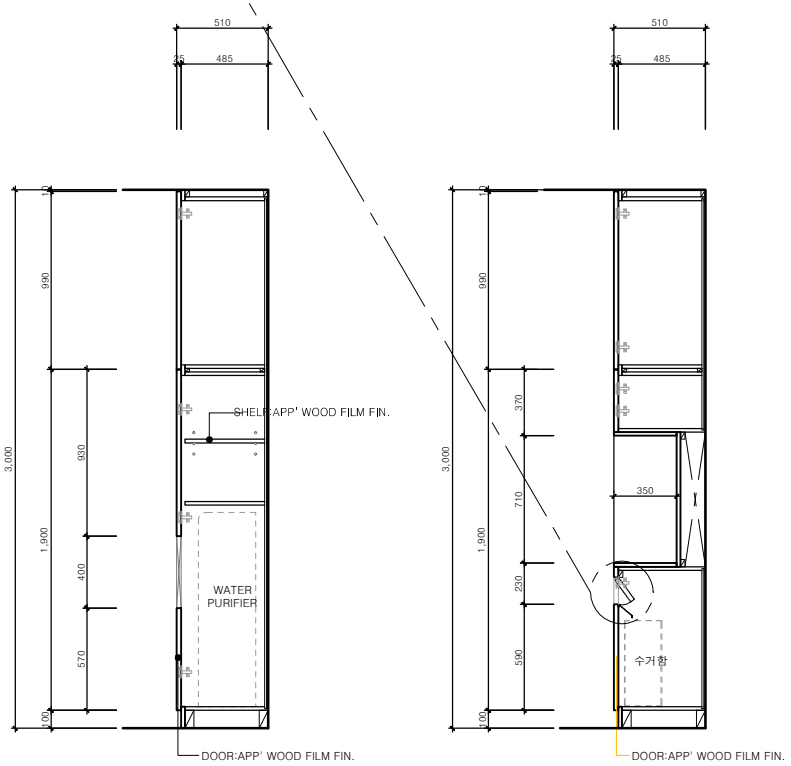

3 SIDESECTION

SCALE 1/30

KORAIL RETAIL

서울시 영등포구 당산3가 2-7
TEL / 02) 2630-8945
FAX / 02) 2630-8926

StoryWay

NOTE / REVISION

NAME OF PROJECT

ARCHITECTURE

STRUCTURE

MECHANIC

ELECTRIC

APPROVED BY

DESIGNED BY

DRAWING BY

CHECKED BY

DATE

SCALE
1 / 30


DRAWING TITLE
FURNITURE(Built-in)
회의실 1.

PROJECT NO.

SHEET NO.	DRAWING NO.
505	F-505


Greco DESIGN GROUP
Sukjung Bldg. 2F
203-3 Donggyo-dong,
Mapo-gu, Seoul, Korea. 03992
www.grecodesign.co.kr
T.+82-2-336-2082 F.+82-2-336-2297

※ 기기 사이즈 확인 후 집기 제작 요!

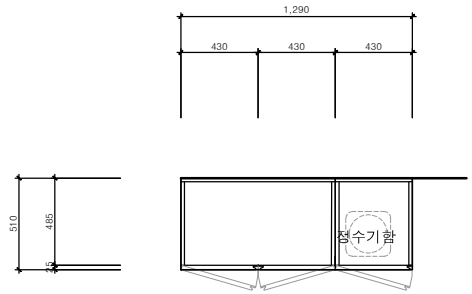


1 TOPVIEW

SCALE 1/30

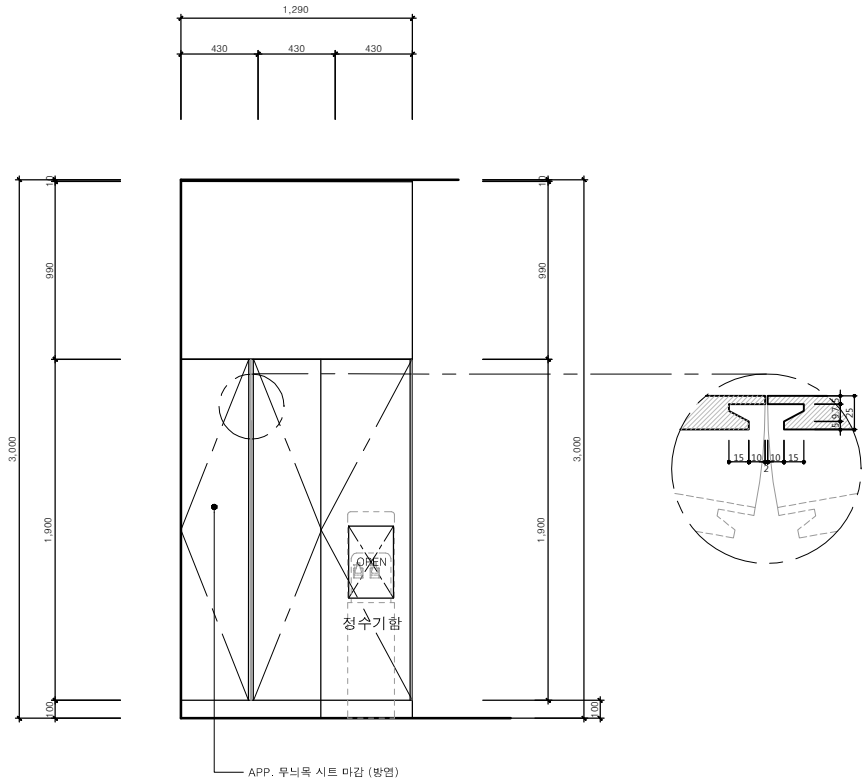

2 FRONTVIEW

SCALE 1/30

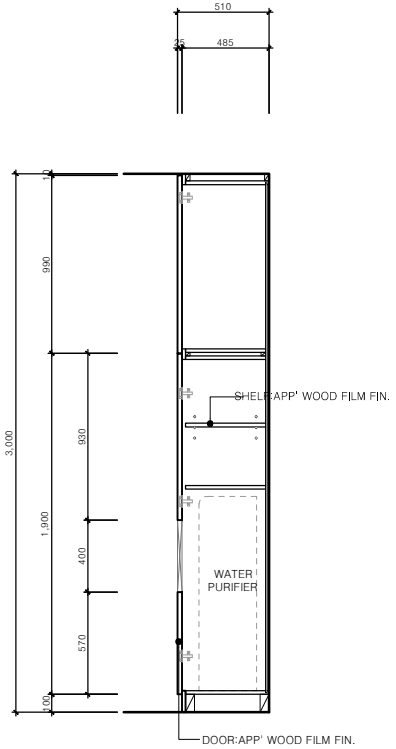

3 SIDESECTION

SCALE 1/30

KORAIL RETAIL
서울시 영등포구 당산3가 2-7
TEL / 02) 2630-8945
FAX / 02) 2630-8926

StoryWay

NOTE / REVISION

NAME OF PROJECT

ARCHITECTURE

STRUCTURE

MECHANIC

ELECTRIC

APPROVED BY

DESIGNED BY

DRAWING BY

CHECKED BY

DATE

SCALE
1 / 30

DRAWING TITLE
FURNITURE(Built-in)
(회의실 2.)

PROJECT NO.

SHEET NO.	DRAWING NO.
506	F-506

Greco DESIGN GROUP
Sukjung Bldg. 2F
203-3 Donggyo-dong,
Mapo-gu, Seoul, Korea. 03992
www.grecodesign.co.kr
T.+82-2-336-2082 F.+82-2-336-2297