RETAIL

KORAIL

부산역 3층맛이방 전문점 2개소 신축공사

2017. 02.

코레일유통(주)

■ DRAWING LIST

SHEET NO.	DRAWING NO.	DRAWING TITLE	SCALE	REMARK	SHEET NO.	DRAWING NO.	DRAWING TITLE	SCALE	REMARK
001	L-001	표지	NONE						
002	L-002	도면목록표	NONE						
003	I-001	가설 평면도	1/200						
004	I-002	구조틀(벽/천정) 평면도	1/100						
005	I-003	지붕 평면도	1/100						
006	I-004	골조 입면도 -A,B	1/50						
007	I-005	입면도 -A,B	1/50						
008	I-006	입면도 -C,D	1/50						
009	I-007	벽 구조틀 평면도	1/100						
010	I-008	천정 구조틀 평면도	1/100						
011	I-009	지붕 평면도	1/100						
012	I-010	골조 입면도 -A,D	1/100						
013	I-011	입면도 -A,B	1/100						
014	I-012	입면도 -C,D	1/100						
DETAIL									
015	D-01	천정 구조 트러스 상세도	1/30						
016	D-02	출입구 단면상세도 -1	1/15						
017	D-03	벽체 단면상세도	1/15						
018	D-04	유리벽 접합 상세도	1/1						

StoryWay

NOTE / REVISION

ROOF C.H. : 3,650

NAME OF PROJECT

부산역 3층 맞이방 전문점

ARCHITECTURE

STRUCTURE

MECHANIC

ELECTRIC

APPROVED BY

DESIGNED BY

DRAWING BY

CHECKED BY

DATE 2017. 02

SCALE A3 - 1 / none

DRAWING TITLE 도면목록표

PROJECT NO.


SHEET NO. 001 | SHEET NO. L-002

KORAIL RETAIL

서울시 영등포구 당산3가 2-7
TEL / 02) 2630-8945
FAX / 02) 2630-8926

1 도면목록표

SCALE none

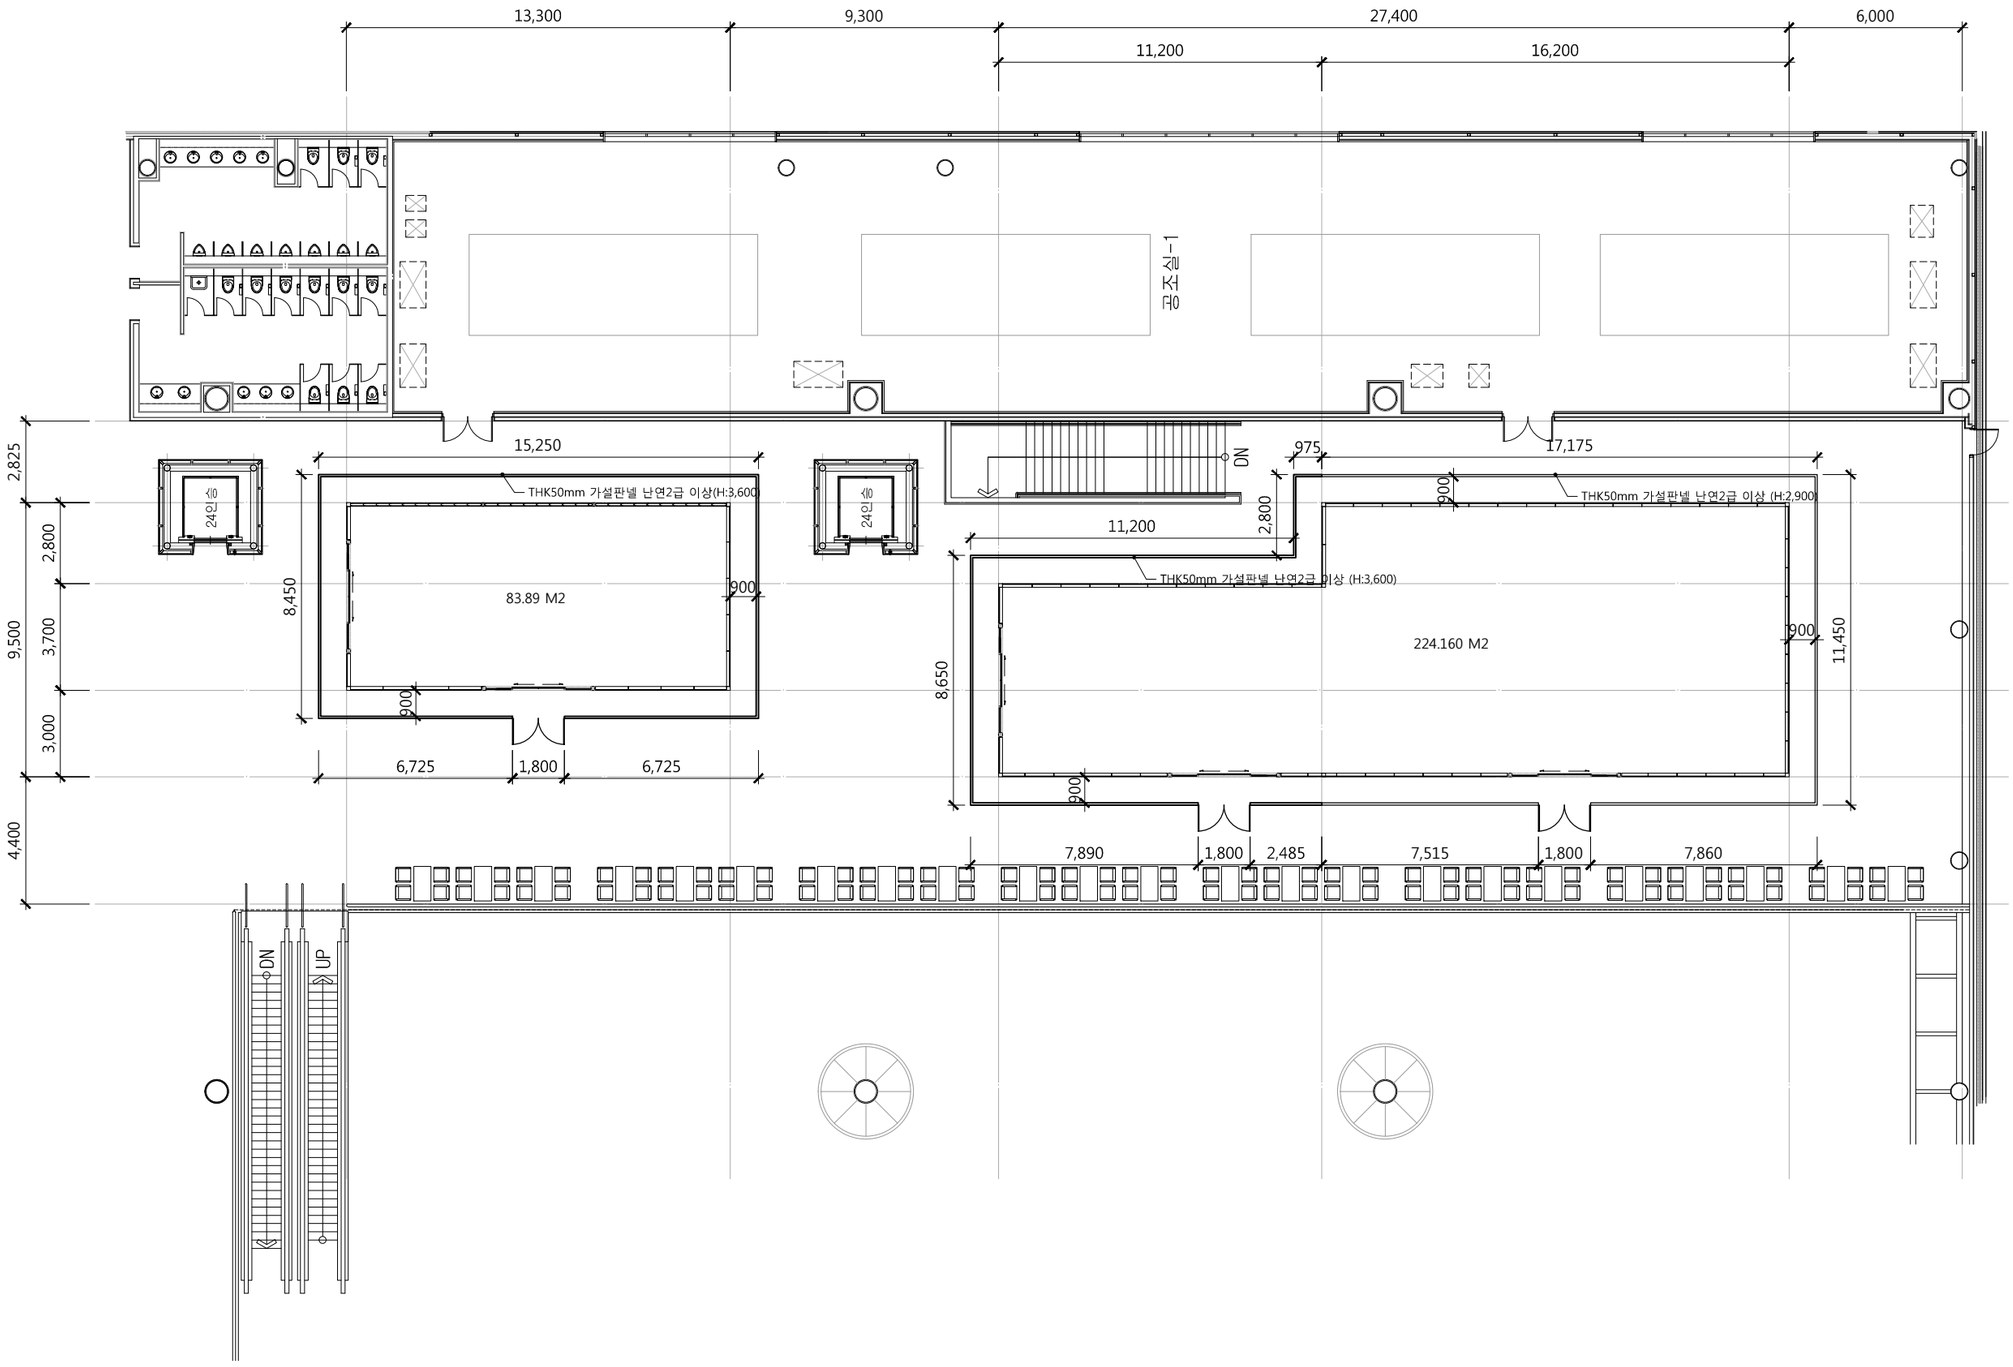

1 가설 평면도

SCALE 1 / 200

StoryWay

NOTE / REVISION

ROOF C.H. : 3,650

NAME OF PROJECT

부산역 3층맞이방 전문점

ARCHITECTURE

STRUCTURE

MECHANIC

ELECTRIC

APPROVED BY

DESIGNED BY

DRAWING BY

CHECKED BY

DATE 2017. 02

SCALE A3 - 1 / 200


DRAWING TITLE 가설 평면도

PROJECT NO.

SHEET NO. 000


SHEET NO. I-001

KORAIL RETAIL
서울시 영등포구 당산3가 2-7
TEL / 02) 2630-8945
FAX / 02) 2630-8926

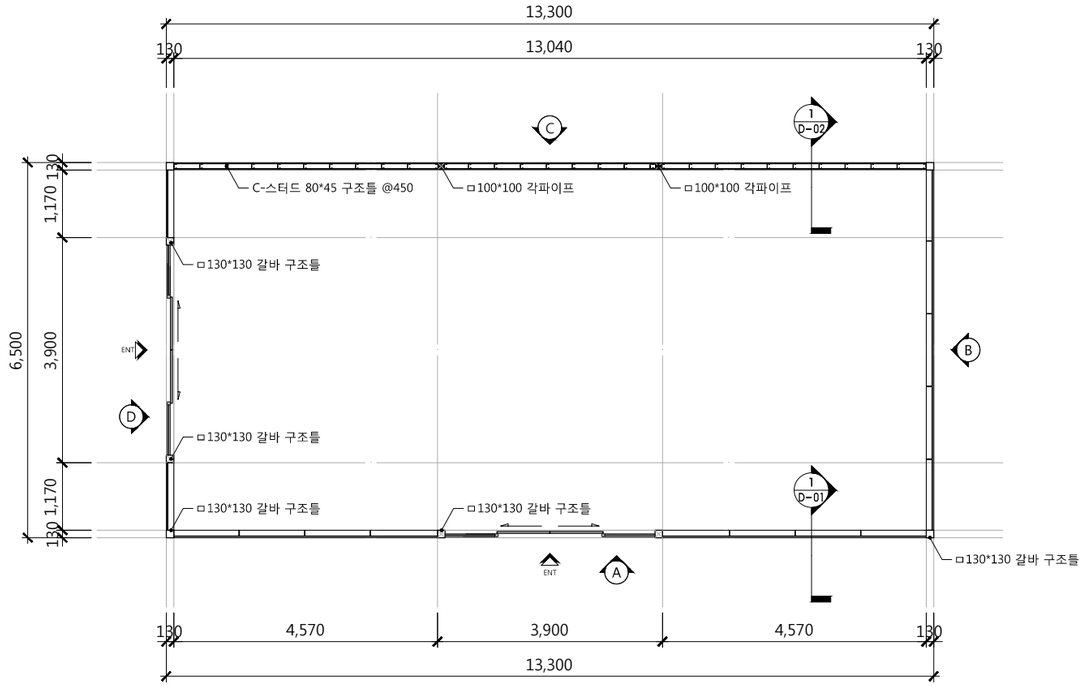

1 확대 평면도

SCALE 1 / 100

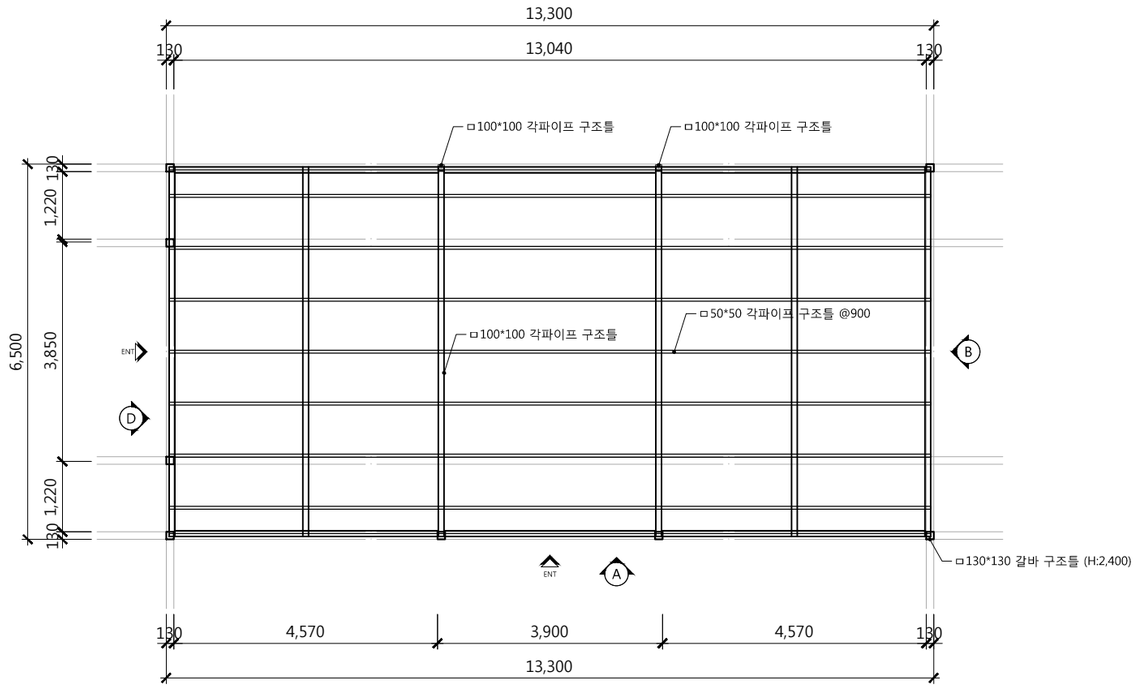

2 천정 구조틀 평면도

SCALE 1 / 100

StoryWay

NOTE / REVISION

ROOF C.H. : 3,650

NAME OF PROJECT

부산역 3층맞이방 전문점 신축공사

ARCHITECTURE

STRUCTURE

MECHANIC

ELECTRIC

APPROVED BY

DESIGNED BY

DRAWING BY

CHECKED BY

DATE 2017. 01

SCALE A3 - 1 / 100

DRAWING TITLE

구조틀(벽/천정) 평면도


PROJECT NO.

SHEET NO. 000

SHEET NO. I-002

KORAIL RETAIL

서울시 영등포구 당산3가 2-7
TEL / 02) 2630-8945
FAX / 02) 2630-8926

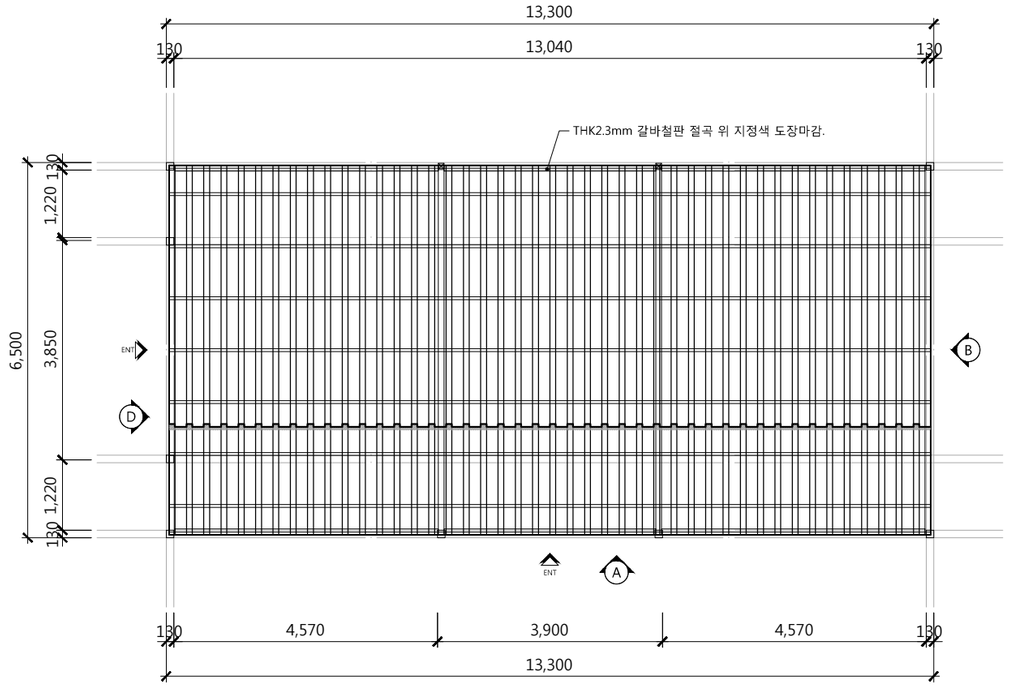

1 지붕 평면도

SCALE 1 / 100

2

SCALE 1 / 100

NOTE / REVISION

ROOF C.H. : 3,650

NAME OF PROJECT

부산역 3층맞이방 전문점 신축공사

ARCHITECTURE

STRUCTURE

MECHANIC

ELECTRIC

APPROVED BY

DESIGNED BY

DRAWING BY

CHECKED BY

DATE 2017. 01

SCALE A3 - 1 / 100


DRAWING TITLE 지붕 평면도

PROJECT NO.

SHEET NO. 000


SHEET NO. I-003

서울시 영등포구 당산3가 2-7
TEL / 02) 2630-8945
FAX / 02) 2630-8926

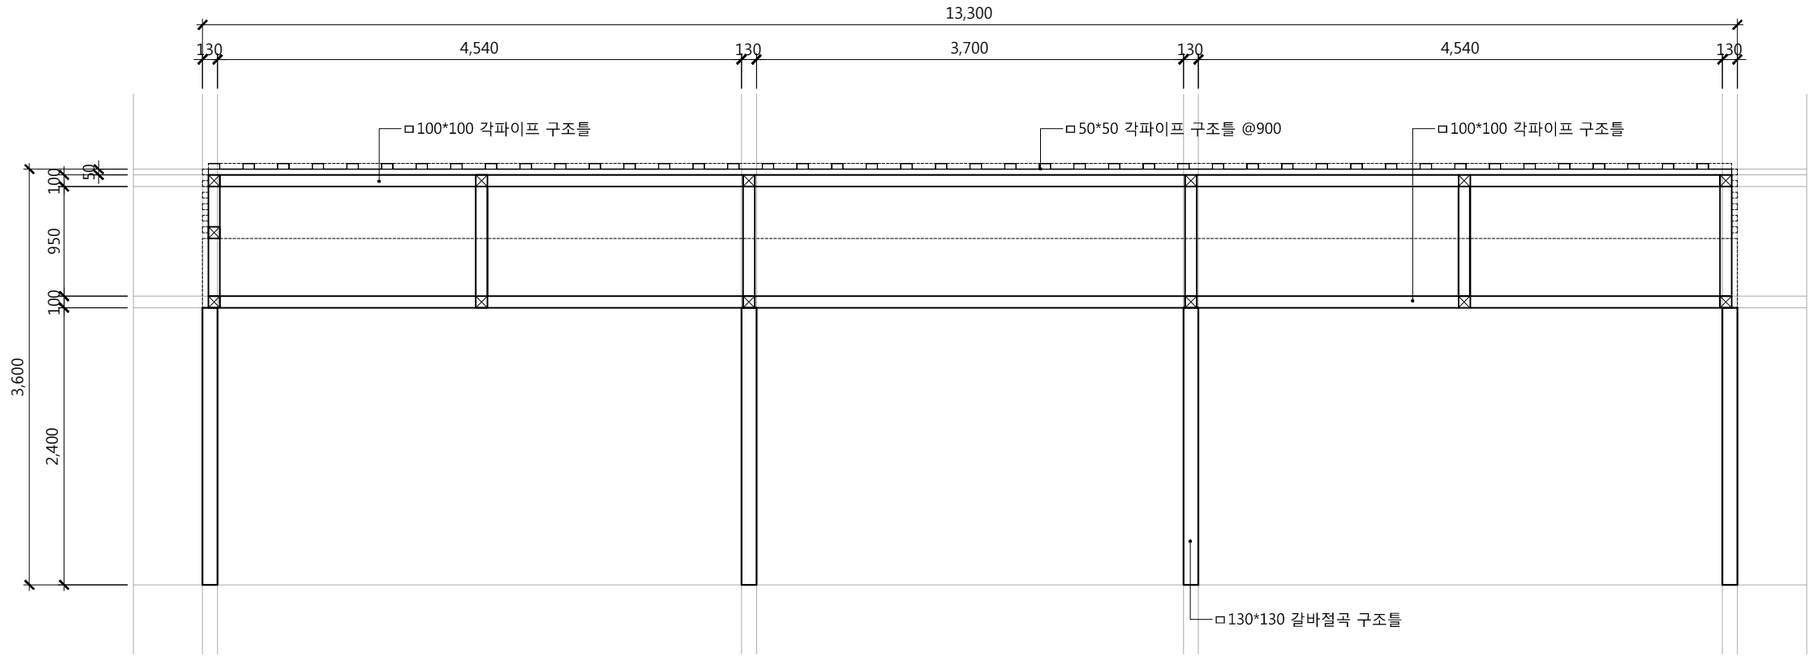

1 골조 입면도 -A

SCALE 1 / 50

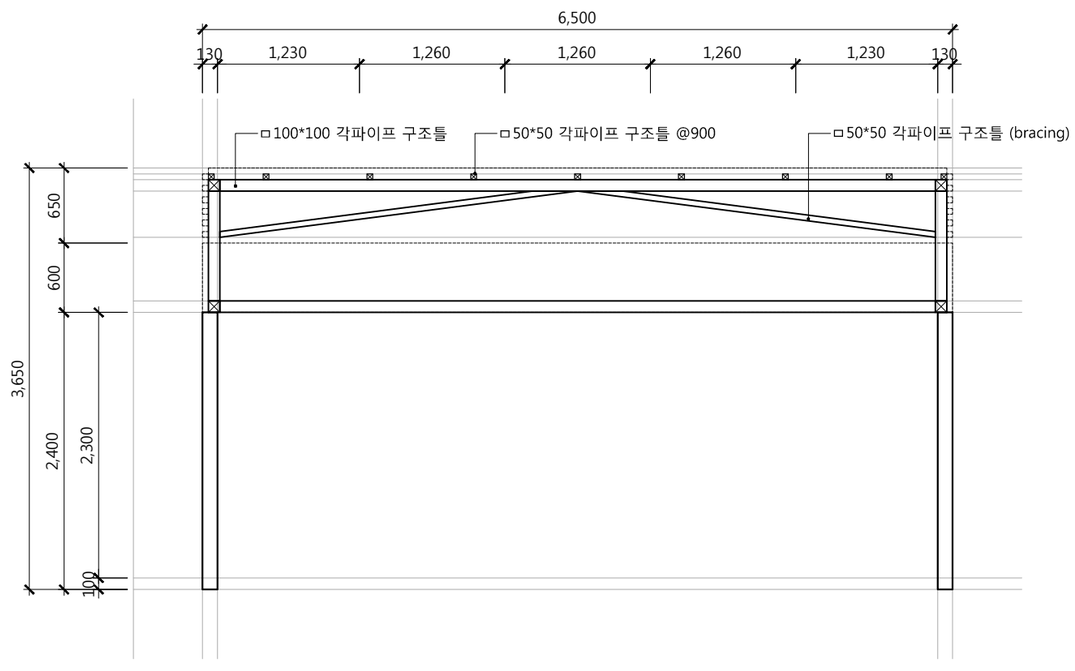

2 골조 입면도 -B

SCALE 1 / 50

StoryWay

NOTE / REVISION

ROOF C.H. : 3,650

NAME OF PROJECT

부산역 3층맞이방 전문점 신축공사

ARCHITECTURE

STRUCTURE

MECHANIC

ELECTRIC

APPROVED BY

DESIGNED BY

DRAWING BY

CHECKED BY

DATE 2017. 01

SCALE A3 - 1 / 50

DRAWING TITLE

골조 입면도 -A,B


PROJECT NO.

SHEET NO. 000

SHEET NO. I-004


KORAIL RETAIL

서울시 영등포구 당산3가 2-7
TEL / 02) 2630-8945
FAX / 02) 2630-8926

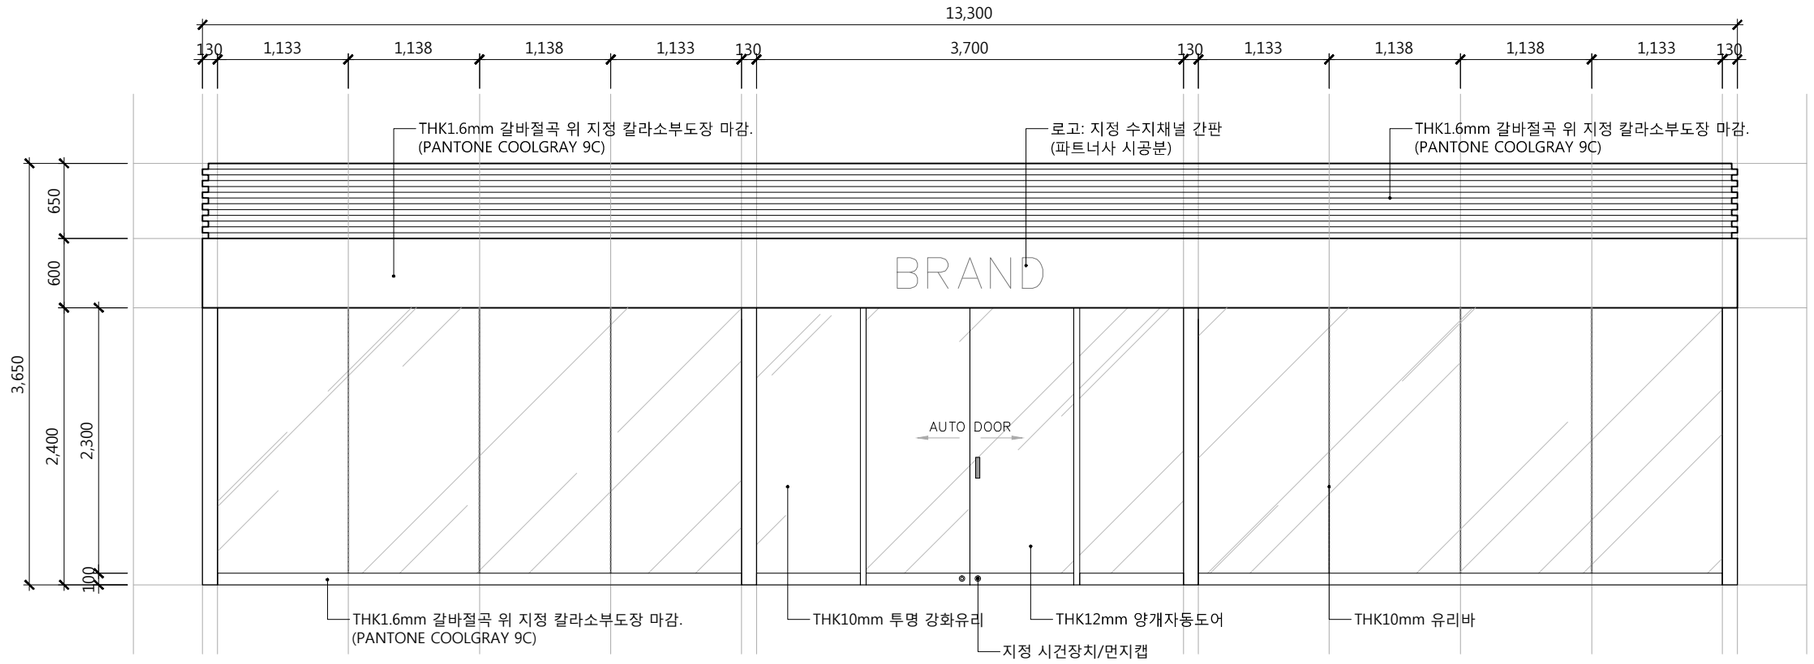

1 입면도 -A

SCALE 1 / 50

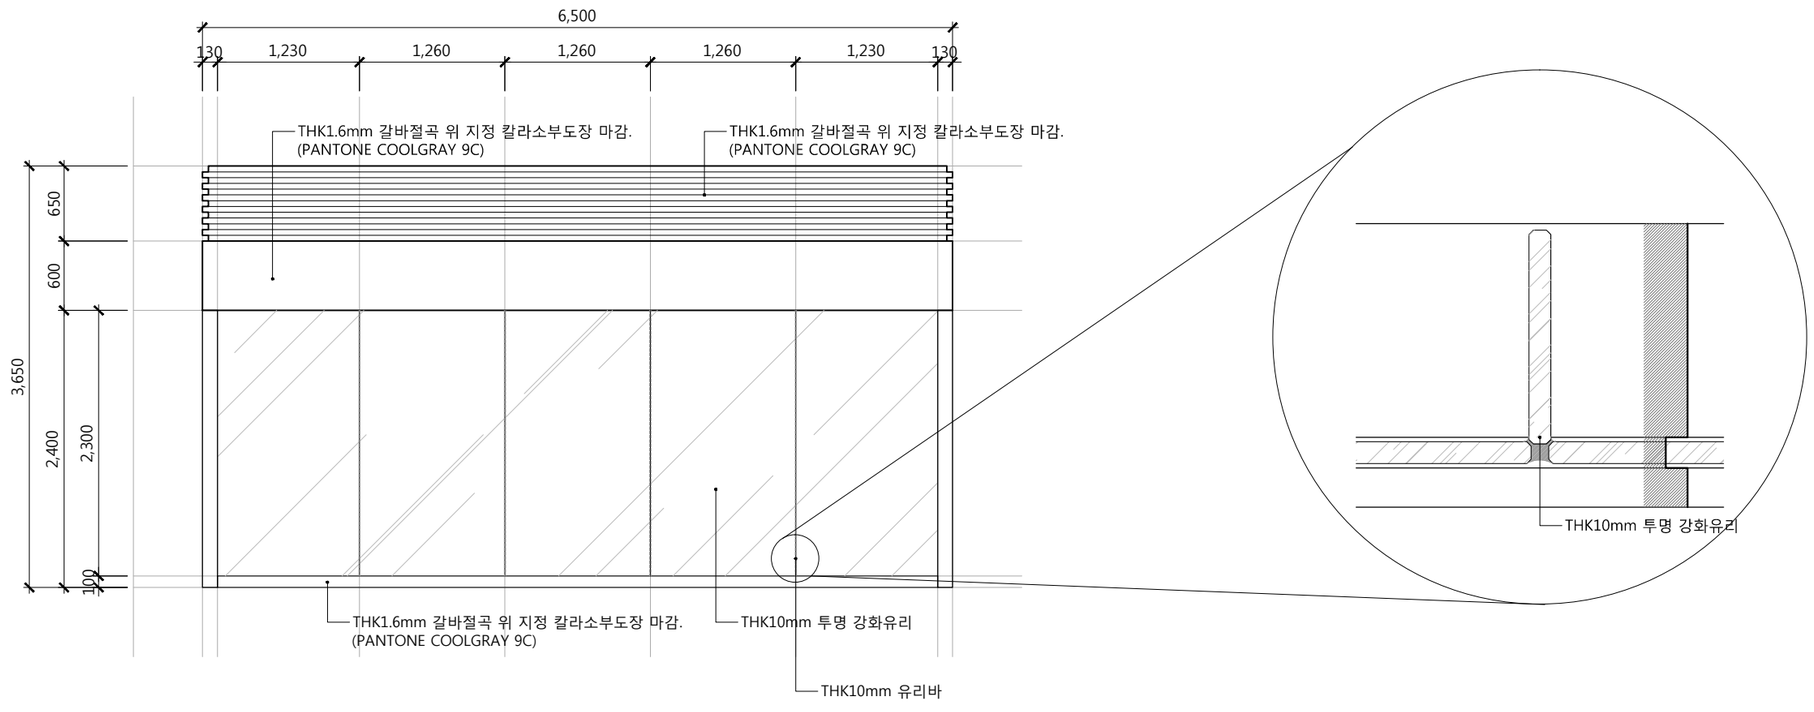

2 입면도 -B

SCALE 1 / 50

StoryWay

NOTE / REVISION

ROOF C.H. : 3,650

NAME OF PROJECT

부산역 3층맞이방 전문점
신축공사

ARCHITECTURE

STRUCTURE

MECHANIC

ELECTRIC

APPROVED BY

DESIGNED BY

DRAWING BY

CHECKED BY

DATE 2017. 01

SCALE A3 - 1 / 50

DRAWING TITLE


입면도 -A,B

PROJECT NO.

SHEET NO. 000


SHEET NO. I-005

KORAIL RETAIL
서울시 영등포구 당산3가 2-7
TEL / 02) 2630-8945
FAX / 02) 2630-8926

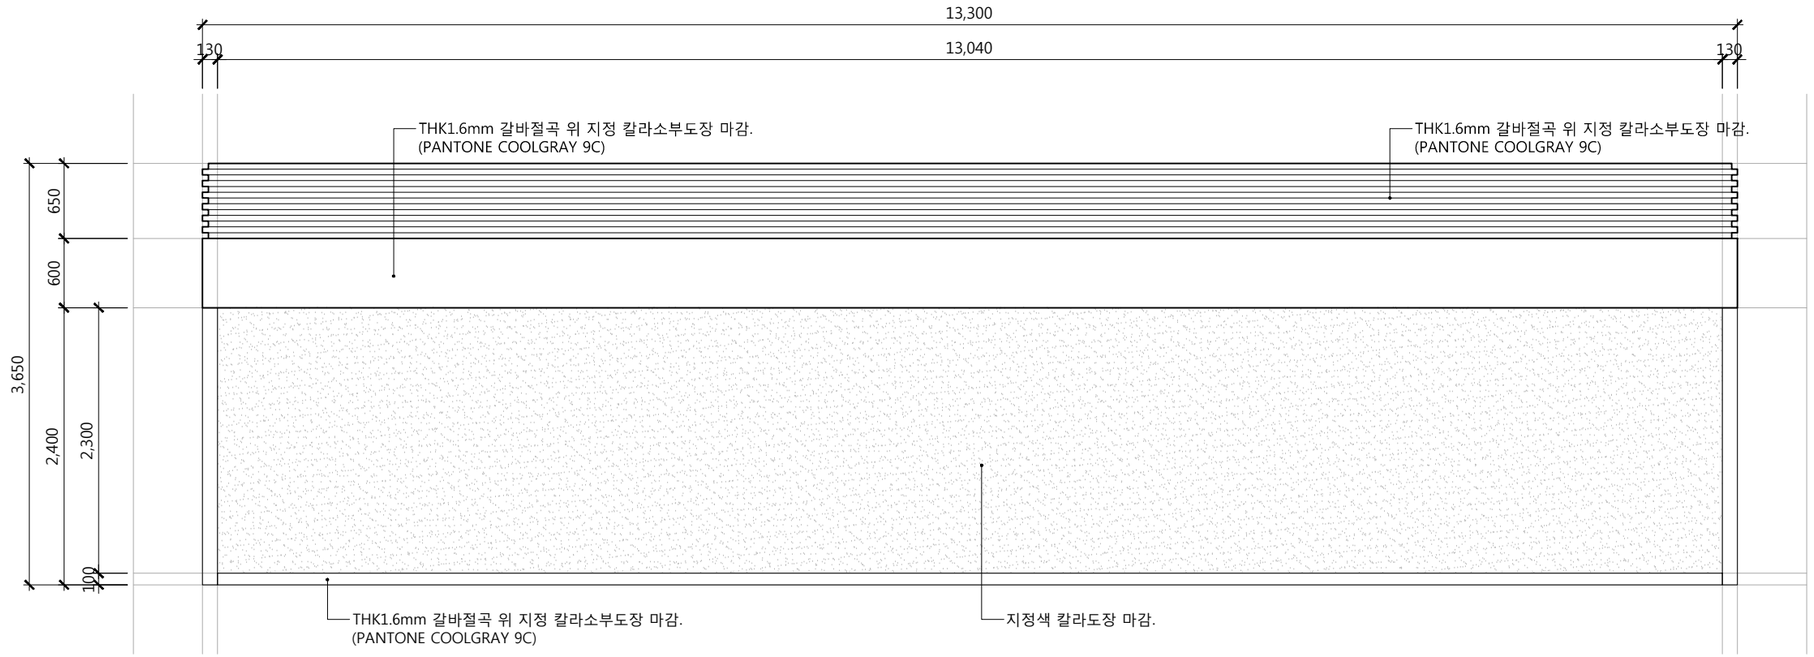

1 입면도 -C

SCALE 1 / 50

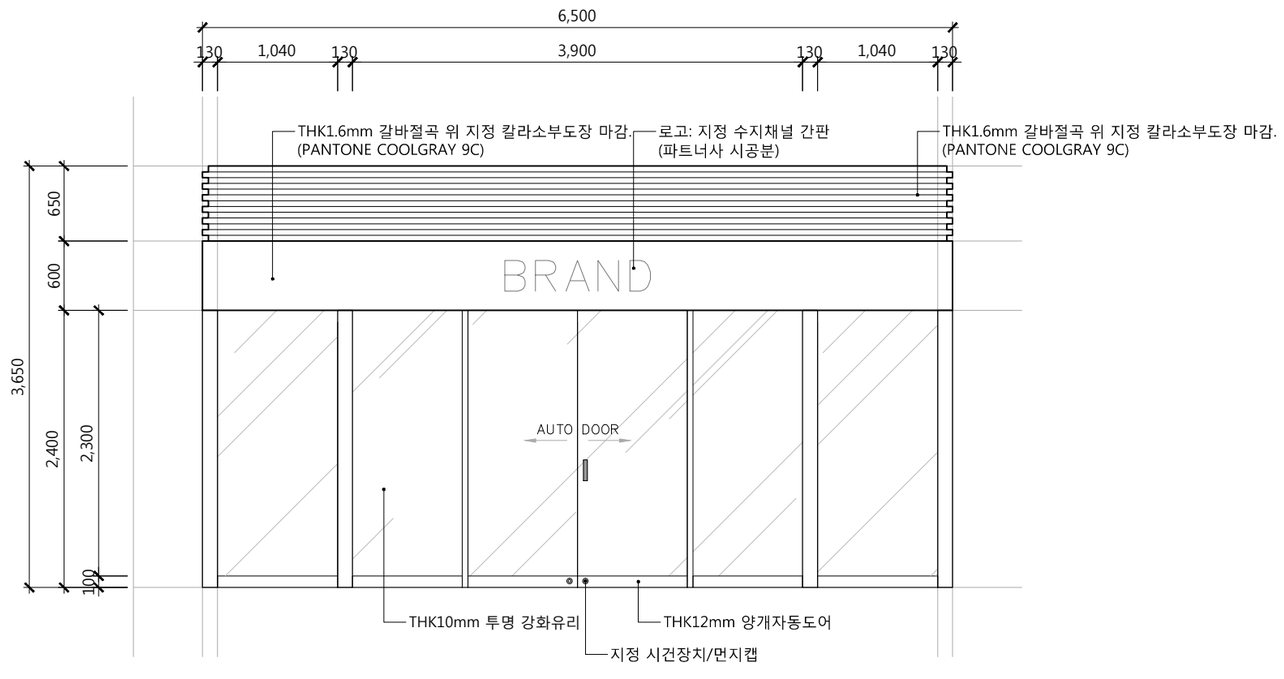

2 입면도 -D

SCALE 1 / 50

StoryWay

NOTE / REVISION

ROOF C.H. : 3,650

NAME OF PROJECT

부산역 3층맞이방 전문점
신축공사

ARCHITECTURE

STRUCTURE

MECHANIC

ELECTRIC

APPROVED BY

DESIGNED BY

DRAWING BY

CHECKED BY

DATE 2017. 01

SCALE A3 - 1 / 50

DRAWING TITLE

입면도 -C,D


PROJECT NO.

SHEET NO. 000

SHEET NO. I-006

KORAIL RETAIL

서울시 영등포구 당산3가 2-7
TEL / 02) 2630-8945
FAX / 02) 2630-8926

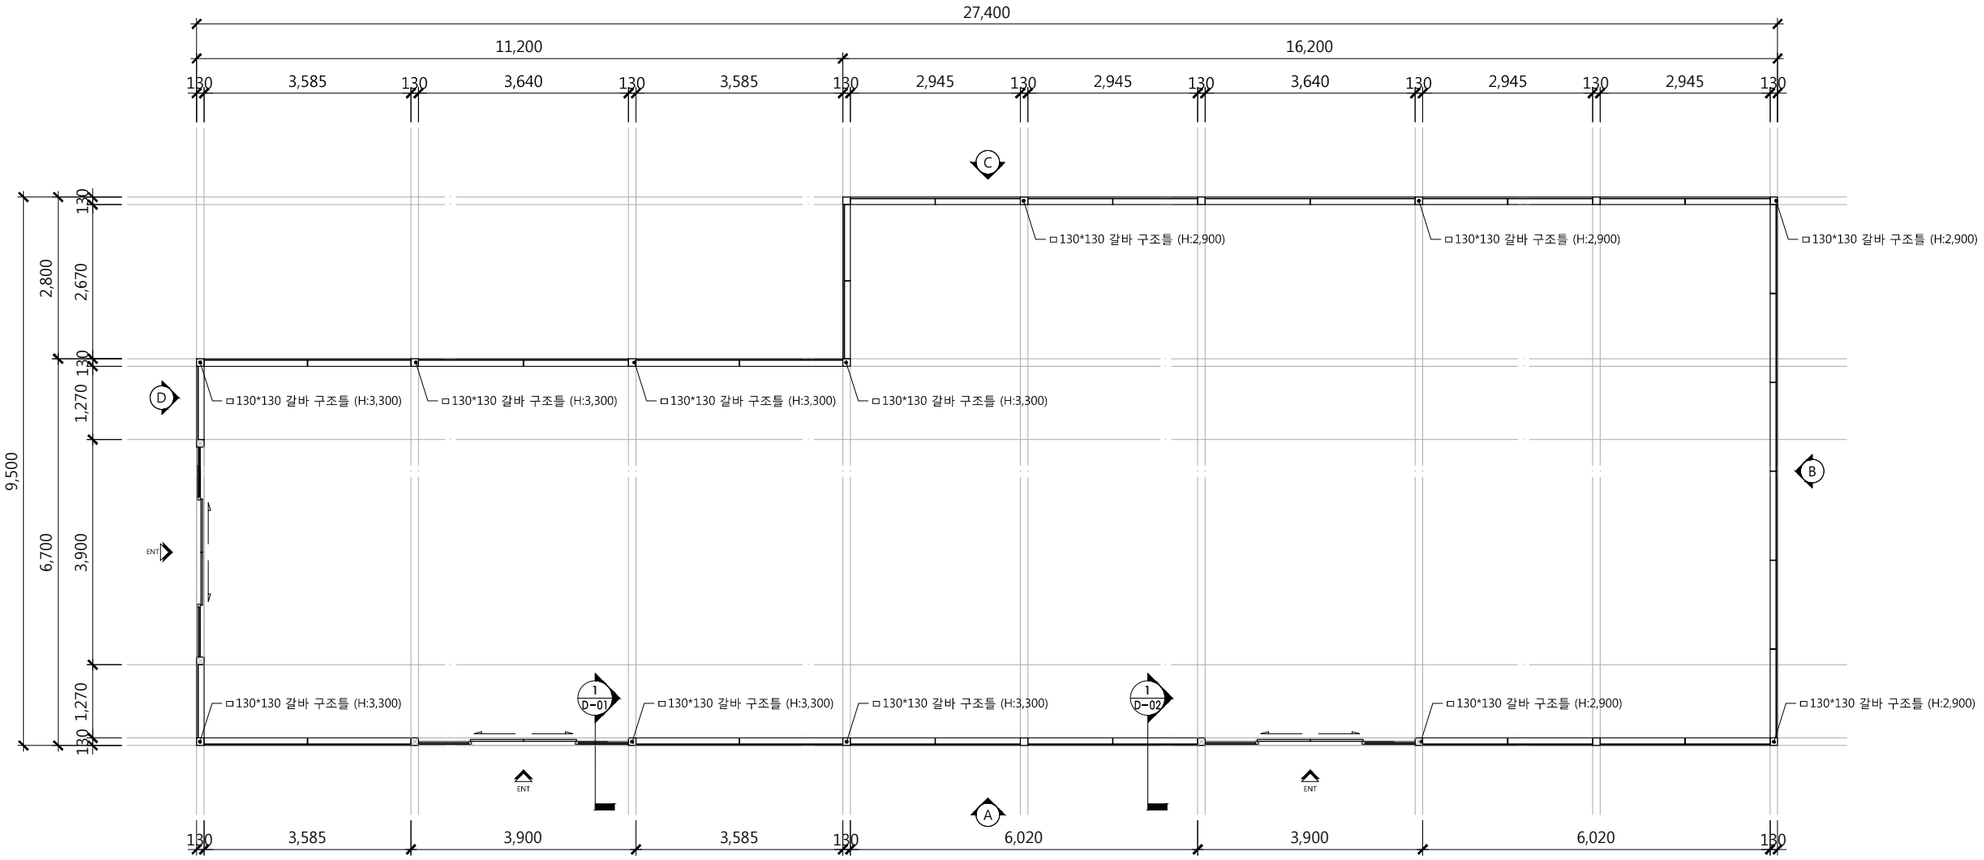

1 벽 구조틀 평면도

SCALE 1 / 100

NOTE / REVISION

ROOF C.H. : 3,650 / 2,900

NAME OF PROJECT

부산역 3층맞이방 전문점 신축공사

ARCHITECTURE

STRUCTURE

MECHANIC

ELECTRIC

APPROVED BY

DESIGNED BY

DRAWING BY

CHECKED BY

DATE 2017. 01

SCALE A3 - 1 / 100

DRAWING TITLE


벽 구조틀 평면도

PROJECT NO.

SHEET NO. 000

SHEET NO. I-007

서울시 영등포구 당산3가 2-7
TEL / 02) 2630-8945
FAX / 02) 2630-8926

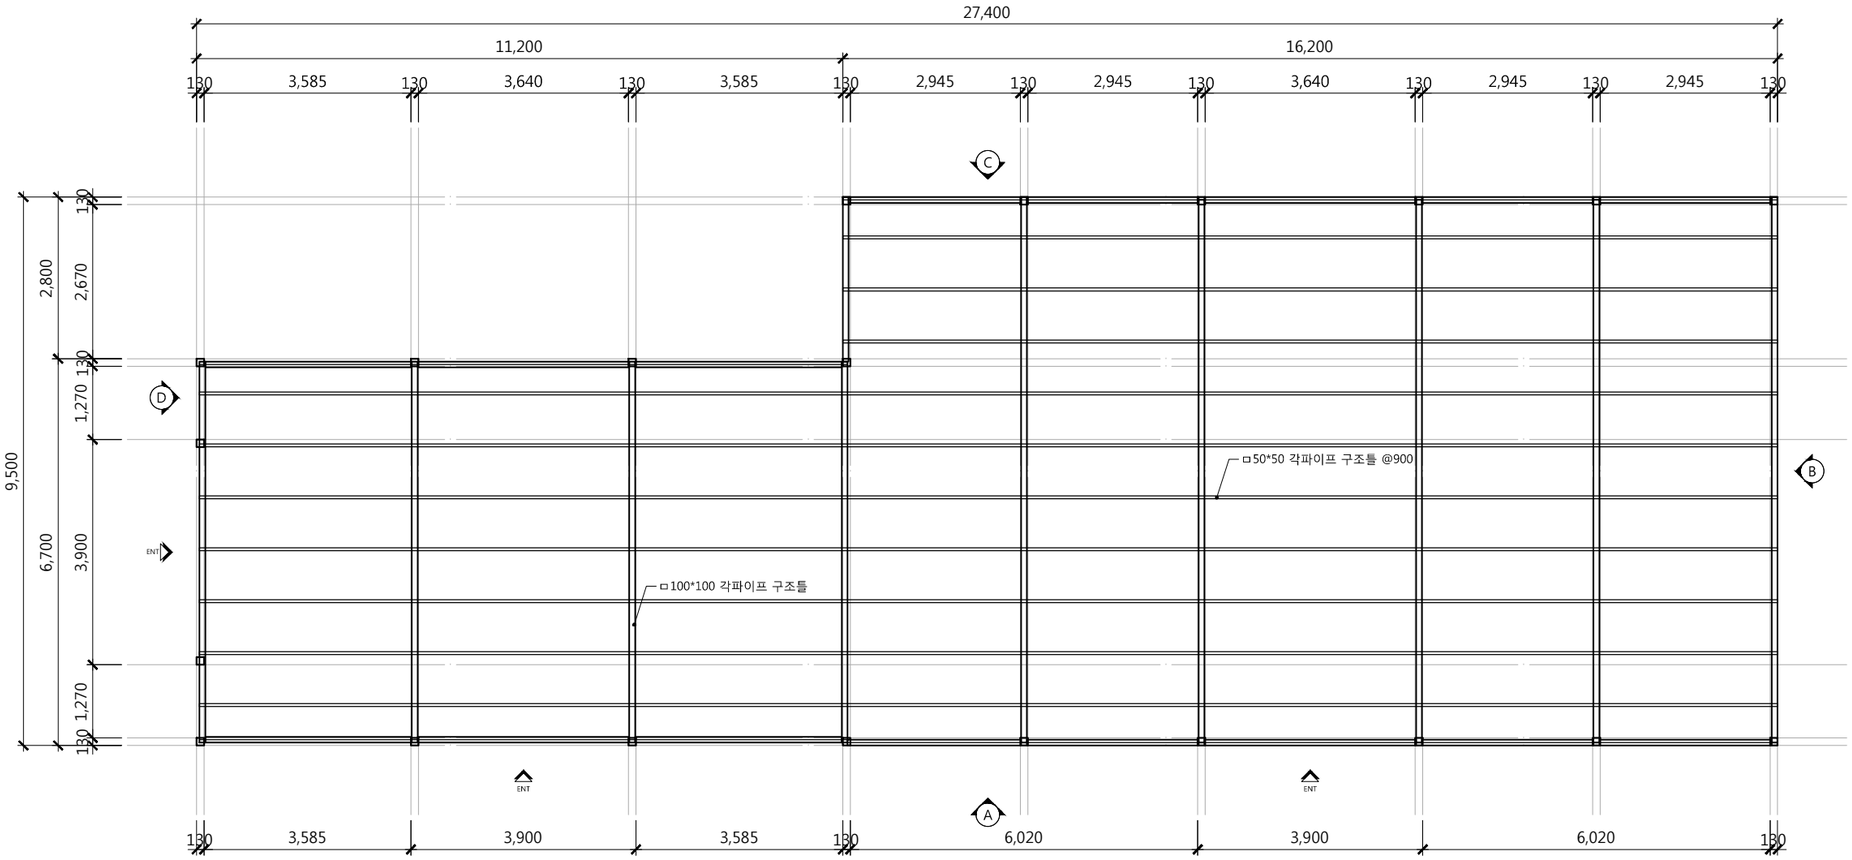

1 천정 구조틀 평면도

SCALE 1 / 100

StoryWay

NOTE / REVISION

ROOF C.H. : 3,650 / 2,900

NAME OF PROJECT

부산역 3층맞이방 전문점 신축공사

ARCHITECTURE

STRUCTURE

MECHANIC

ELECTRIC

APPROVED BY

DESIGNED BY

DRAWING BY

CHECKED BY

DATE 2017. 01

SCALE A3 - 1 / 100

DRAWING TITLE

천정 구조틀 평면도


PROJECT NO.

SHEET NO. 000

SHEET NO. I-008

KORAIL RETAIL

서울시 영등포구 당산3가 2-7
TEL / 02) 2630-8945
FAX / 02) 2630-8926

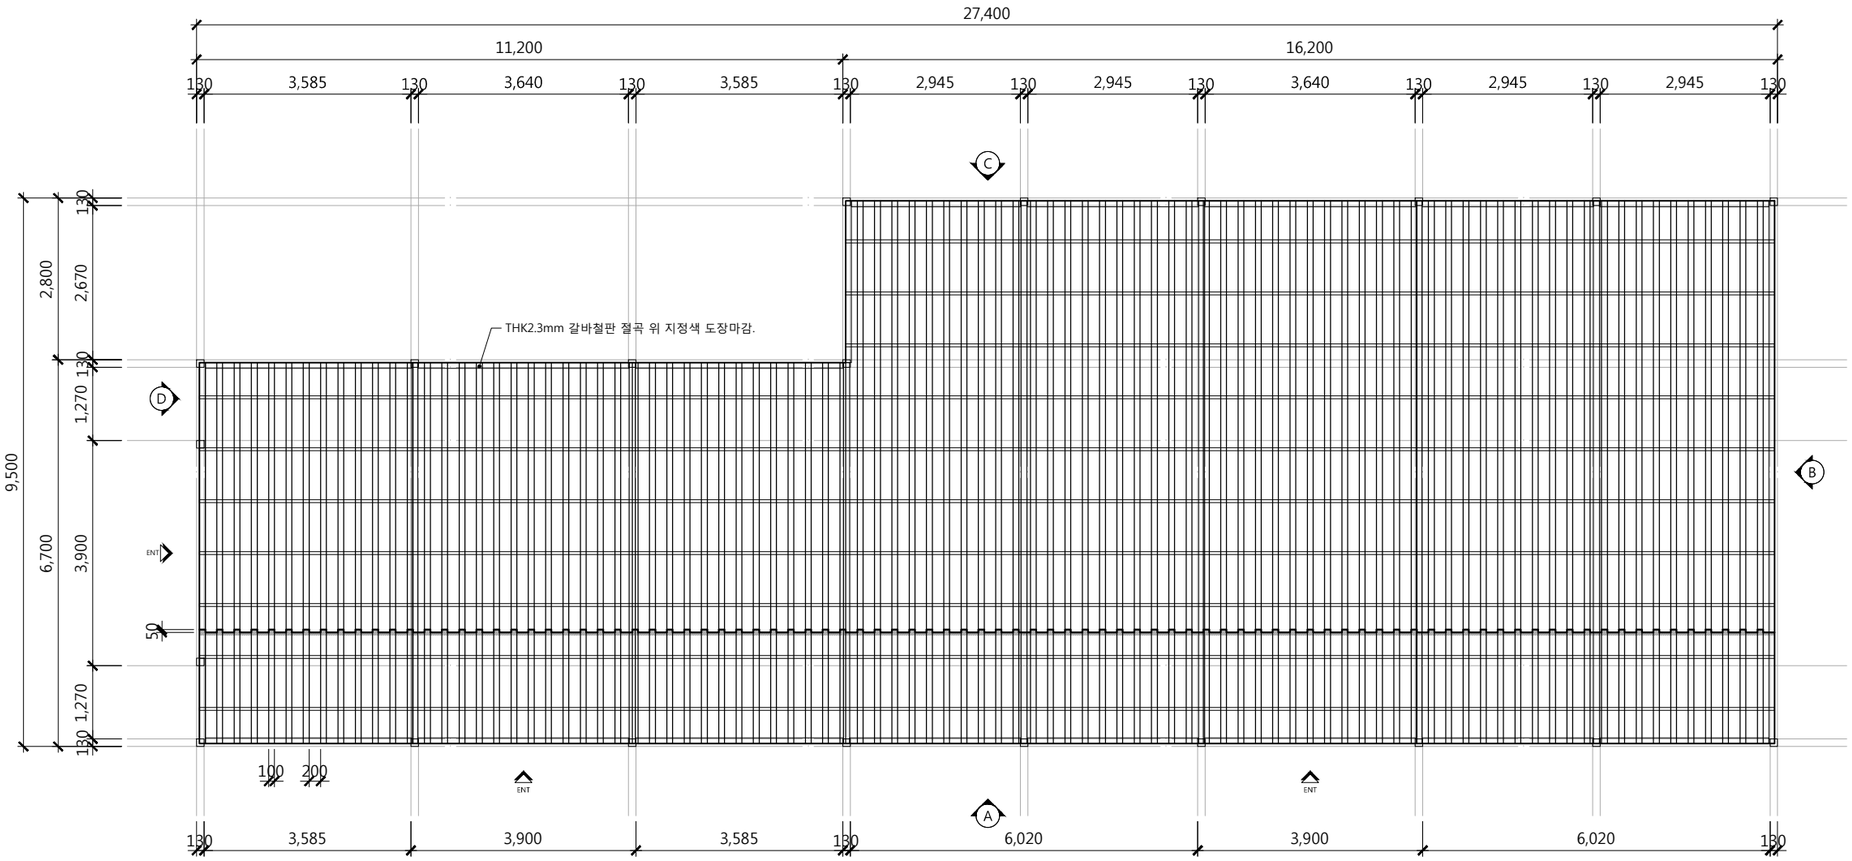

1 지붕 평면도

SCALE 1 / 100

NOTE / REVISION

ROOF C.H. : 3,650 / 2,900

NAME OF PROJECT

부산역 3층맞이방 전문점 신축공사

ARCHITECTURE

STRUCTURE

MECHANIC

ELECTRIC

APPROVED BY

DESIGNED BY

DRAWING BY

CHECKED BY

DATE 2017. 01

SCALE A3 - 1 / 100


DRAWING TITLE 지붕 평면도

PROJECT NO.

SHEET NO. 000


SHEET NO. I-009

서울시 영등포구 당산3가 2-7
TEL / 02) 2630-8945
FAX / 02) 2630-8926

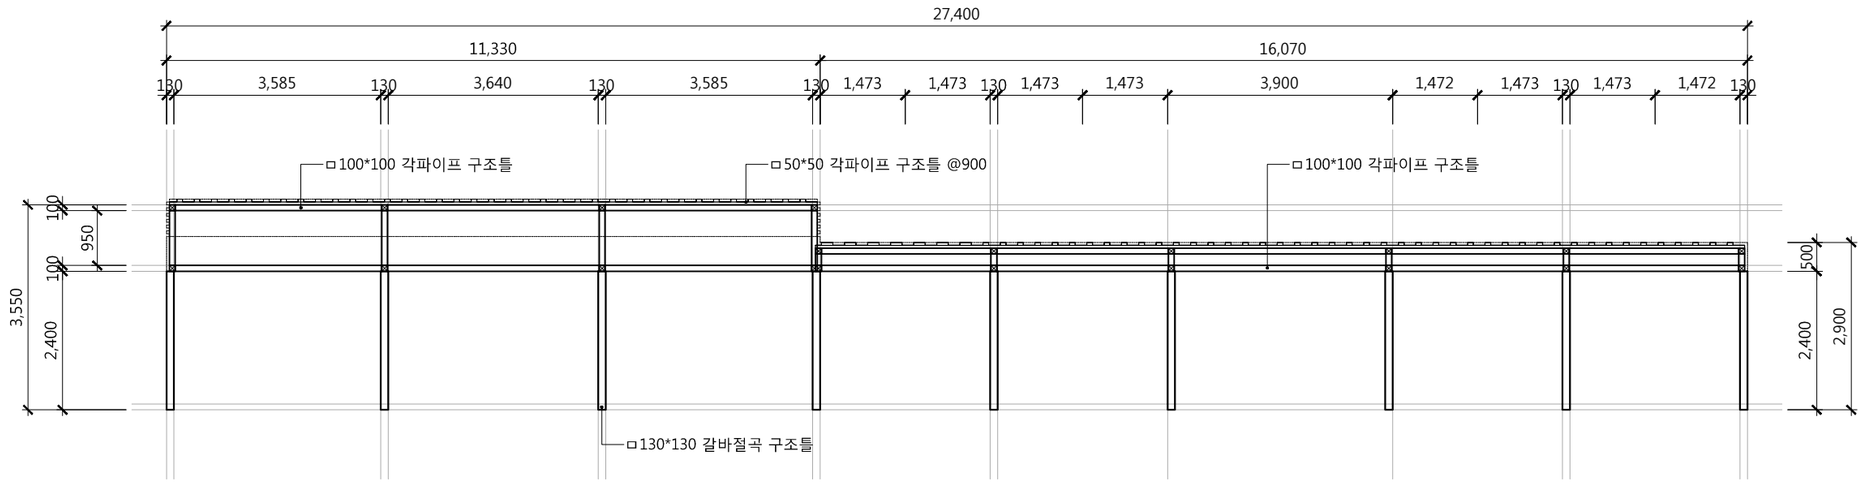

1 골조 입면도 -A

SCALE 1 / 100

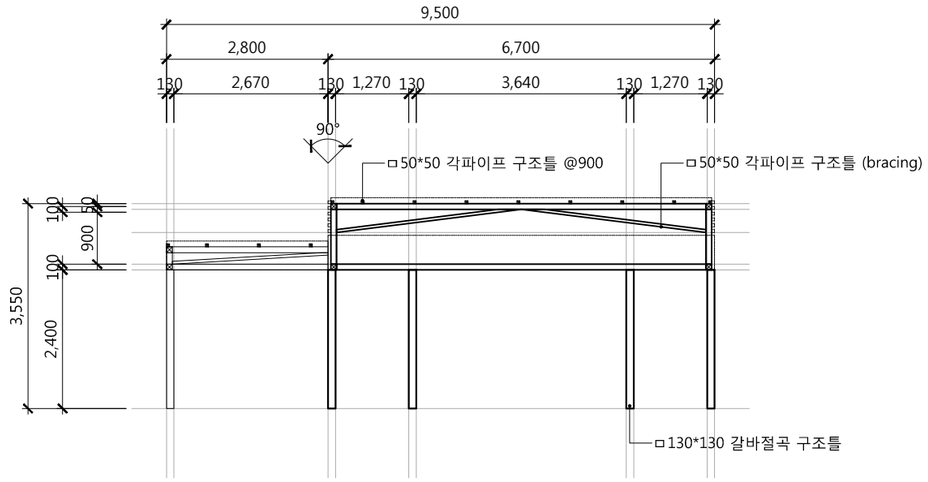

2 골조 입면도 -D

SCALE 1 / 100

StoryWay

NOTE / REVISION

ROOF C.H. : 3,650 / 2,900

NAME OF PROJECT

부산역 3층맞이방 전문점 신축공사

ARCHITECTURE

STRUCTURE

MECHANIC

ELECTRIC

APPROVED BY

DESIGNED BY

DRAWING BY

CHECKED BY

DATE 2017. 01

SCALE A3 - 1 / 100

DRAWING TITLE

골조 입면도 -A,D


PROJECT NO.

SHEET NO. 000

SHEET NO. I-010


KORAIL RETAIL

서울시 영등포구 당산3가 2-7
TEL / 02) 2630-8945
FAX / 02) 2630-8926

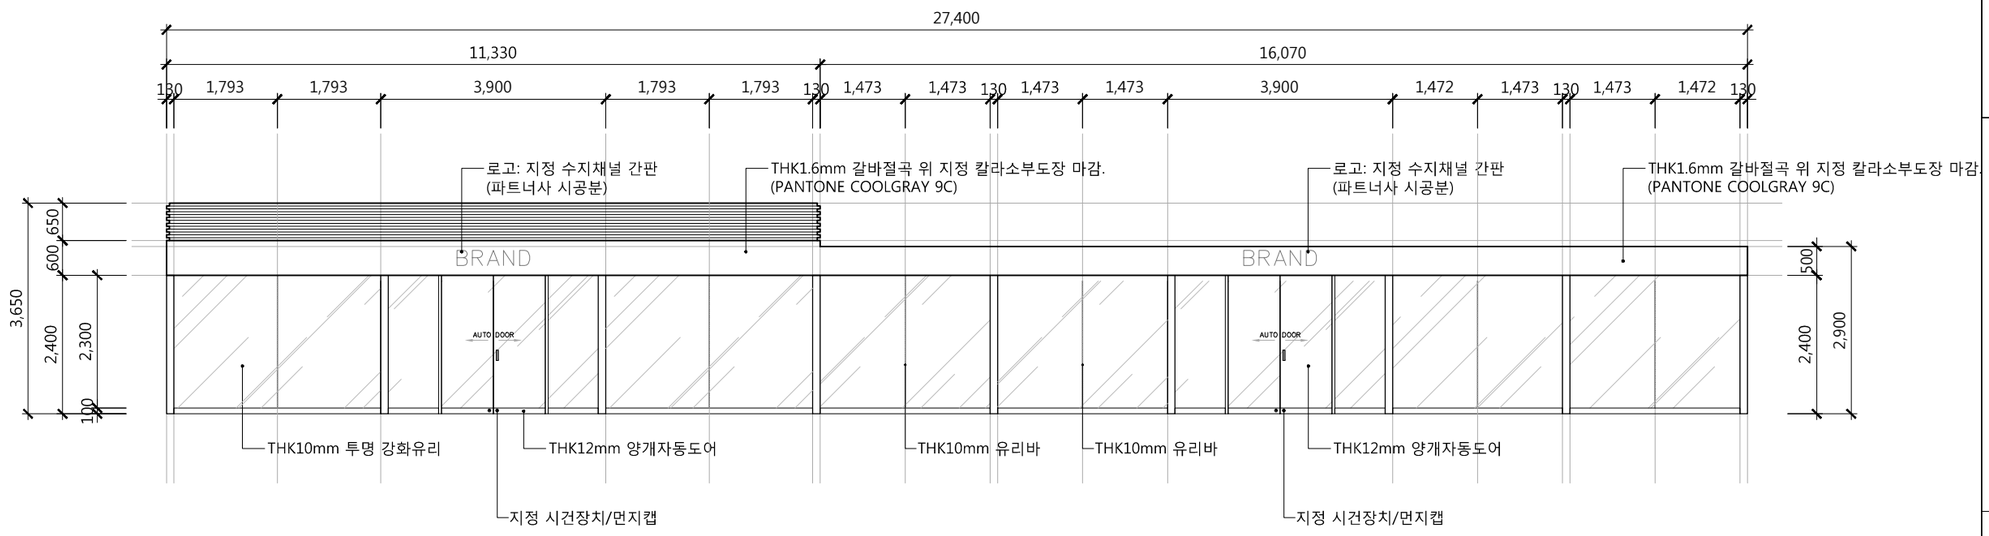

1 입면도 -A

SCALE 1 / 100

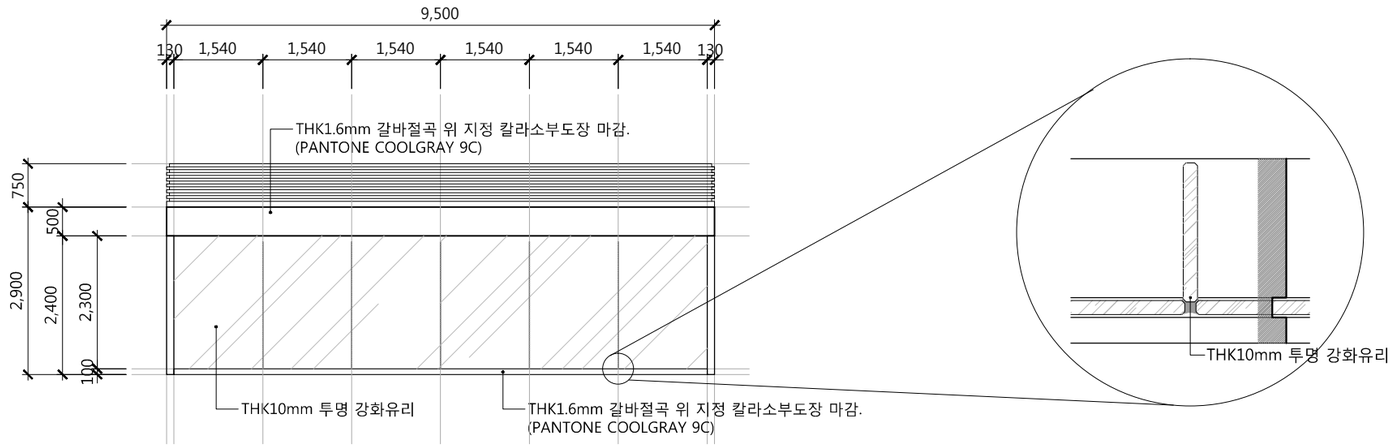

2 입면도 -B

SCALE 1 / 100

StoryWay

NOTE / REVISION

ROOF C.H. : 3,650 / 2,900

NAME OF PROJECT

부산역 3층맞이방 전문점
신축공사

ARCHITECTURE

STRUCTURE

MECHANIC

ELECTRIC

APPROVED BY

DESIGNED BY

DRAWING BY

CHECKED BY

DATE 2017. 01

SCALE A3 - 1 / 100

DRAWING TITLE

입면도 -A,B


PROJECT NO.

SHEET NO. 000

SHEET NO. I-011


KORAIL RETAIL

서울시 영등포구 당산3가 2-7
TEL / 02) 2630-8945
FAX / 02) 2630-8926

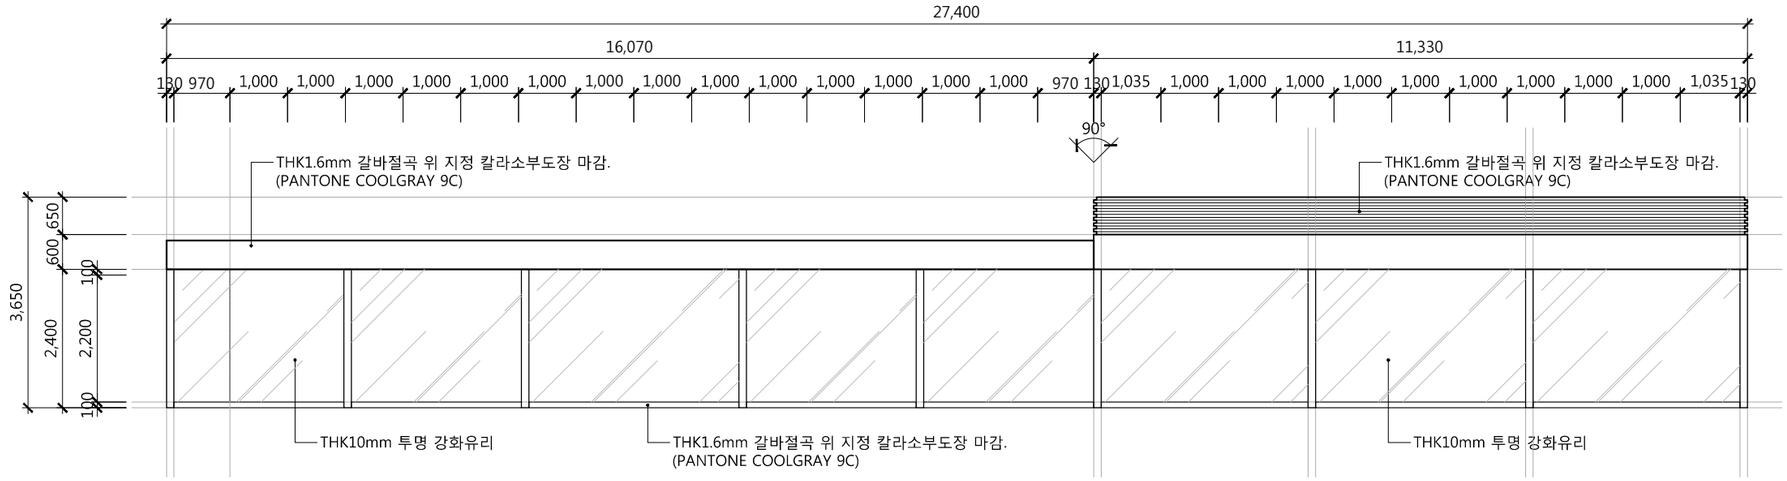

1 입면도 -C

SCALE 1 / 100

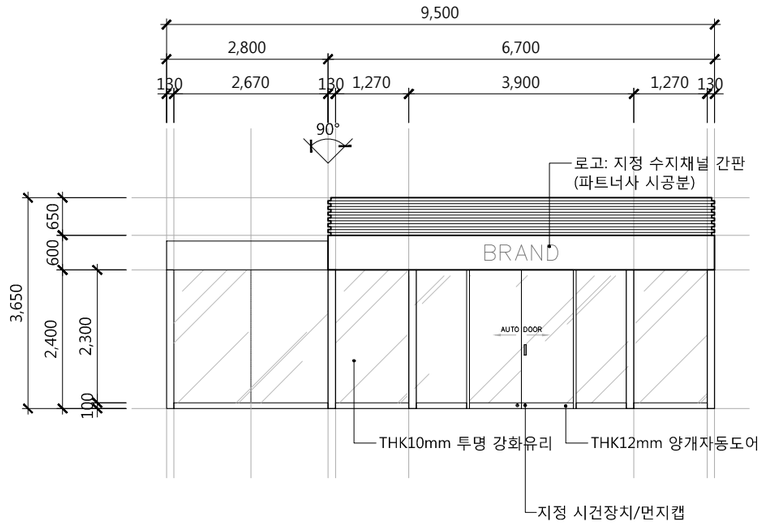

2 입면도 -D

SCALE 1 / 100

StoryWay

NOTE / REVISION

ROOF C.H. : 3,650 / 2,900

NAME OF PROJECT

부산역 3층맞이방 전문점
신축공사

ARCHITECTURE

STRUCTURE

MECHANIC

ELECTRIC

APPROVED BY

DESIGNED BY

DRAWING BY

CHECKED BY

DATE 2017. 01

SCALE A3 - 1 / 100

DRAWING TITLE

입면도 -C,D


PROJECT NO.

SHEET NO. 000

SHEET NO. I-012


KORAIL RETAIL

서울시 영등포구 당산3가 2-7
TEL / 02) 2630-8945
FAX / 02) 2630-8926

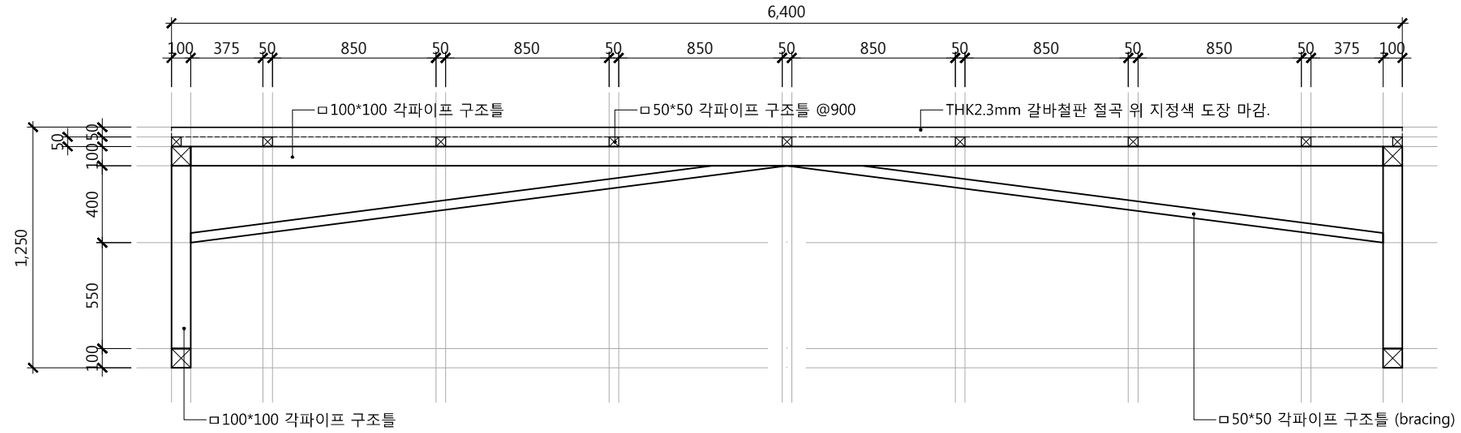


1 천정 구조 트러스 상세도 -1

SCALE 1 / 30

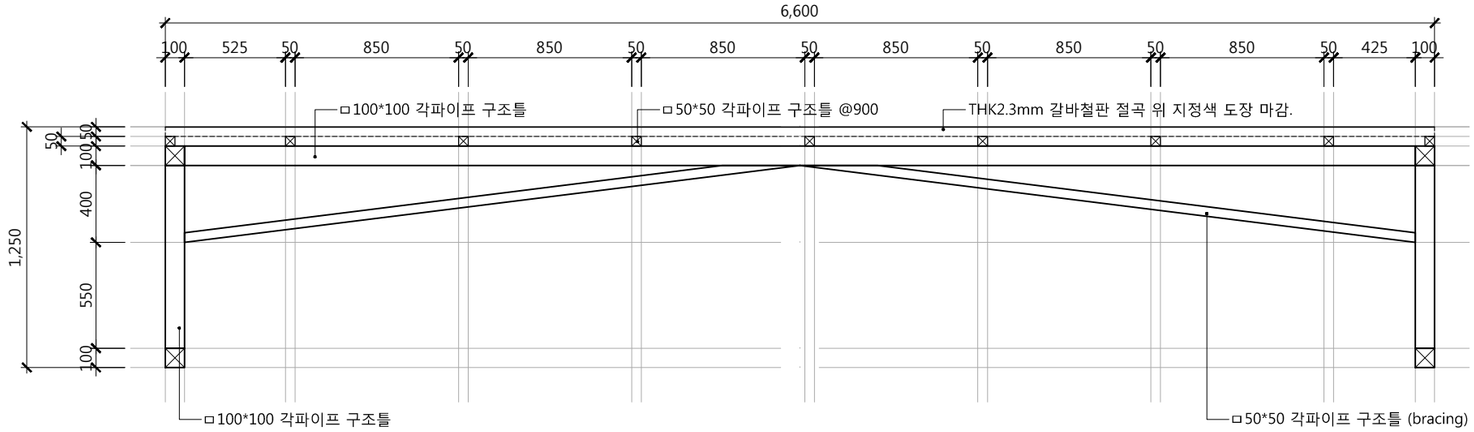

2 천정 구조 트러스 상세도 -2

SCALE 1 / 30

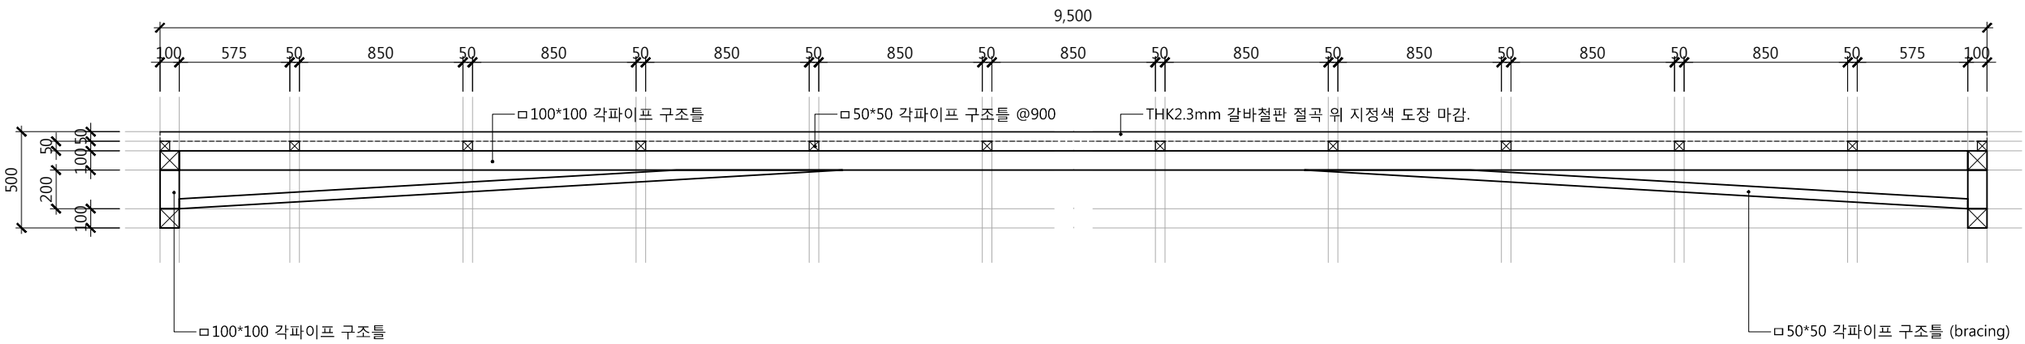

3 천정 구조 트러스 상세도 -3

SCALE 1 / 30

StoryWay

NOTE / REVISION

ROOF C.H. : 3,650 / 2,900

NAME OF PROJECT

부산역 3층맞이방 전문점 신축공사

ARCHITECTURE

STRUCTURE

MECHANIC

ELECTRIC

APPROVED BY

DESIGNED BY

DRAWING BY

CHECKED BY

DATE 2017. 01

SCALE A3 - 1 / 30

DRAWING TITLE

천정 구조 트러스 상세도


PROJECT NO.

SHEET NO. 000

SHEET NO. D-01

KORAIL RETAIL

서울시 영등포구 당산3가 2-7
TEL / 02) 2630-8945
FAX / 02) 2630-8926

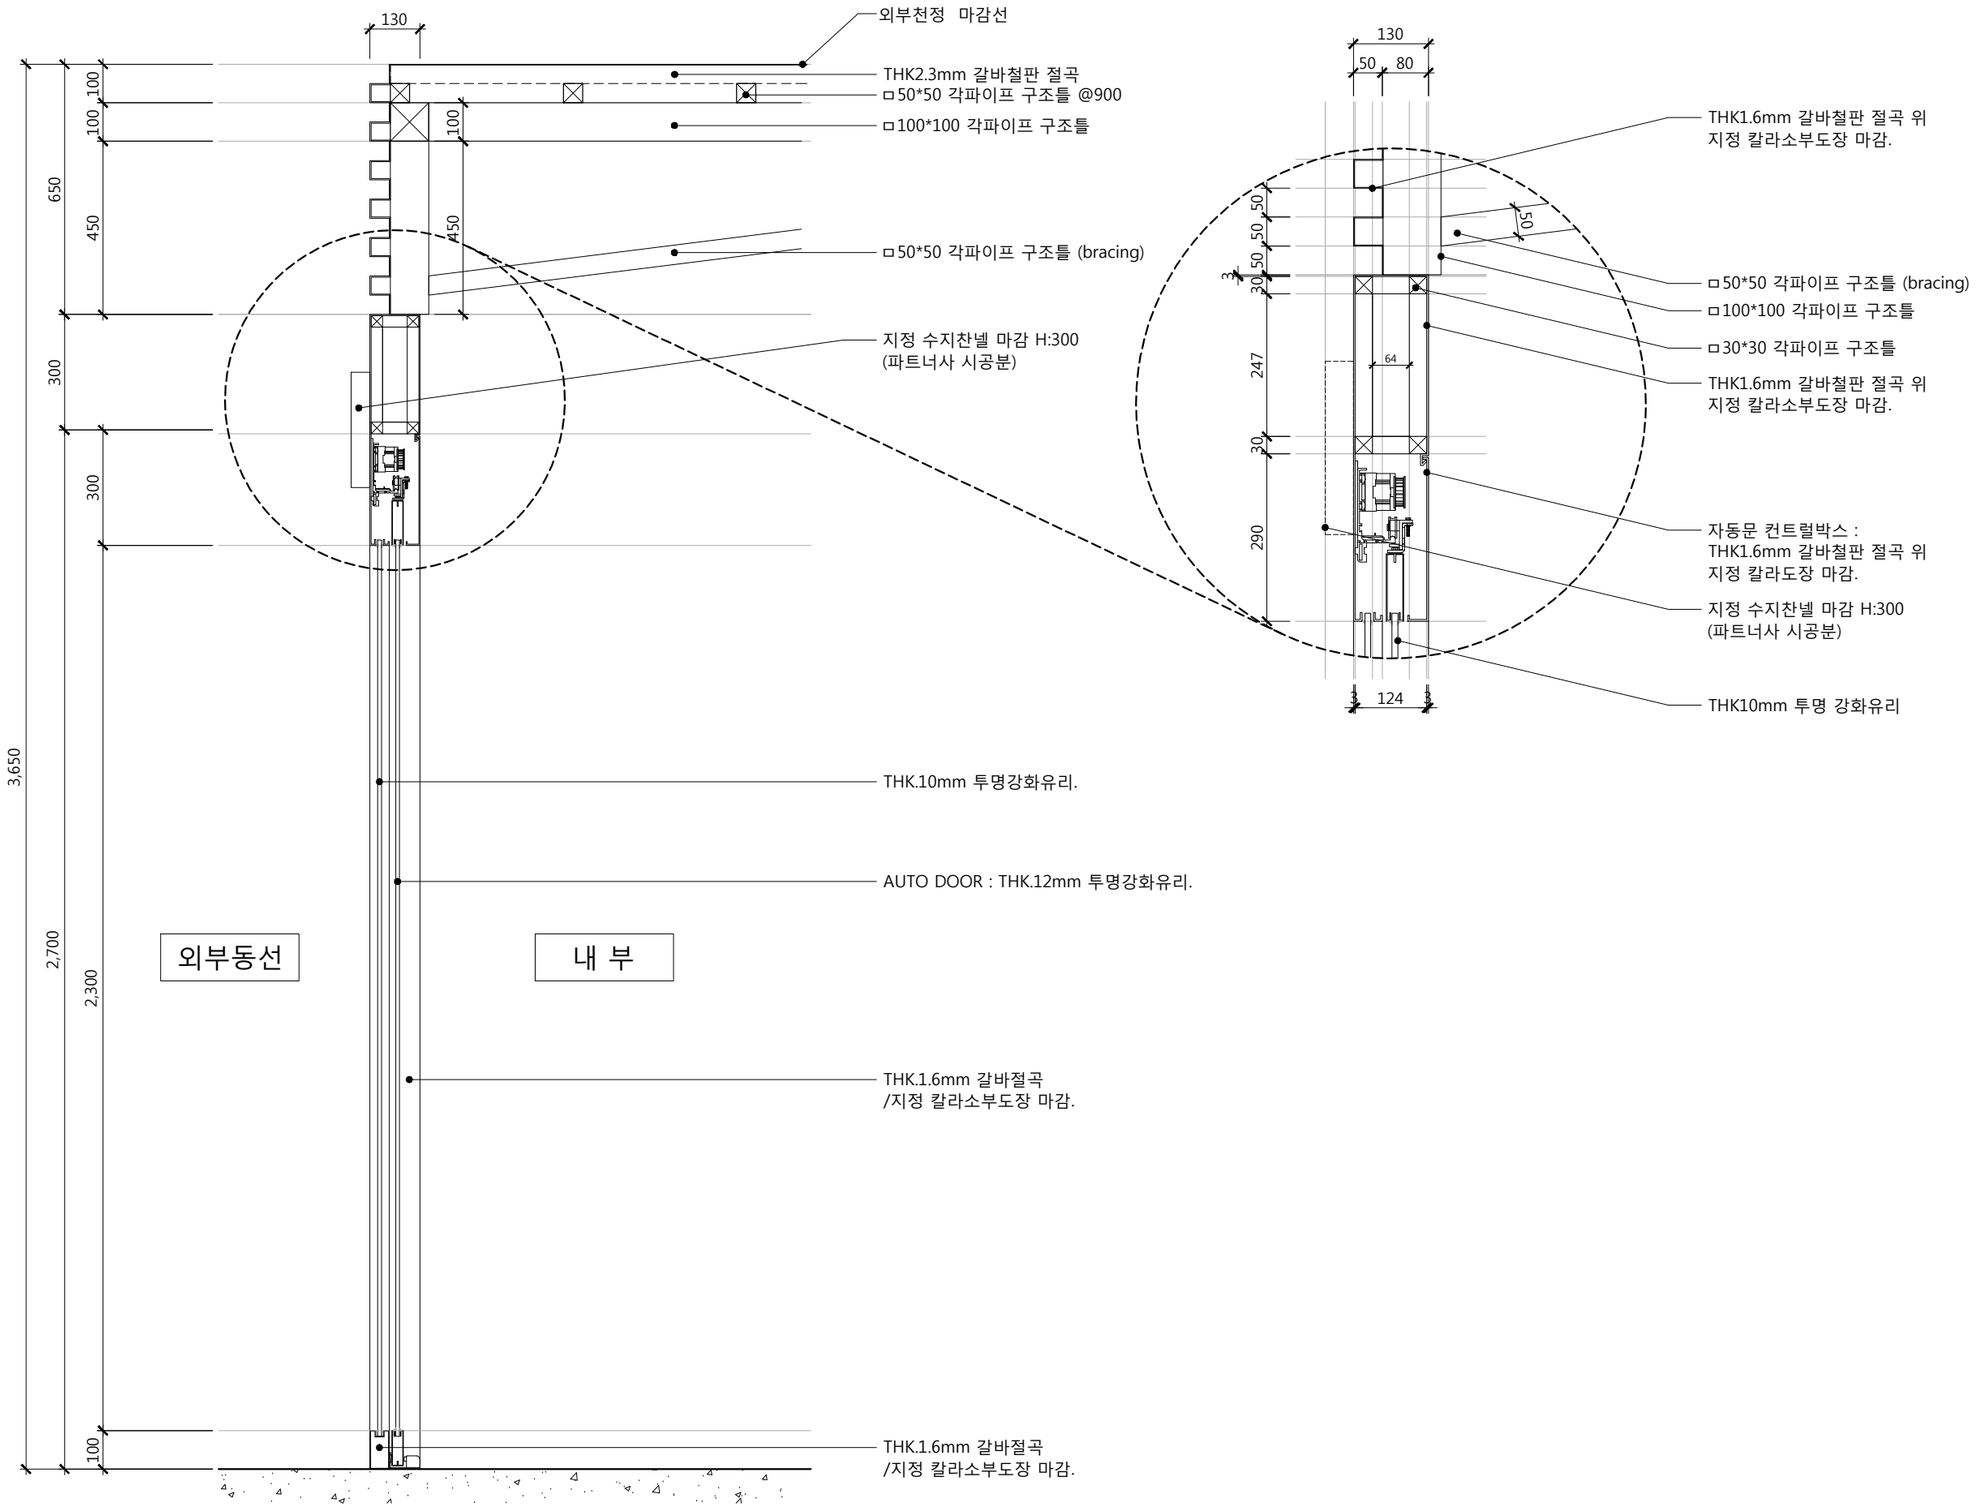

1 출입구 단면상세도

SCALE 1 / 15

StoryWay

NOTE / REVISION

ROOF C.H. : 3,650 / 2,900

NAME OF PROJECT

부산역 3층 상업시설
인테리어 공사

ARCHITECTURE

STRUCTURE

MECHANIC

ELECTRIC

APPROVED BY

DESIGNED BY

DRAWING BY

CHECKED BY

DATE 2017. 01

SCALE A3 - 1 / 15

DRAWING TITLE

출입구 단면 상세도


PROJECT NO.

SHEET NO. 000

SHEET NO. D-02

KORAIL RETAIL

서울시 영등포구 당산3가 2-7
TEL / 02) 2630-8945
FAX / 02) 2630-8926

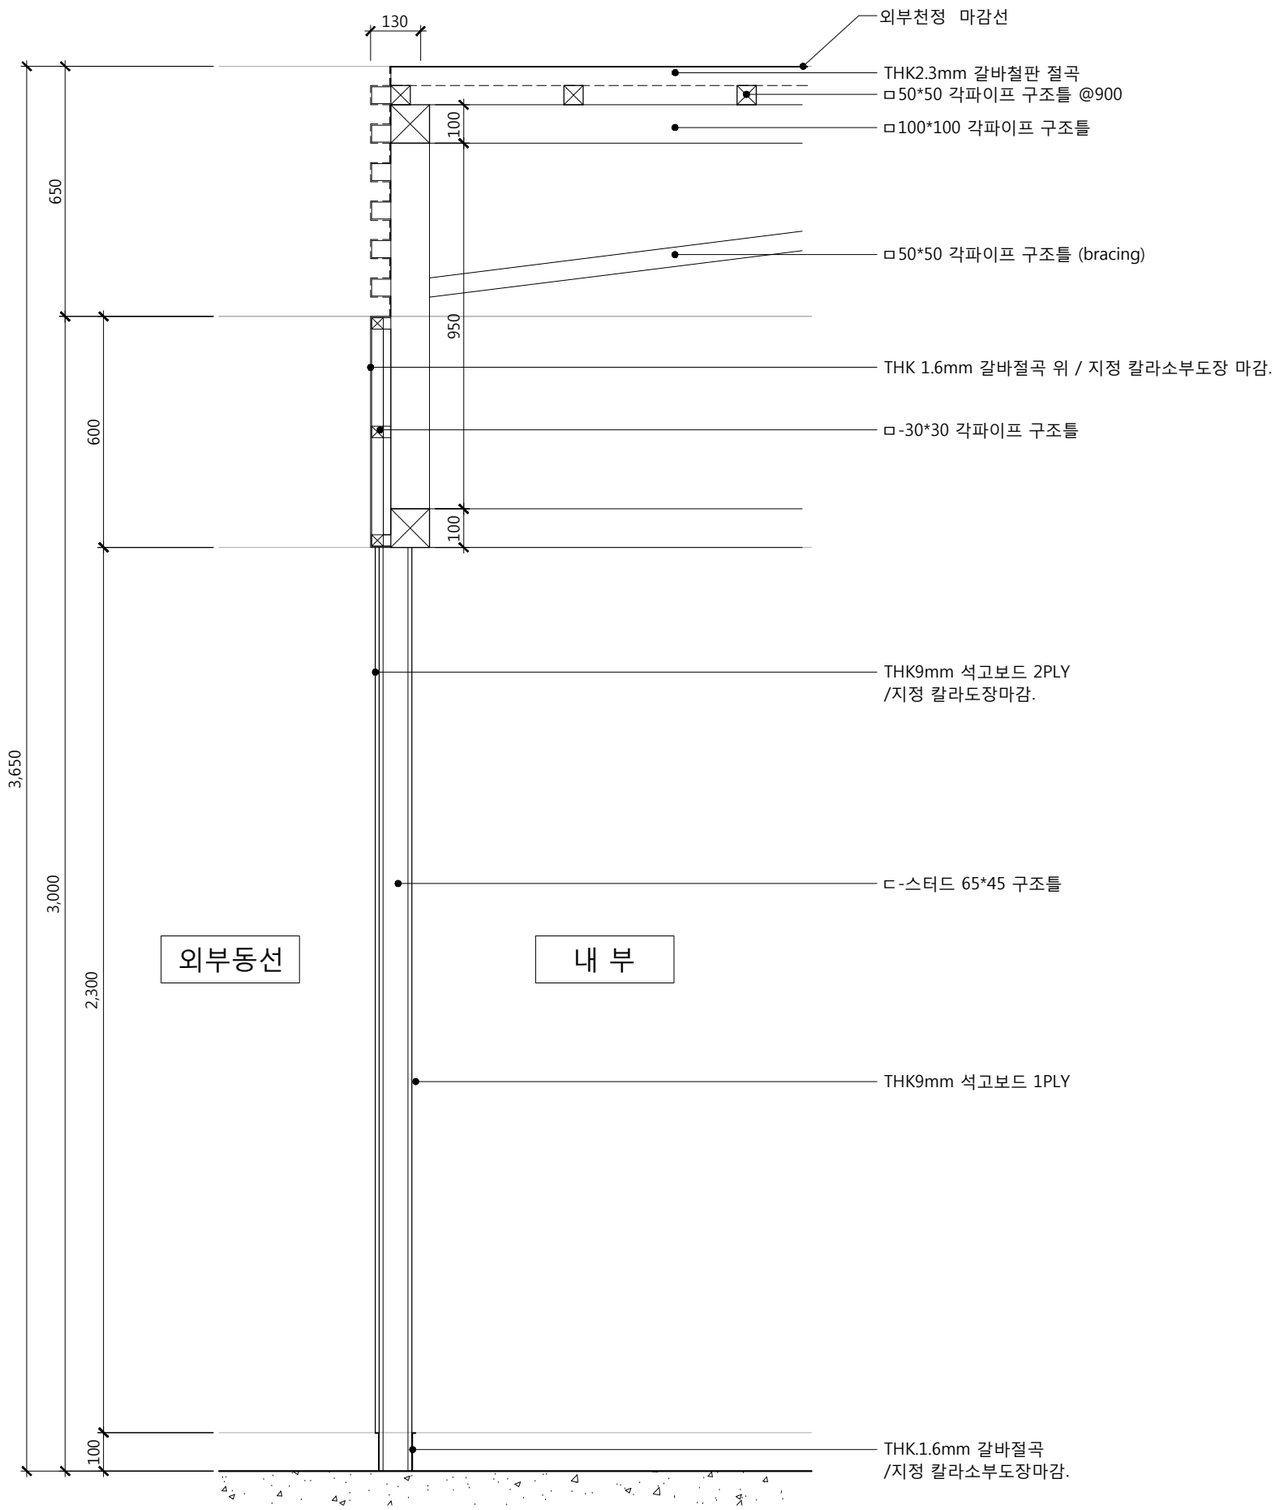

1 벽체 단면상세도

SCALE 1 / 15

StoryWay

NOTE / REVISION

ROOF C.H. : 3,650 / 2,900

NAME OF PROJECT

부산역 3층맞이방 전문점 신축공사

ARCHITECTURE

STRUCTURE

MECHANIC

ELECTRIC

APPROVED BY

DESIGNED BY

DRAWING BY

CHECKED BY

DATE 2017. 01

SCALE A3 - 1 / 15

DRAWING TITLE

벽체 단면상세도

PROJECT NO.

SHEET NO. 000

SHEET NO. D-03

KORAIL RETAIL

서울시 영등포구 당산3가 2-7
TEL / 02) 2630-8945
FAX / 02) 2630-8926