
1층 ↔ 승인된 2층 · 대응점 정합 오버레이

공통 기둥 57곳 · 공통 구조 모서리 9곳 · 1층 회전/기울기/구간별 비율 보정


회색: 승인된 2층 고정　파랑: 대응점으로 정합한 1층　하단 별도 위치도 제외

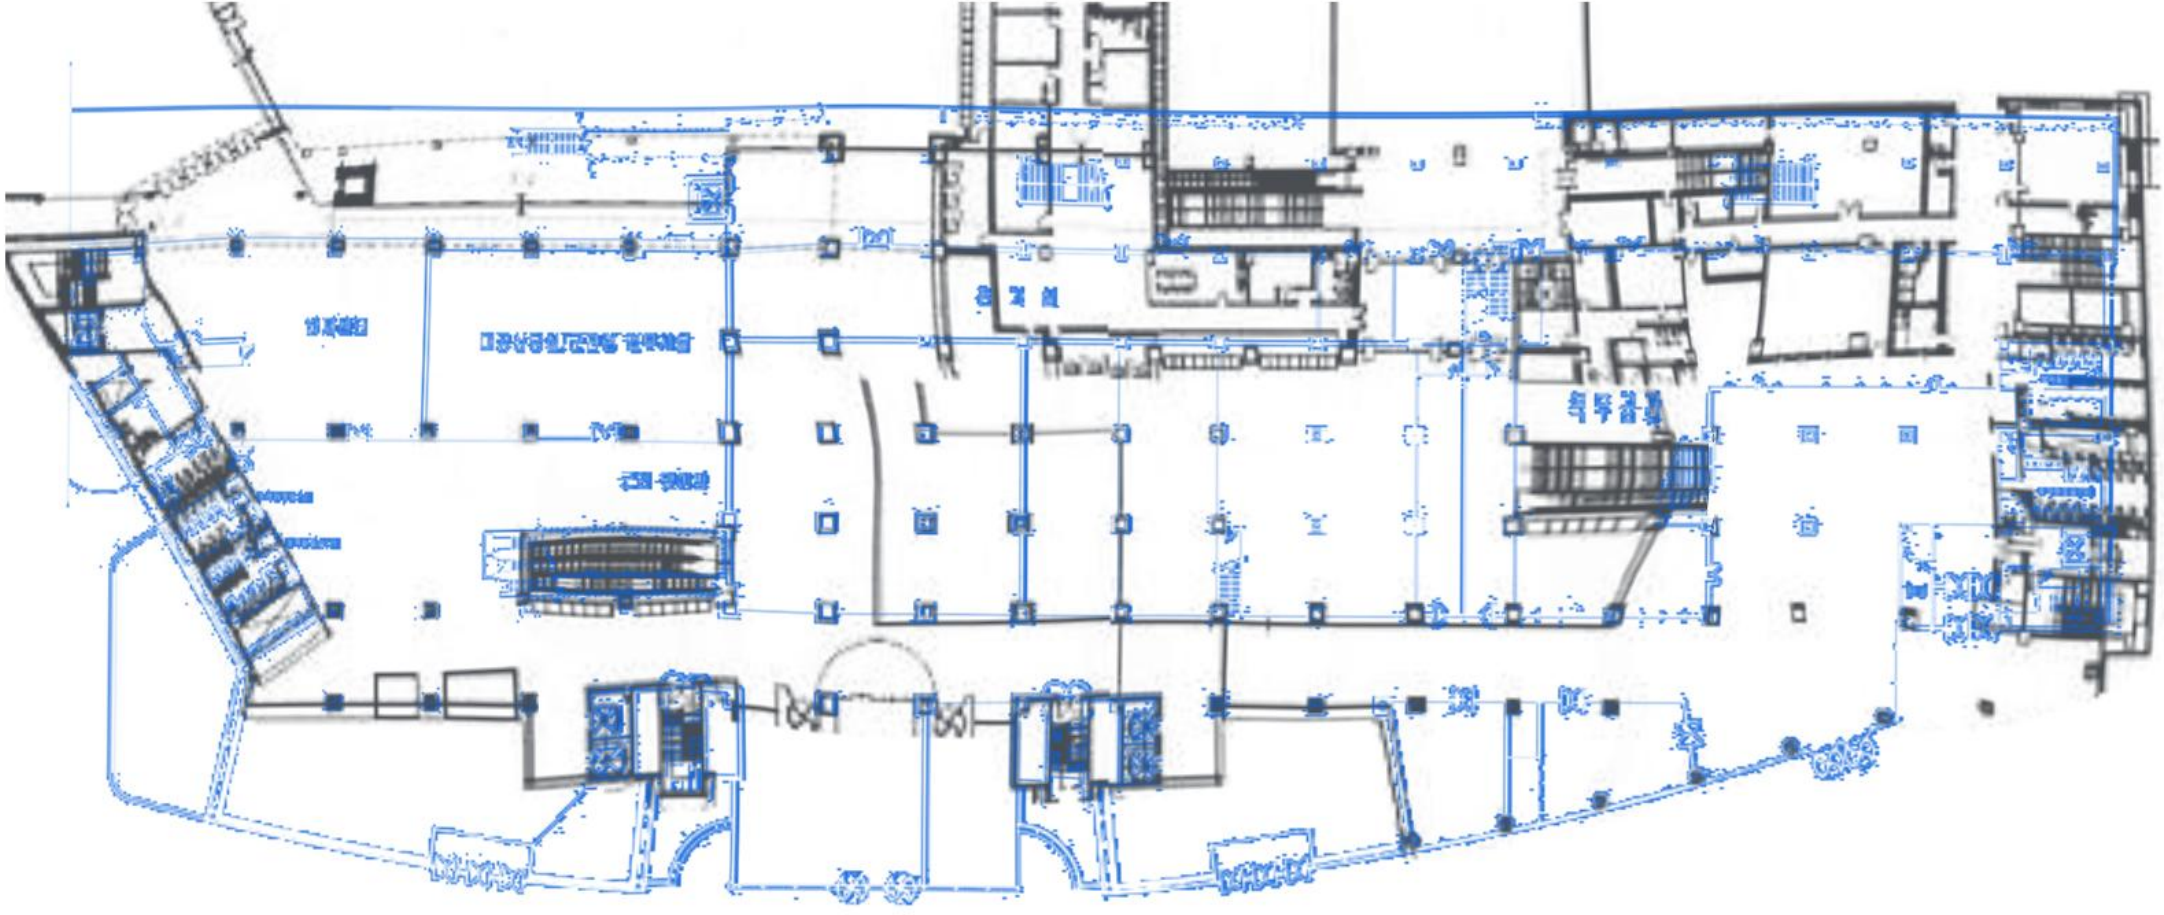

서측 승강기·계단 코어 · 대응 정합 상세

동일 구조 대응점을 고정한 1층 도면 변형; 서로 다른 층의 칸막이는 각각 표시

회색: 승인된 2층 고정　파랑: 대응점으로 정합한 1층　하단 별도 위치도 제외

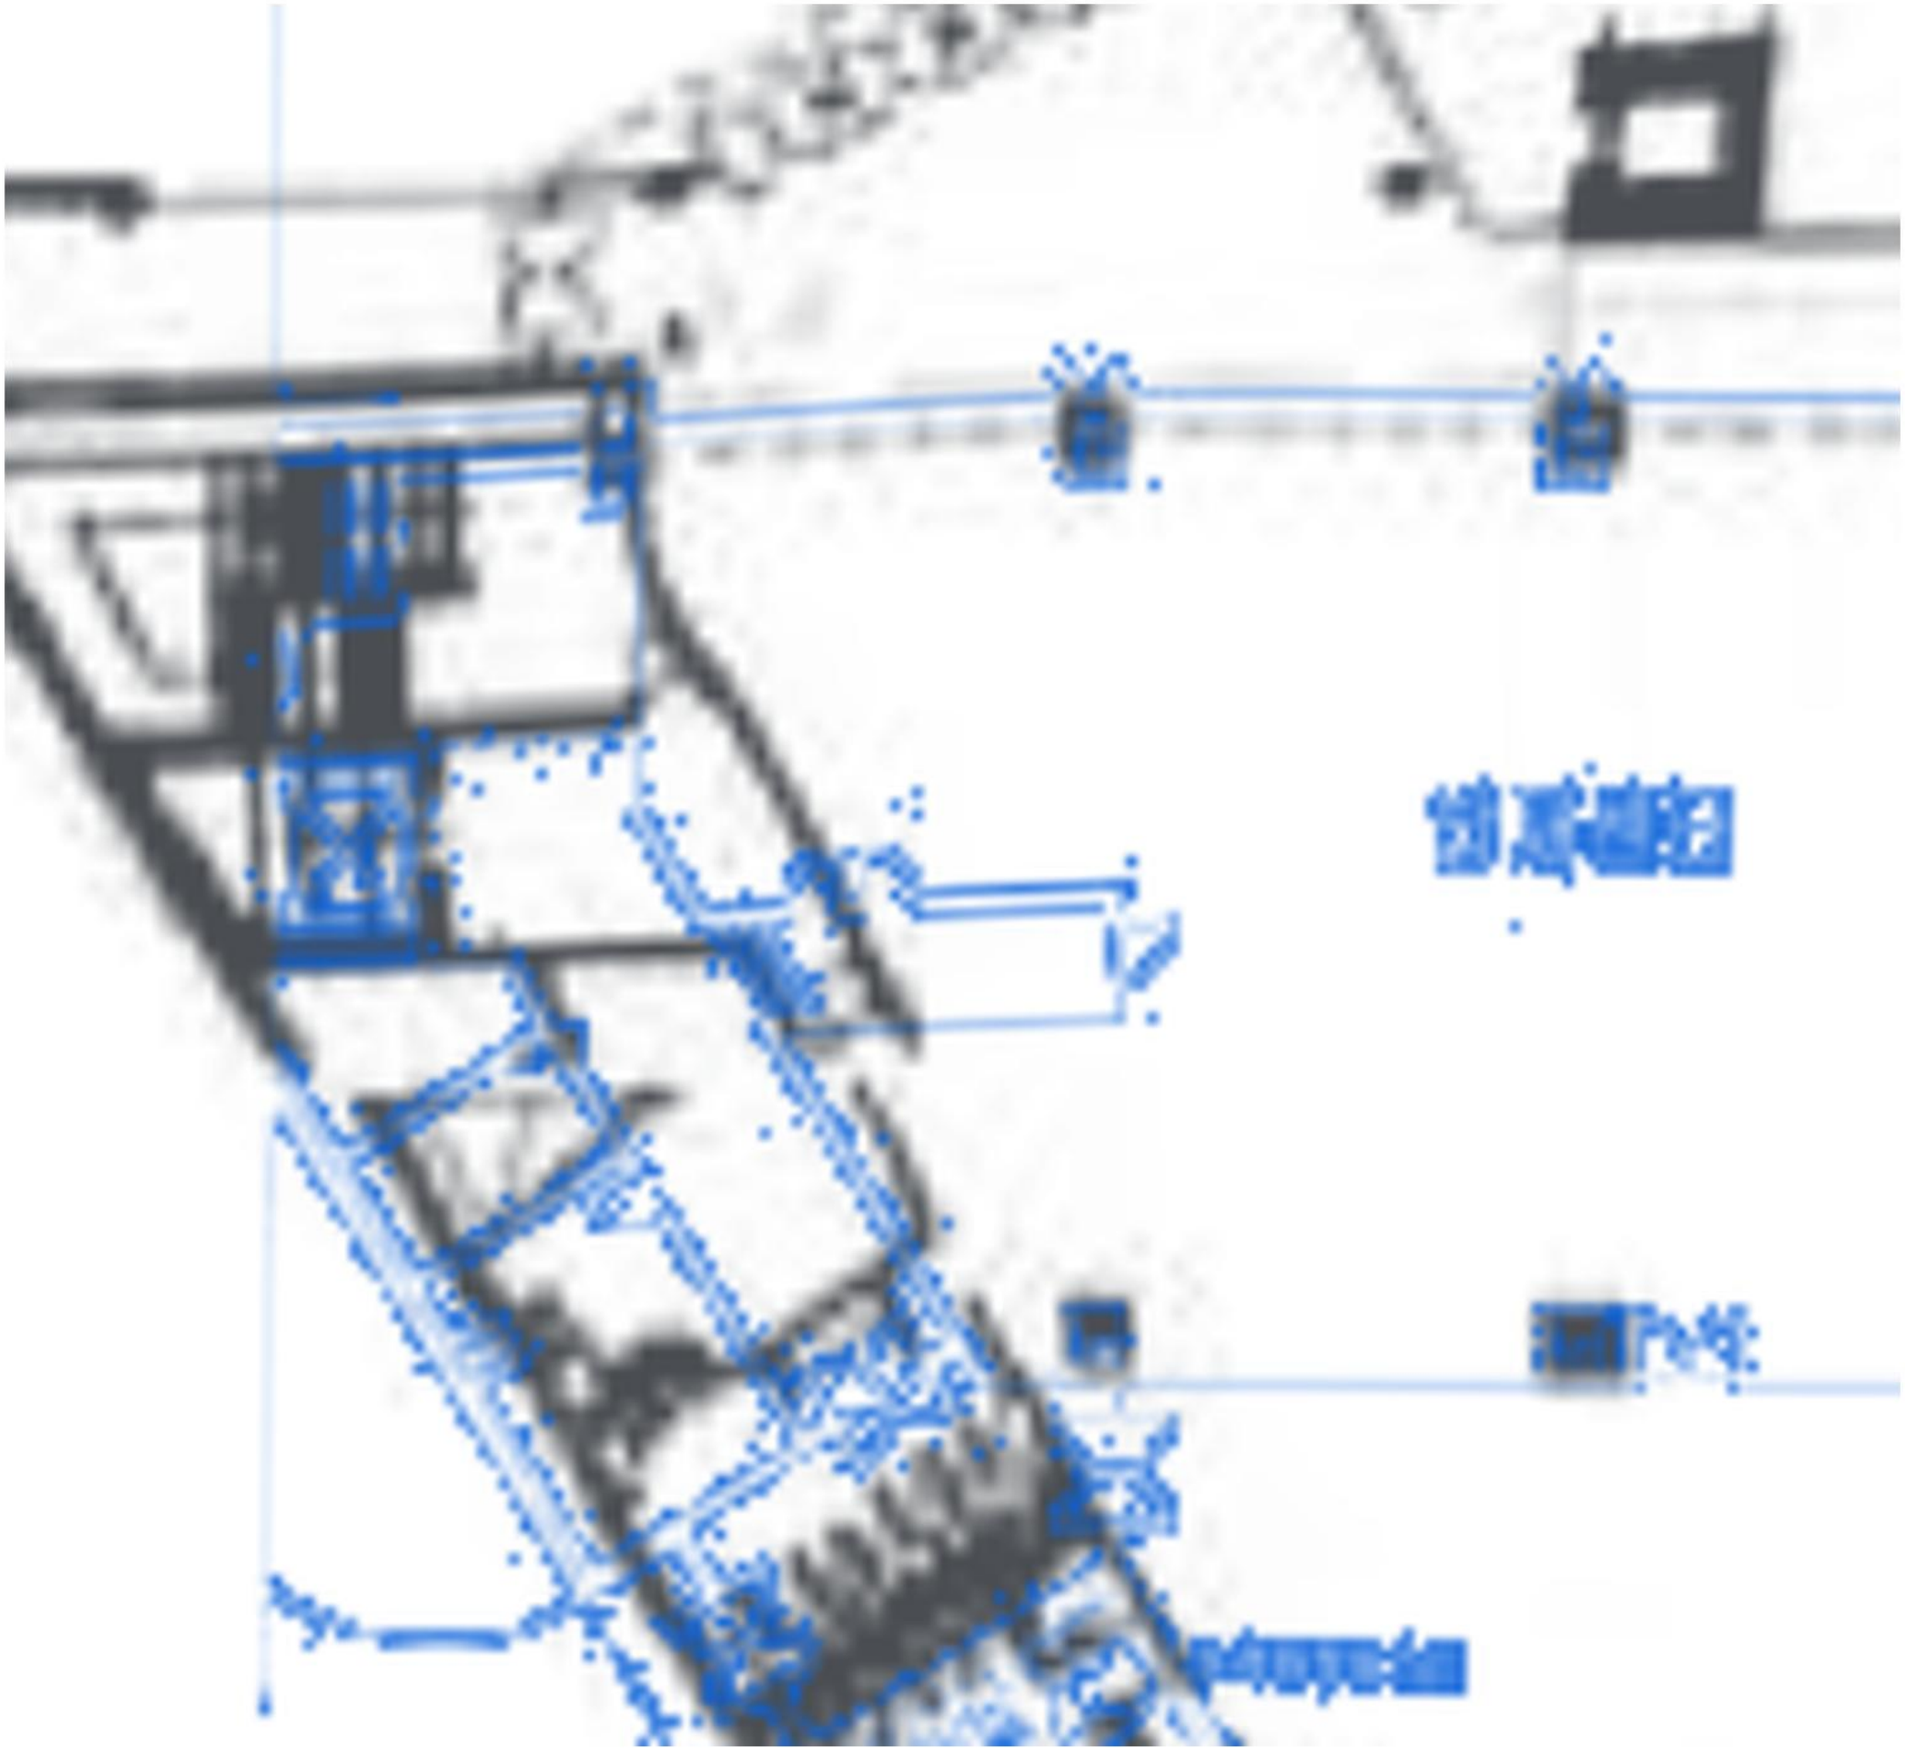

2층 전체 도면과 정합한 1층 도면

승인된 2층 전체는 고정하고 공통 구조 구간에 1층을 대응시켰습니다.

회색: 승인된 2층 고정　파랑: 대응점으로 정합한 1층　하단 별도 위치도 제외

