
KORAIL RETAIL

부산역 1층 맛이방 전문점 신축공사

2018 . 12.

코레일유통(주)

GRECO DESIGNGROUP

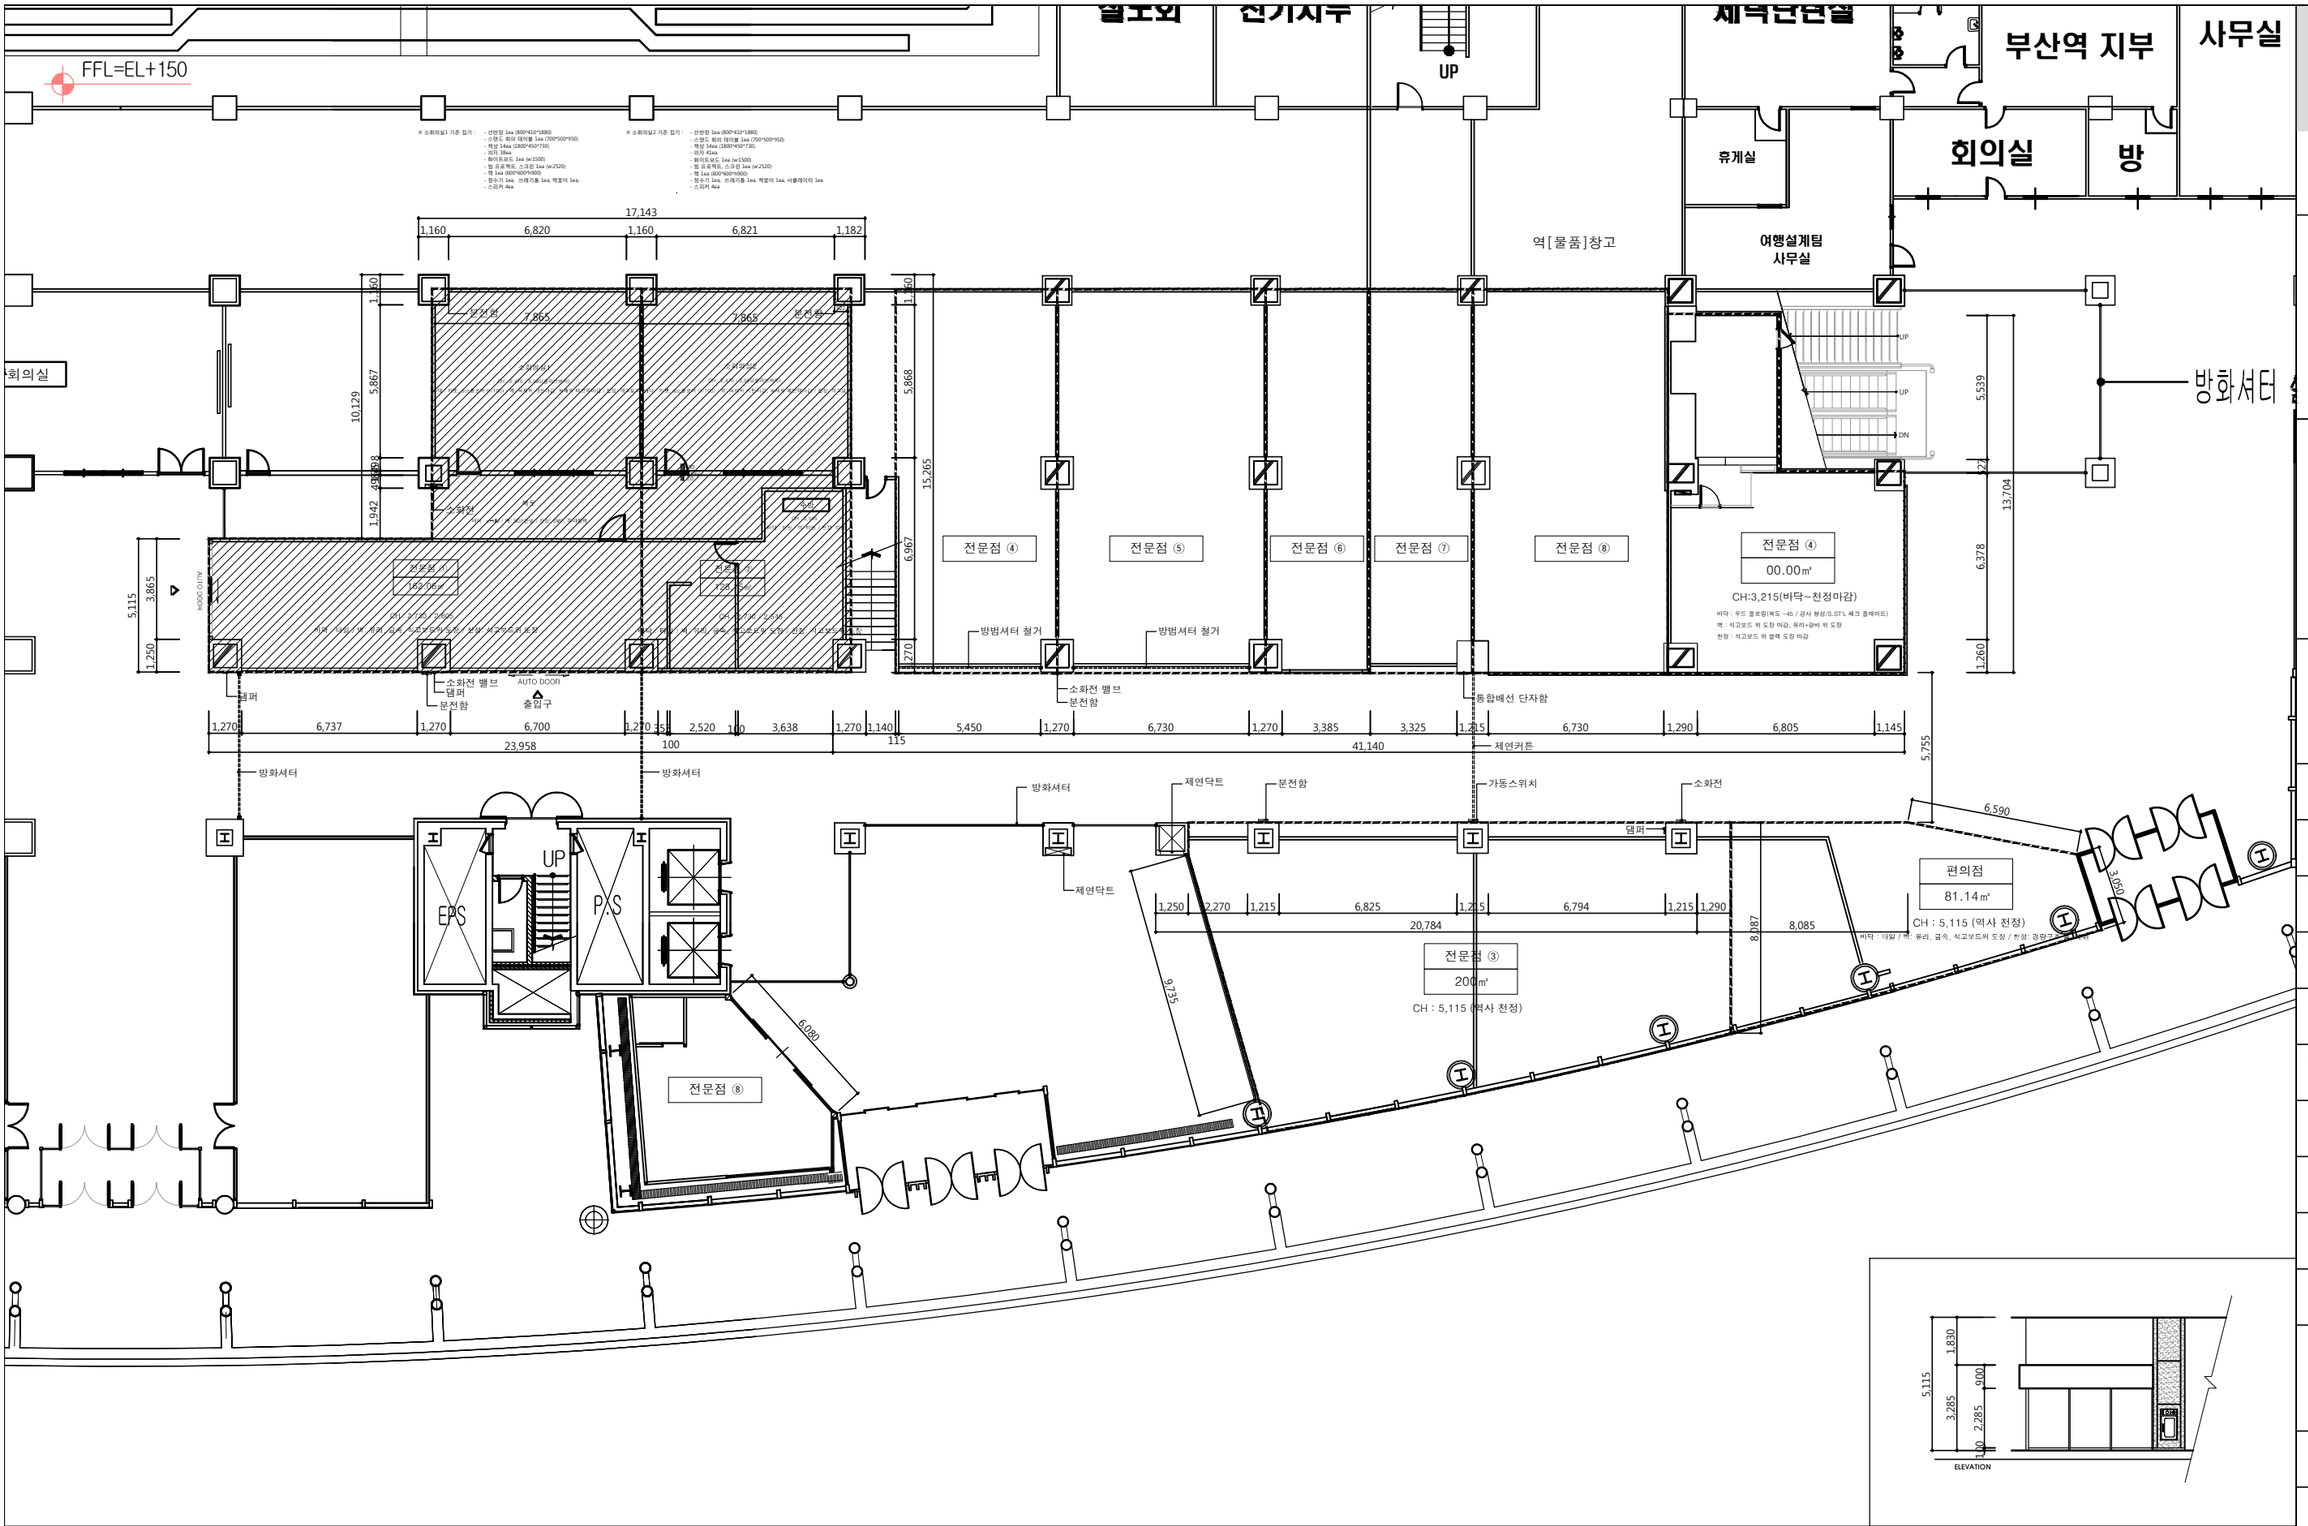

※ 특이사항 (NOTES)

ELEVATION

1 BASE FLOOR PLAN (전체 배치도_1F)

SCALE 1/250

KORAIL RETAIL
서울시 영등포구 당산3가 2-7
TEL / 02) 2630-8945
FAX / 02) 2630-8926

StoryWay

NOTE / REVISION

NAME OF PROJECT
부산역 Project_1F
전문점①,②

ARCHITECTURE

STRUCTURE

MECHANIC

ELECTRIC

APPROVED BY

DESIGNED BY

DRAWING BY
Park, H. R.

CHECKED BY
Kim, S.C.

DATE
2018. 11.


SCALE
1 / 250

DRAWING TITLE
BASE FLOOR PLAN
(전체 배치도_1F)

PROJECT NO.

SHEET NO.	DRAWING NO.
101	I-101

Greco DESIGNGROUP
Sukjung Bldg. 2F
203-3 Donggyo-dong,
Mapo-gu, Seoul, Korea. 03992
www.grecodesign.co.kr
T.+82-2-336-2082 F.+82-2-336-2297

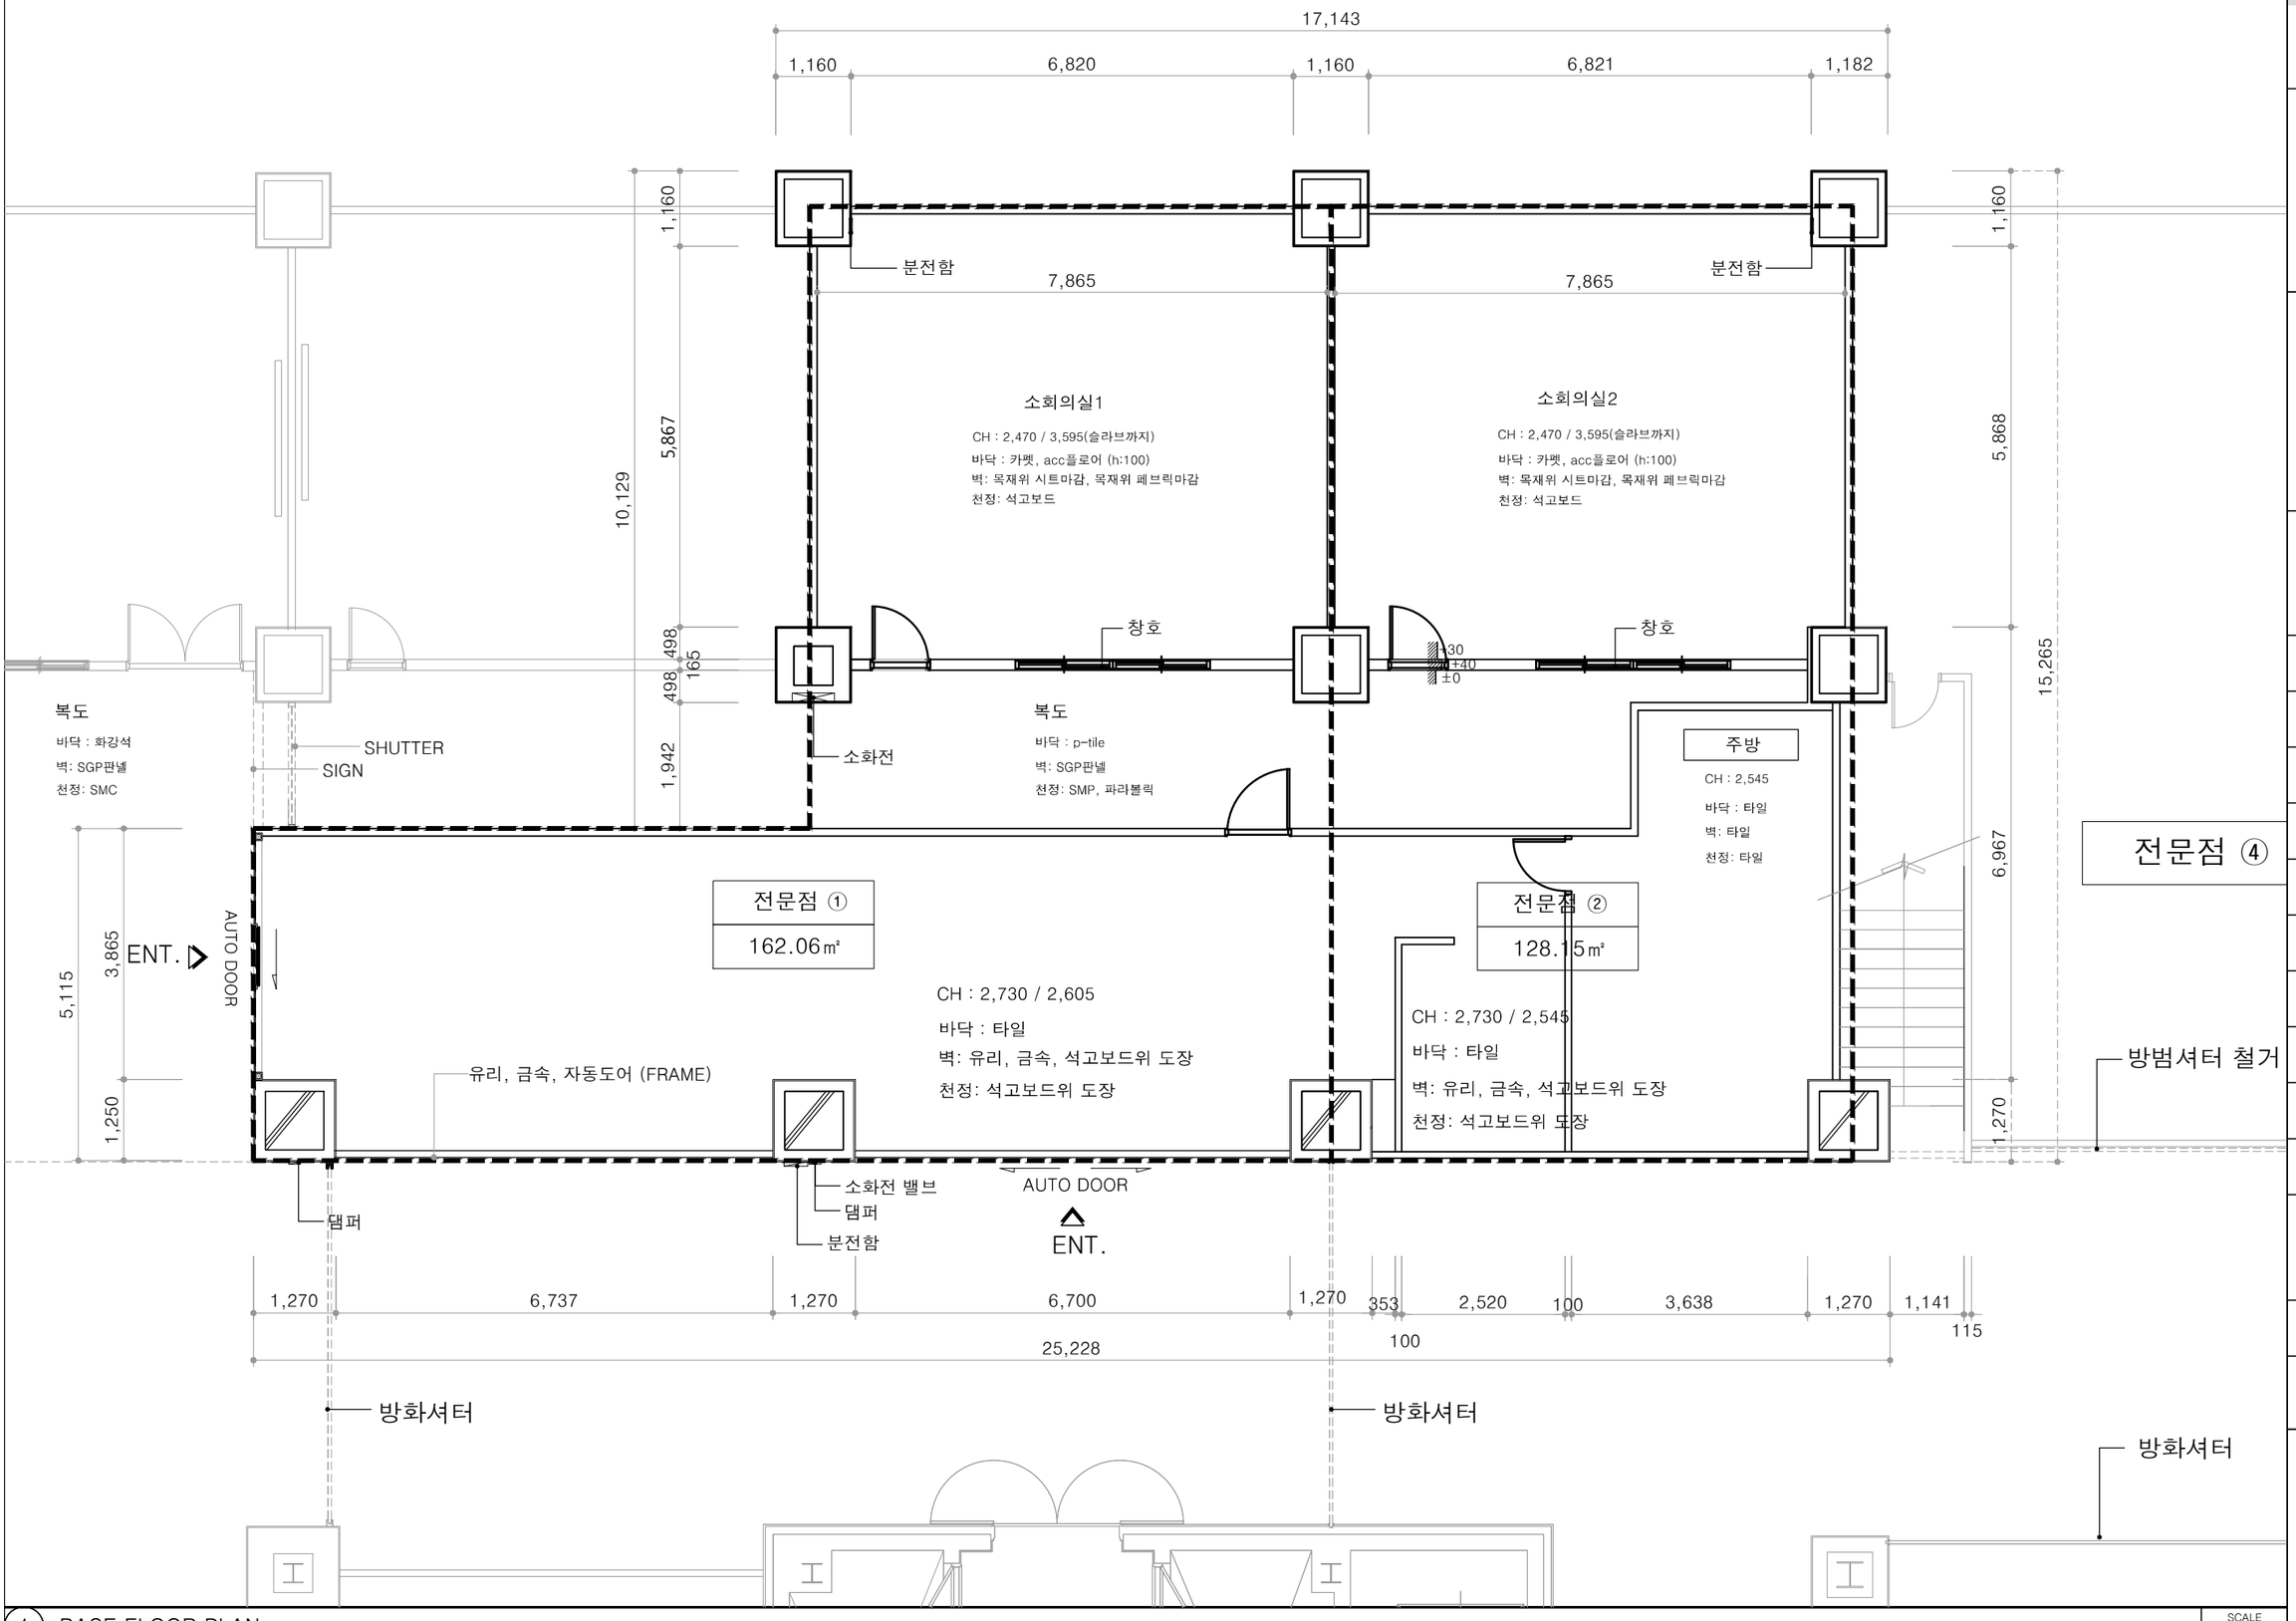

1 BASE FLOOR PLAN

SCALE 1/100

KORAIL RETAIL
서울시 영등포구 당산3가 2-7
TEL / 02) 2630-8945
FAX / 02) 2630-8926

StoryWay

NOTE / REVISION

전문점 1: 162.06㎡
전문점 2: 128.15㎡
역사 건물 CH:5,115
매장 마감 CH:3,200 (마감제외)

NAME OF PROJECT

부산역 Project_1F
전문점①,②

ARCHITECTURE

STRUCTURE

MECHANIC

ELECTRIC

APPROVED BY

DESIGNED BY

DRAWING BY
Park, H. R.

CHECKED BY
Kim, S.C.

DATE
2018. 11.


SCALE
1 / 100

DRAWING TITLE
BASE FLOOR PLAN

PROJECT NO.

SHEET NO.	DRAWING NO.
102	I-102

Greco DESIGNGROUP
Sukjung Bldg. 2F
203-3 Donggyo-dong,
Mapo-gu, Seoul, Korea. 03992
www.grecodesign.co.kr
T.+82-2-336-2082 F.+82-2-336-2297

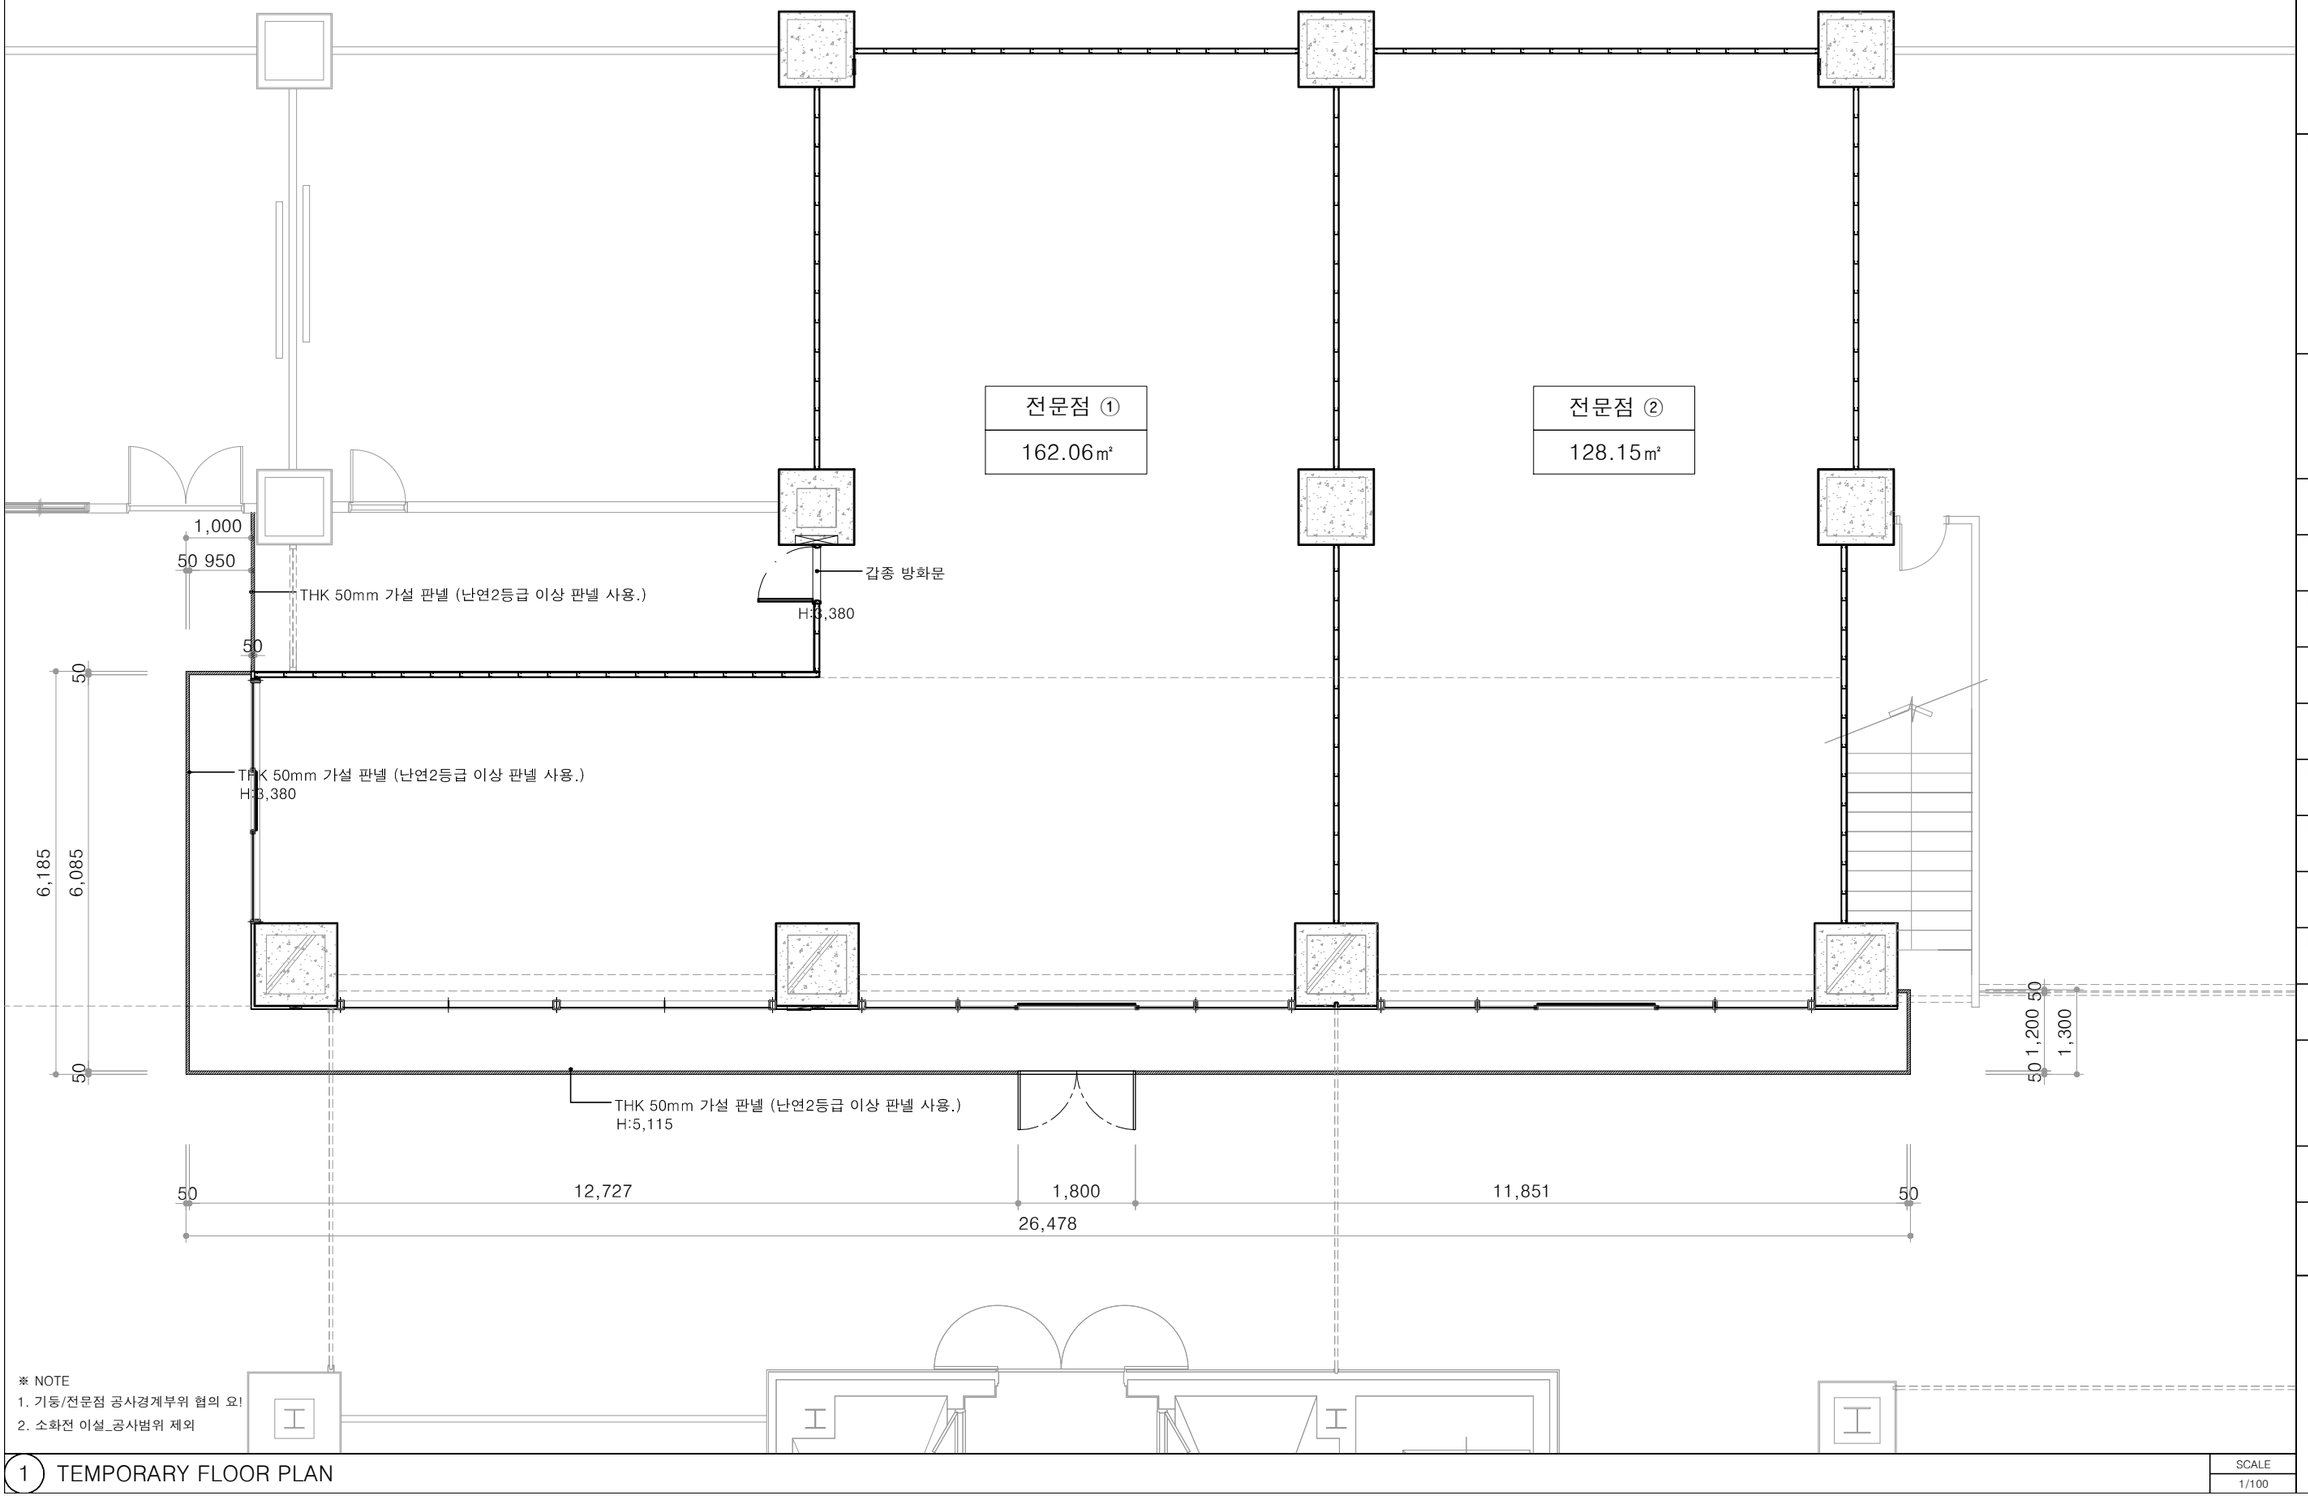

※ NOTE
1. 기둥/전문점 공사경계부위 협의 요!
2. 소화전 이설_공사범위 제외

1 TEMPORARY FLOOR PLAN

SCALE 1/100

KORAIL RETAIL
서울시 영등포구 당산3가 2-7
TEL / 02) 2630-8945
FAX / 02) 2630-8926

StoryWay

NOTE / REVISION

전문점 1: 162.06㎡
전문점 2: 128.15㎡
역사 건물 CH:5,115
매장 마감 CH:3,200 (마감제외)

NAME OF PROJECT

부산역 Project_1F
전문점①,②

ARCHITECTURE

STRUCTURE

MECHANIC

ELECTRIC

APPROVED BY

DESIGNED BY

DRAWING BY
Park, H. R.

CHECKED BY
Kim, S.C.

DATE
2018. 11.


SCALE
1 / 100

DRAWING TITLE
TEMPORARY FLOOR PLAN

PROJECT NO.

SHEET NO.	DRAWING NO.
103	I-103

Greco DESIGNGROUP
Sukjung Bldg. 2F
203-3 Donggyo-dong,
Mapo-gu, Seoul, Korea. 03992
www.grecodesign.co.kr
T.+82-2-336-2082 F.+82-2-336-2297

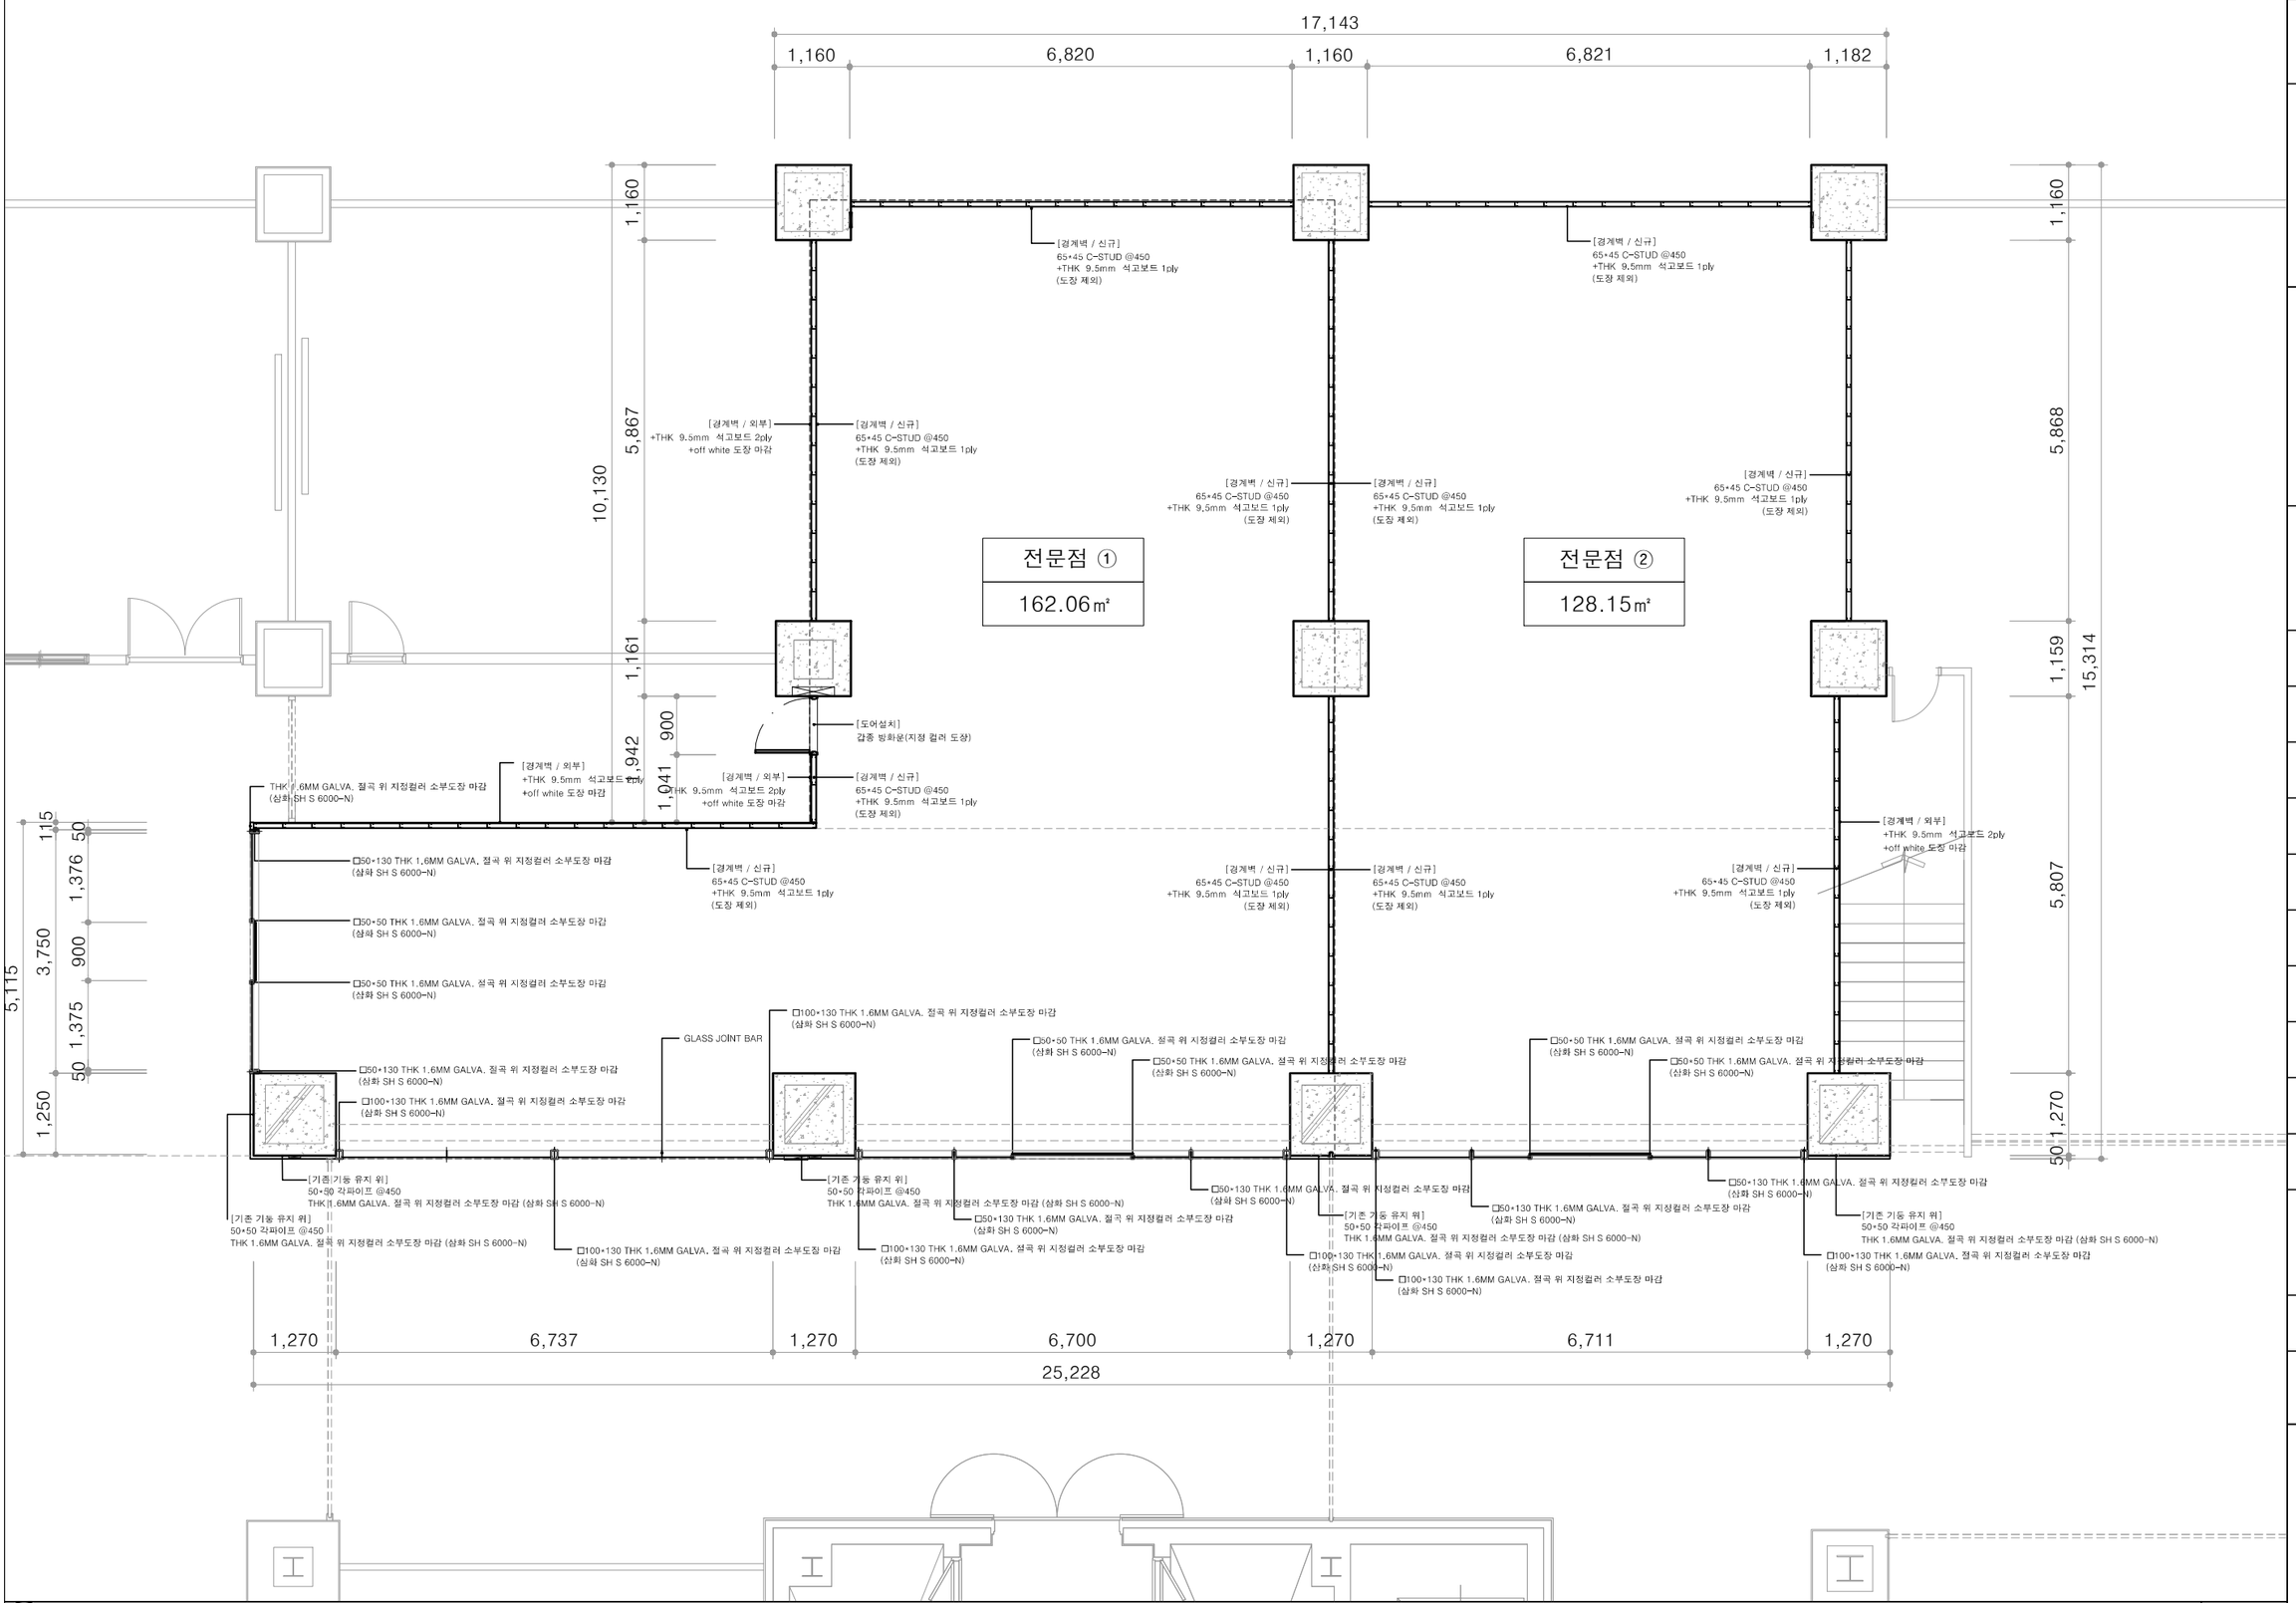

1 STRUCTURE PLAN

SCALE 1/100

KORAIL RETAIL
서울시 영등포구 당산3가 2-7
TEL / 02) 2630-8945
FAX / 02) 2630-8926

StoryWay

NOTE / REVISION

전문점 1: 162.06㎡
전문점 2: 128.15㎡
역사 건물 CH:5,115
매장 마감 CH:3,200 (마감제외)

NAME OF PROJECT

부산역 Project_1F
전문점①,②

ARCHITECTURE

STRUCTURE

MECHANIC

ELECTRIC

APPROVED BY

DESIGNED BY

DRAWING BY
Park, H. R.

CHECKED BY
Kim, S.C.

DATE
2018. 11.


SCALE
1 / 100

DRAWING TITLE
STRUCTURE PLAN

PROJECT NO.

SHEET NO.	DRAWING NO.
104	I-104

Greco DESIGNGROUP
Sukjung Bldg. 2F
203-3 Donggyo-dong,
Mapo-gu, Seoul, Korea. 03992
www.grecodesign.co.kr
T.+82-2-336-2082 F.+82-2-336-2297

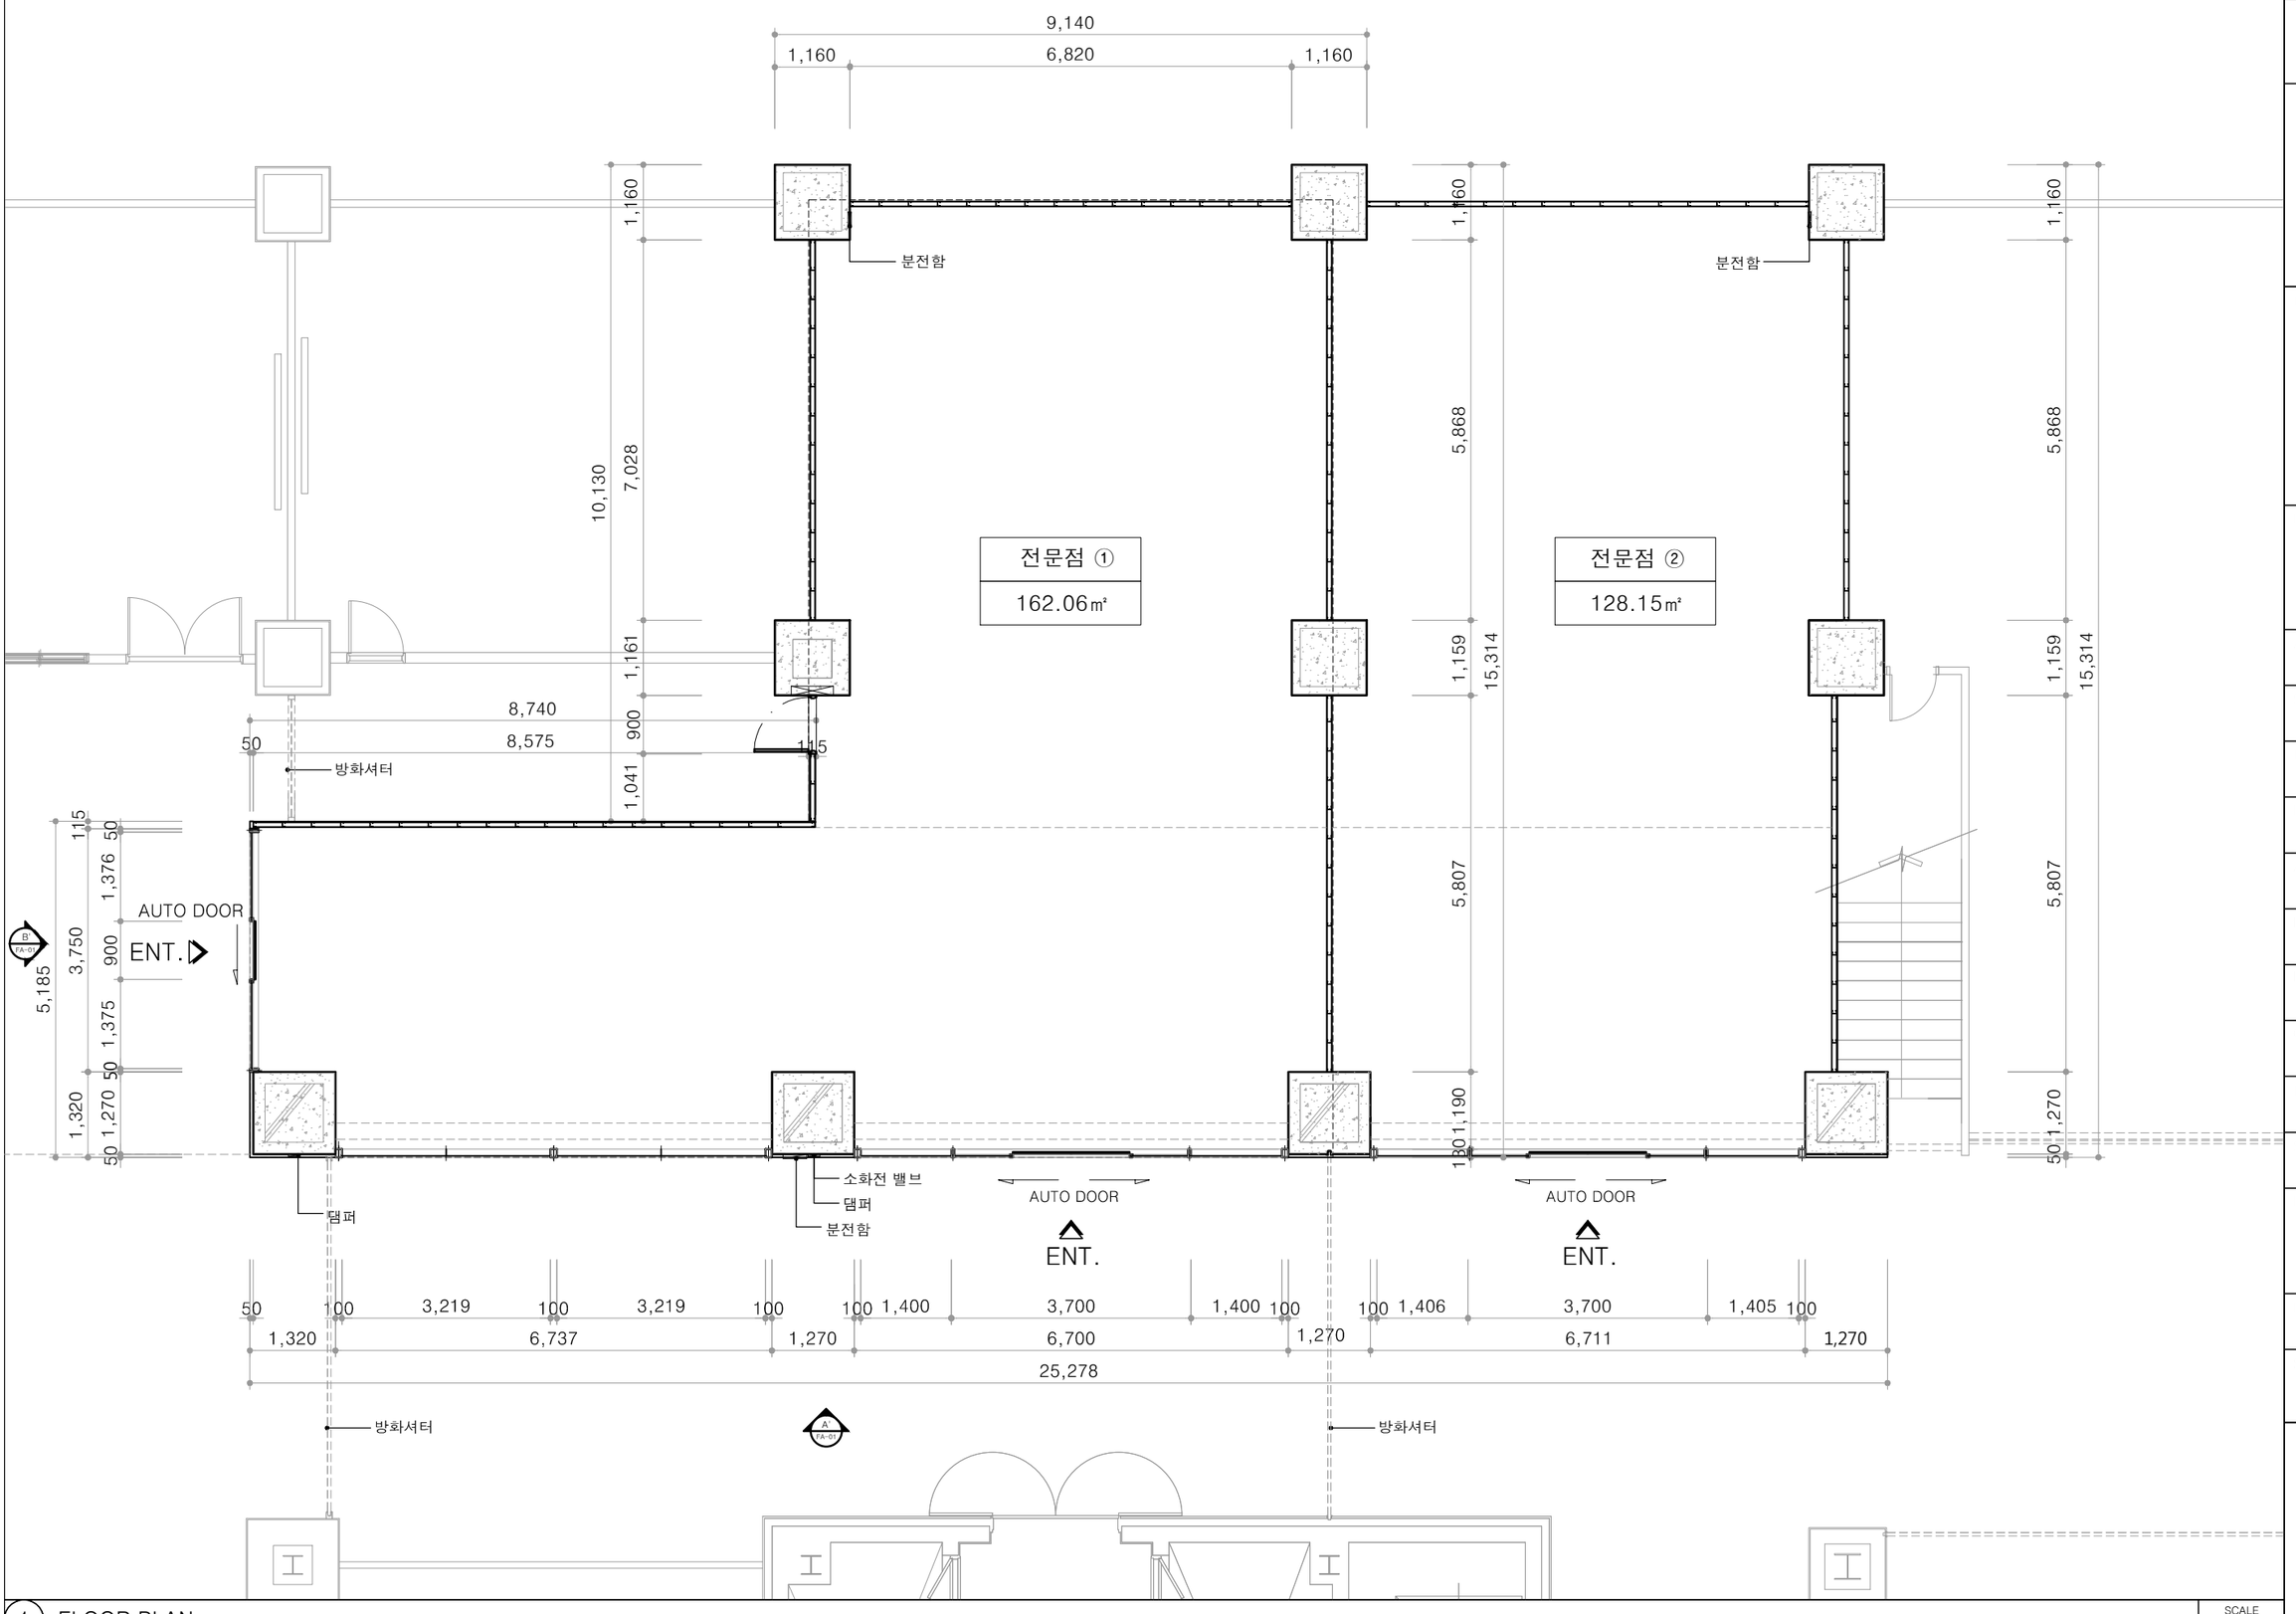

1 FLOOR PLAN

SCALE 1/100

KORAIL RETAIL
서울시 영등포구 당산3가 2-7
TEL / 02) 2630-8945
FAX / 02) 2630-8926

StoryWay

NOTE / REVISION

전문점 1: 162.06㎡
전문점 2: 128.15㎡
역사 건물 CH:5,115
매장 마감 CH:3,200 (마감제외)

NAME OF PROJECT

부산역 Project_1F
전문점①,②

ARCHITECTURE

STRUCTURE

MECHANIC

ELECTRIC

APPROVED BY

DESIGNED BY

DRAWING BY
Park, H. R.

CHECKED BY
Kim, S.C.

DATE
2018. 11.


SCALE
1 / 100

DRAWING TITLE
FLOOR PLAN

PROJECT NO.

SHEET NO.	DRAWING NO.
105	I-105

Greco DESIGNGROUP
Sukjung Bldg. 2F
203-3 Donggyo-dong,
Mapo-gu, Seoul, Korea. 03992
www.grecodesign.co.kr
T.+82-2-336-2082 F.+82-2-336-2297

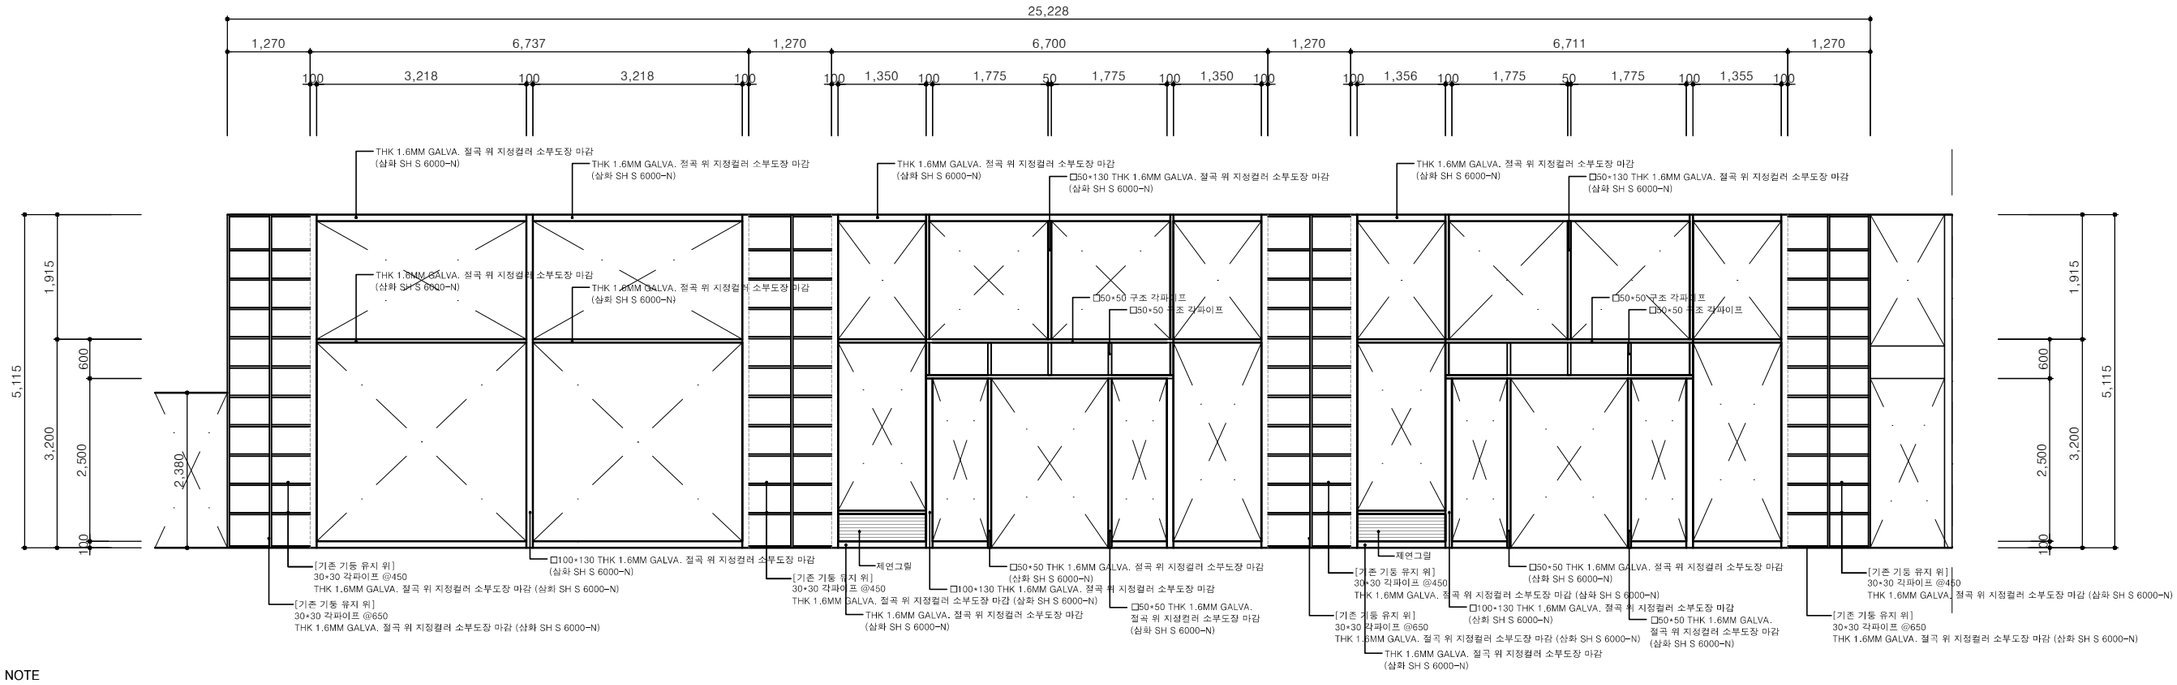


※ NOTE

1. 코레일 유통 협의사항 : 제연그릴 위치 CON'F 요!

1 FACADE STRUCTURE PLAN A'

SCALE 1/100

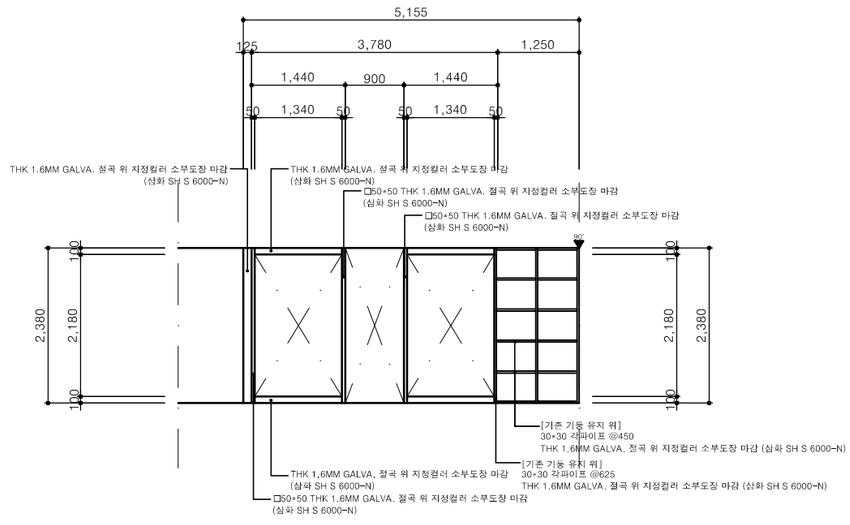

2 FACADE STRUCTURE PLAN B'

SCALE 1/100

KORAIL RETAIL
서울시 영등포구 당산3가 2-7
TEL / 02) 2630-8945
FAX / 02) 2630-8926

StoryWay

NOTE / REVISION

전문점 1: 162.06㎡
전문점 2: 128.15㎡
역사 건물 CH:5,115
매장 마감 CH:3,200 (마감제외)

NAME OF PROJECT

부산역 Project_1F
전문점①,②

ARCHITECTURE

STRUCTURE

MECHANIC

ELECTRIC

APPROVED BY

DESIGNED BY

DRAWING BY
Park, H. R.

CHECKED BY
Kim, S.C.

DATE
2018. 11.


SCALE
1 / 100

DRAWING TITLE
FACADE STRUCTURE PLAN

PROJECT NO.

SHEET NO.	DRAWING NO.
201	I-201


Greco DESIGNGROUP
Sukjung Bldg. 2F
203-3 Donggyo-dong,
Mapo-gu, Seoul, Korea. 03992
www.grecodesign.co.kr
T.+82-2-336-2082 F.+82-2-336-2297

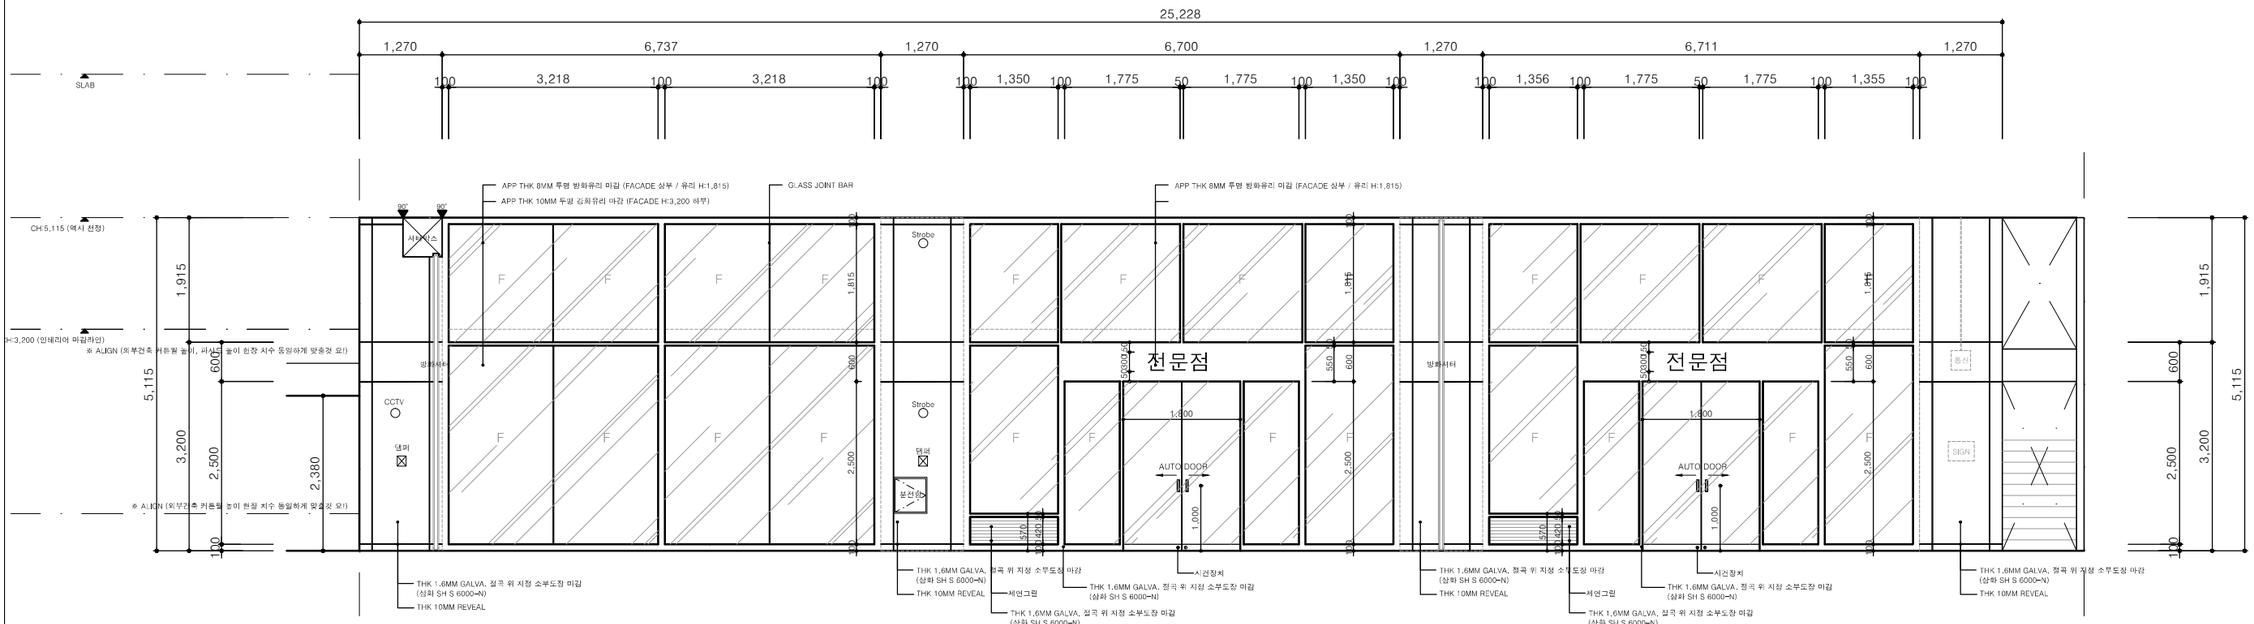

※ NOTE
1. 코레일 유통 협의사항 : 제연그릴 위치 CON'F 요!
2. 건축설비 마감 : 공사범위 제외

1 FACADE PLAN A'

SCALE 1/100

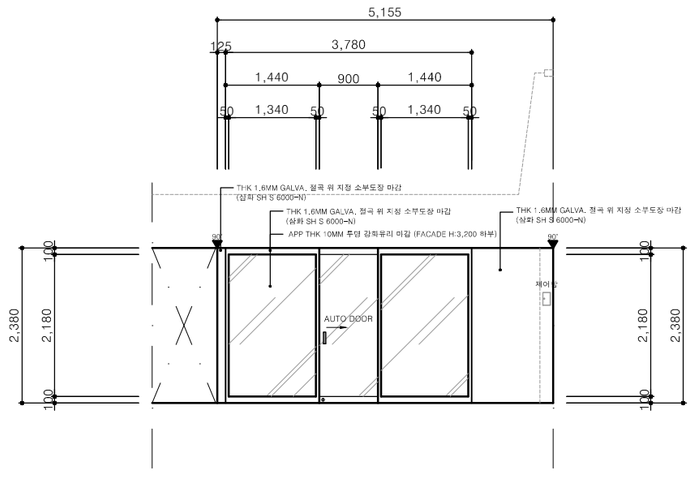

2 FACADE PLAN B'

SCALE 1/100

KORAIL RETAIL
서울시 영등포구 당산3가 2-7
TEL / 02) 2630-8945
FAX / 02) 2630-8926

StoryWay

NOTE / REVISION

전문점 1: 162.06㎡
전문점 2: 128.15㎡
역사 건물 CH:5,115
매장 마감 CH:3,200 (마감제외)

NAME OF PROJECT

부산역 Project_1F
전문점①,②

ARCHITECTURE

STRUCTURE

MECHANIC

ELECTRIC

APPROVED BY

DESIGNED BY

DRAWING BY
Park, H. R.

CHECKED BY
Kim, S.C.

DATE
2018. 11.

SCALE
1 / 100


DRAWING TITLE
FACADE PLAN

PROJECT NO.

SHEET NO. 202


DRAWING NO. I-202

Greco DESIGNGROUP
Sukjung Bldg. 2F
203-3 Donggyo-dong,
Mapo-gu, Seoul, Korea. 03992
www.grecodesign.co.kr
T.+82-2-336-2082 F.+82-2-336-2297

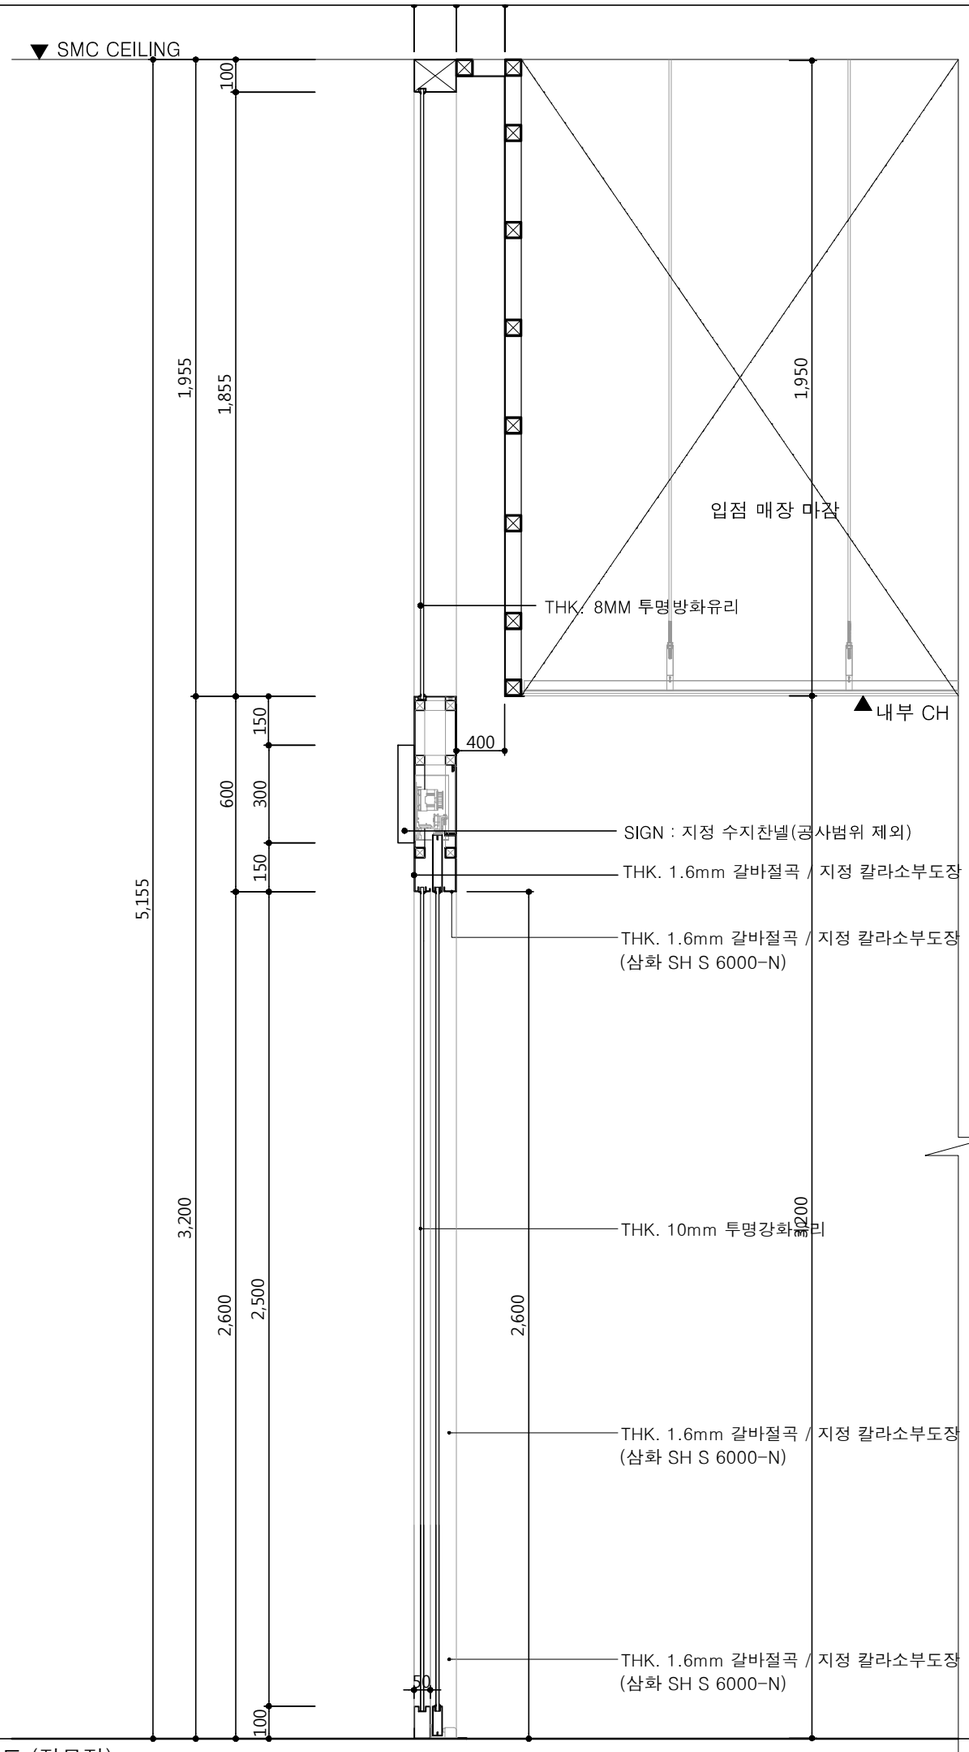

1 출입구 단면 상세도 (전문점)

SCALE 1/20

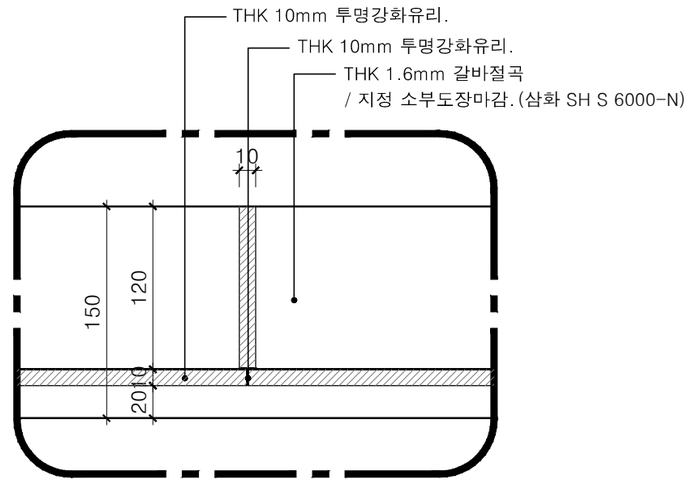

2 GLASS JOINT DETAIL

SCALE NONE

KORAIL RETAIL
서울시 영등포구 당산3가 2-7
TEL / 02) 2630-8945
FAX / 02) 2630-8926

StoryWay

NOTE / REVISION

NAME OF PROJECT
부산역 Project_1F
전문점①,②

ARCHITECTURE

STRUCTURE

MECHANIC

ELECTRIC

APPROVED BY

DESIGNED BY

DRAWING BY
Park, H. R.

CHECKED BY
Kim, S.C.

DATE
2018. 11.


SCALE
1 / 20, NONE

DRAWING TITLE
DETAIL
출입구 단면 상세도, GLASS JOINT

PROJECT NO.

SHEET NO.	DRAWING NO.
301	D-301

Greco DESIGNGROUP
Sukjung Bldg. 2F
203-3 Donggyo-dong,
Mapo-gu, Seoul. Korea. 03992
www.grecodesign.co.kr
T.+82-2-336-2082 F.+82-2-336-2297

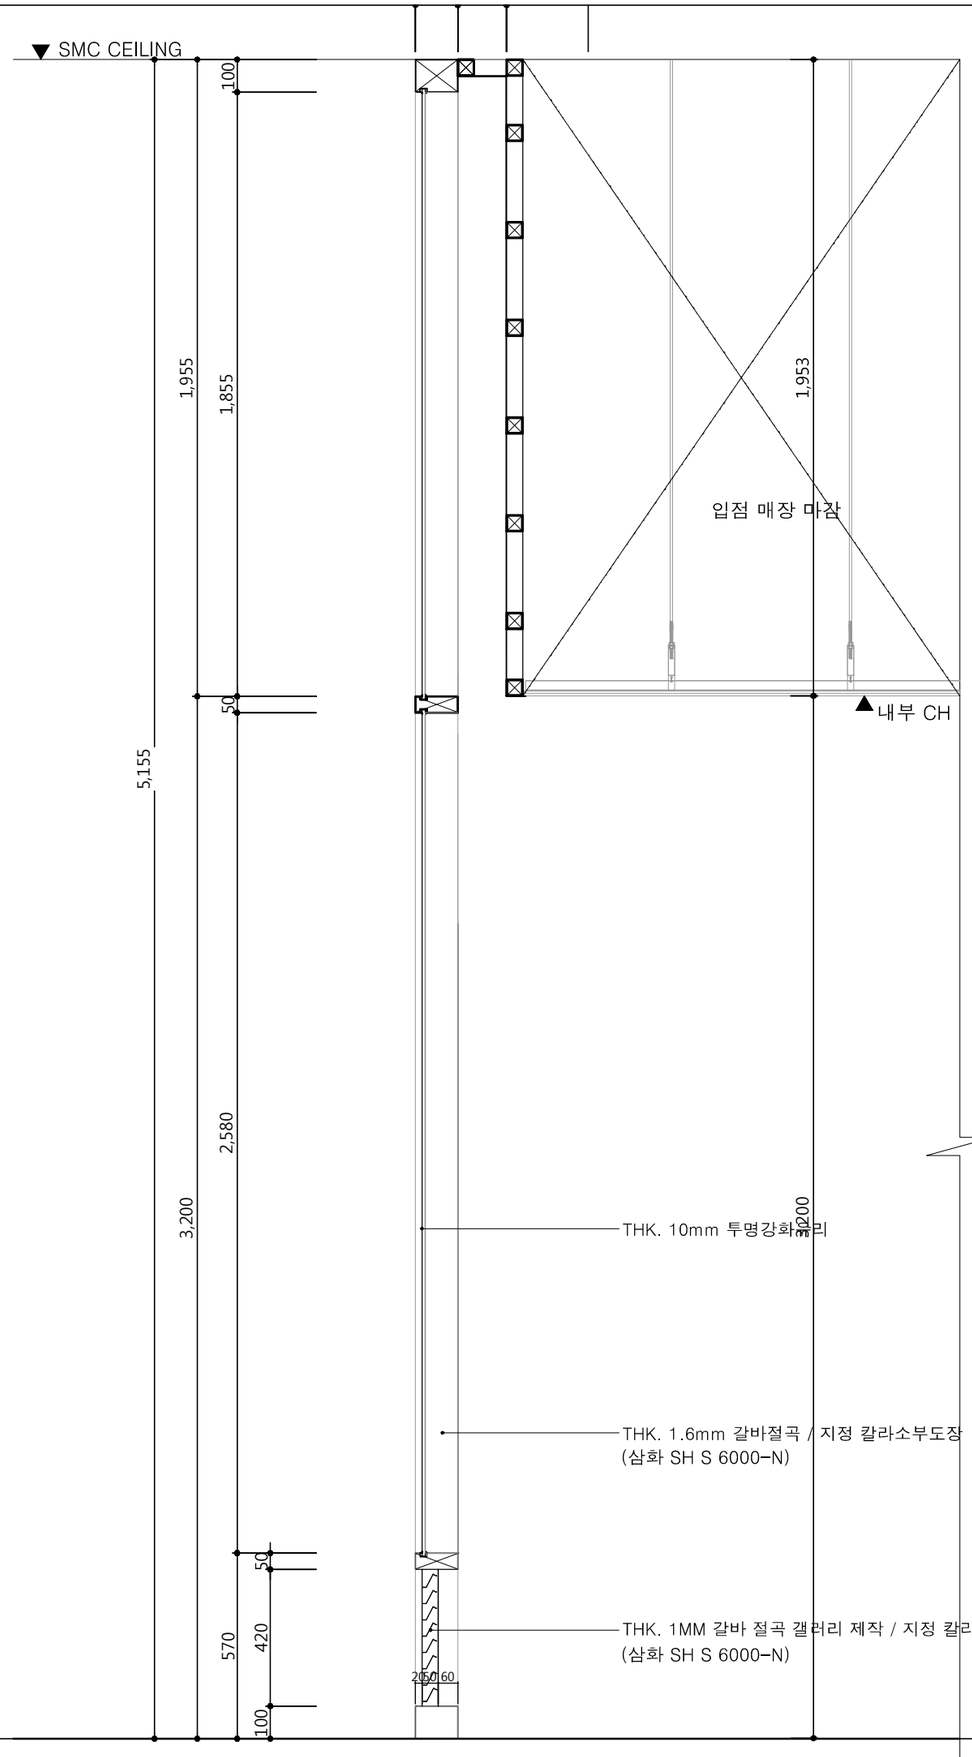

1 파사드 & 단면 커튼박스 상세도 (전문점)

SCALE 1/20

KORAIL RETAIL
서울시 영등포구 당산3가 2-7
TEL / 02) 2630-8945
FAX / 02) 2630-8926

StoryWay

NOTE / REVISION

NAME OF PROJECT
부산역 Project_1F
전문점①,②

ARCHITECTURE

STRUCTURE

MECHANIC

ELECTRIC

APPROVED BY

DESIGNED BY

DRAWING BY
Park, H. R.

CHECKED BY
Kim, S.C.

DATE
2018. 11.

SCALE
1 / 20

DRAWING TITLE
DETAIL
파사드 & 커튼박스 단면 상세도

PROJECT NO.

SHEET NO.	DRAWING NO.
302	D-302

Greco DESIGNGROUP
Sukjung Bldg. 2F
203-3 Donggyo-dong,
Mapo-gu, Seoul, Korea. 03992
www.grecodesign.co.kr
T.+82-2-336-2082 F.+82-2-336-2297