
KORAIL RETAIL

부산역 3층 맛이방 전문점 신축공사

2018. 01.

코레일유통(주)

Greco DESIGNGROUP

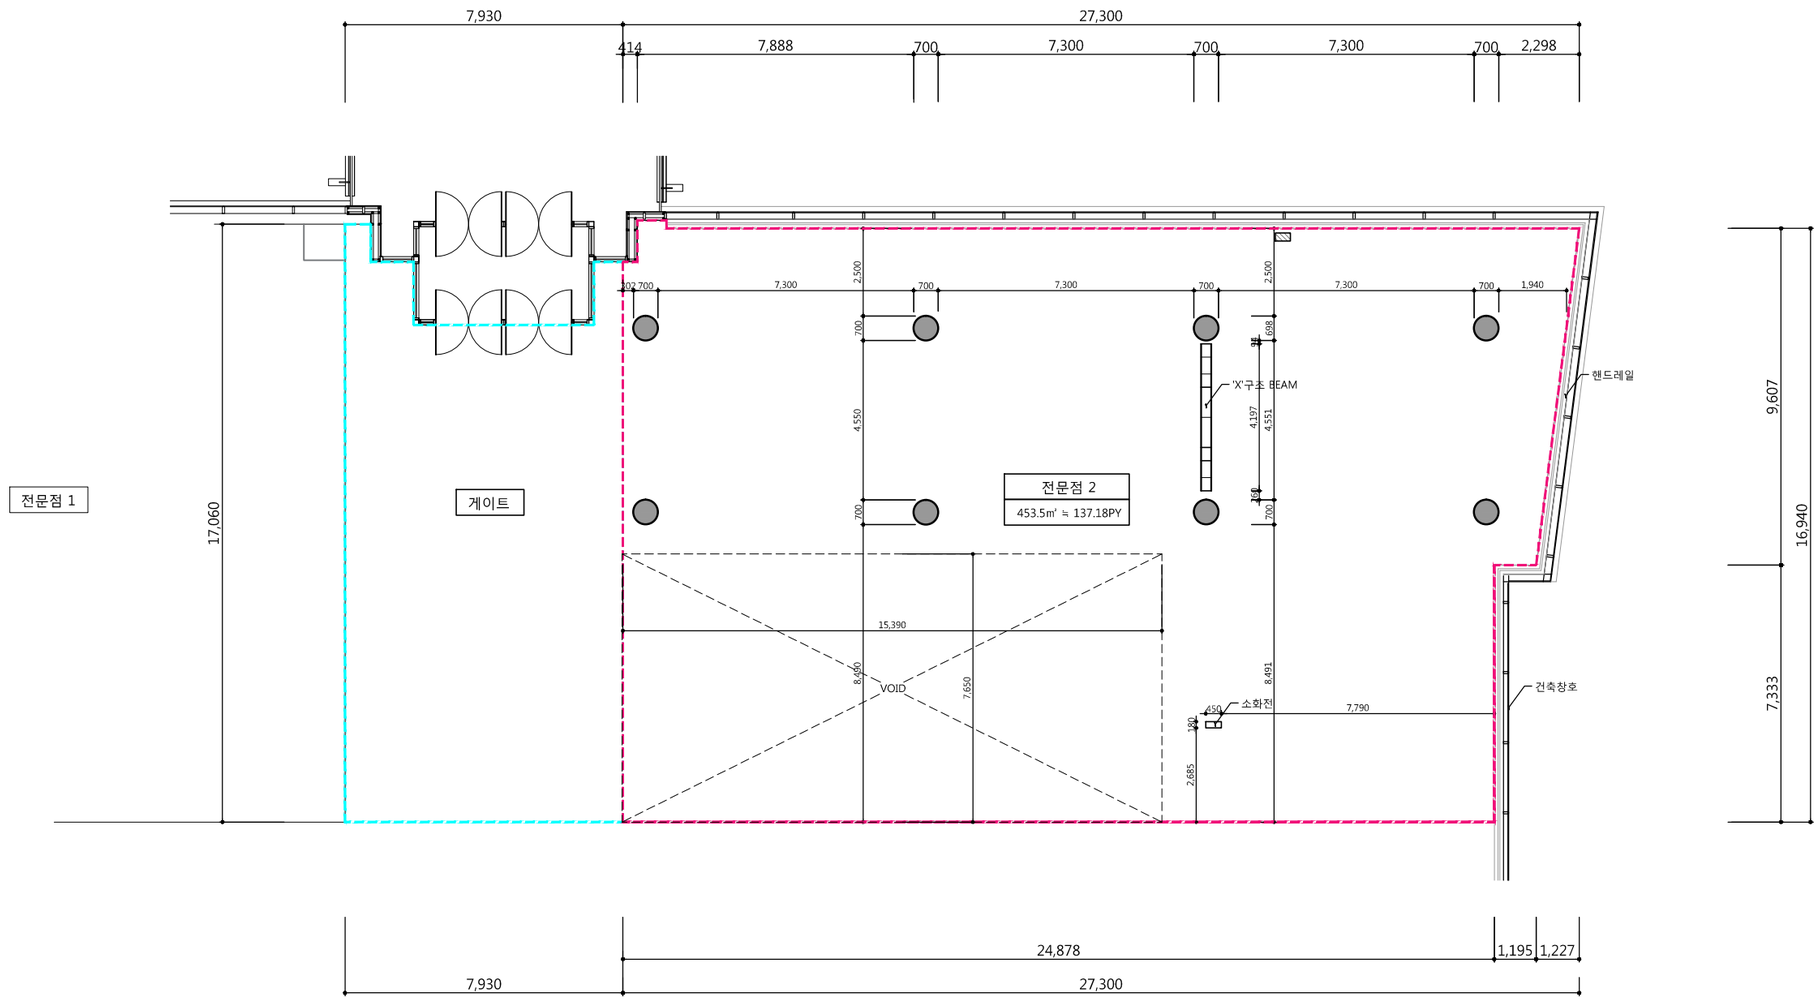

■ LEGEND

	DESCRIPTION	SYMBOL	Q'TY	DESCRIPTION
PT 01	PANTONE COLOR #COOL GRAY 9C			
GL 01	투명 강화유리 THK. 10MM			

■ NOTES

※ 철거범위 : 현재 가설 설치되어 있으나 실제 공사범위가 더 확장되므로 가설 이설 필요.

1 SCALE 1/120 **BASE FLOOR PLAN**

KORAIL RETAIL
서울시 영등포구 당산3가 2-7
TEL / 02) 2630-8945
FAX / 02) 2630-8926

StoryWay

NOTE / REVISION

전문점 2 : 453.5㎡ (137.18PY)

NAME OF PROJECT

부산역 3F 맞이방 전문점 2

ARCHITECTURE

STRUCTURE

MECHANIC

ELECTRIC

APPROVED BY

DESIGNED BY

DRAWING BY
Park, Hyeran

CHECKED BY
Choi, Jinha

DATE
2017. 01. 08


SCALE
1 / 120

DRAWING TITLE
BASE FLOOR PLAN

PROJECT NO.

SHEET NO.	DRAWING NO.
003	I-001

Greco DESIGNGROUP
Sukjung Bldg. 2F
203-3 Donggyo-dong,
Mapo-gu, Seoul, Korea. 03992
www.grecodesign.co.kr
T.+82-2-336-2082 F.+82-2-336-2297

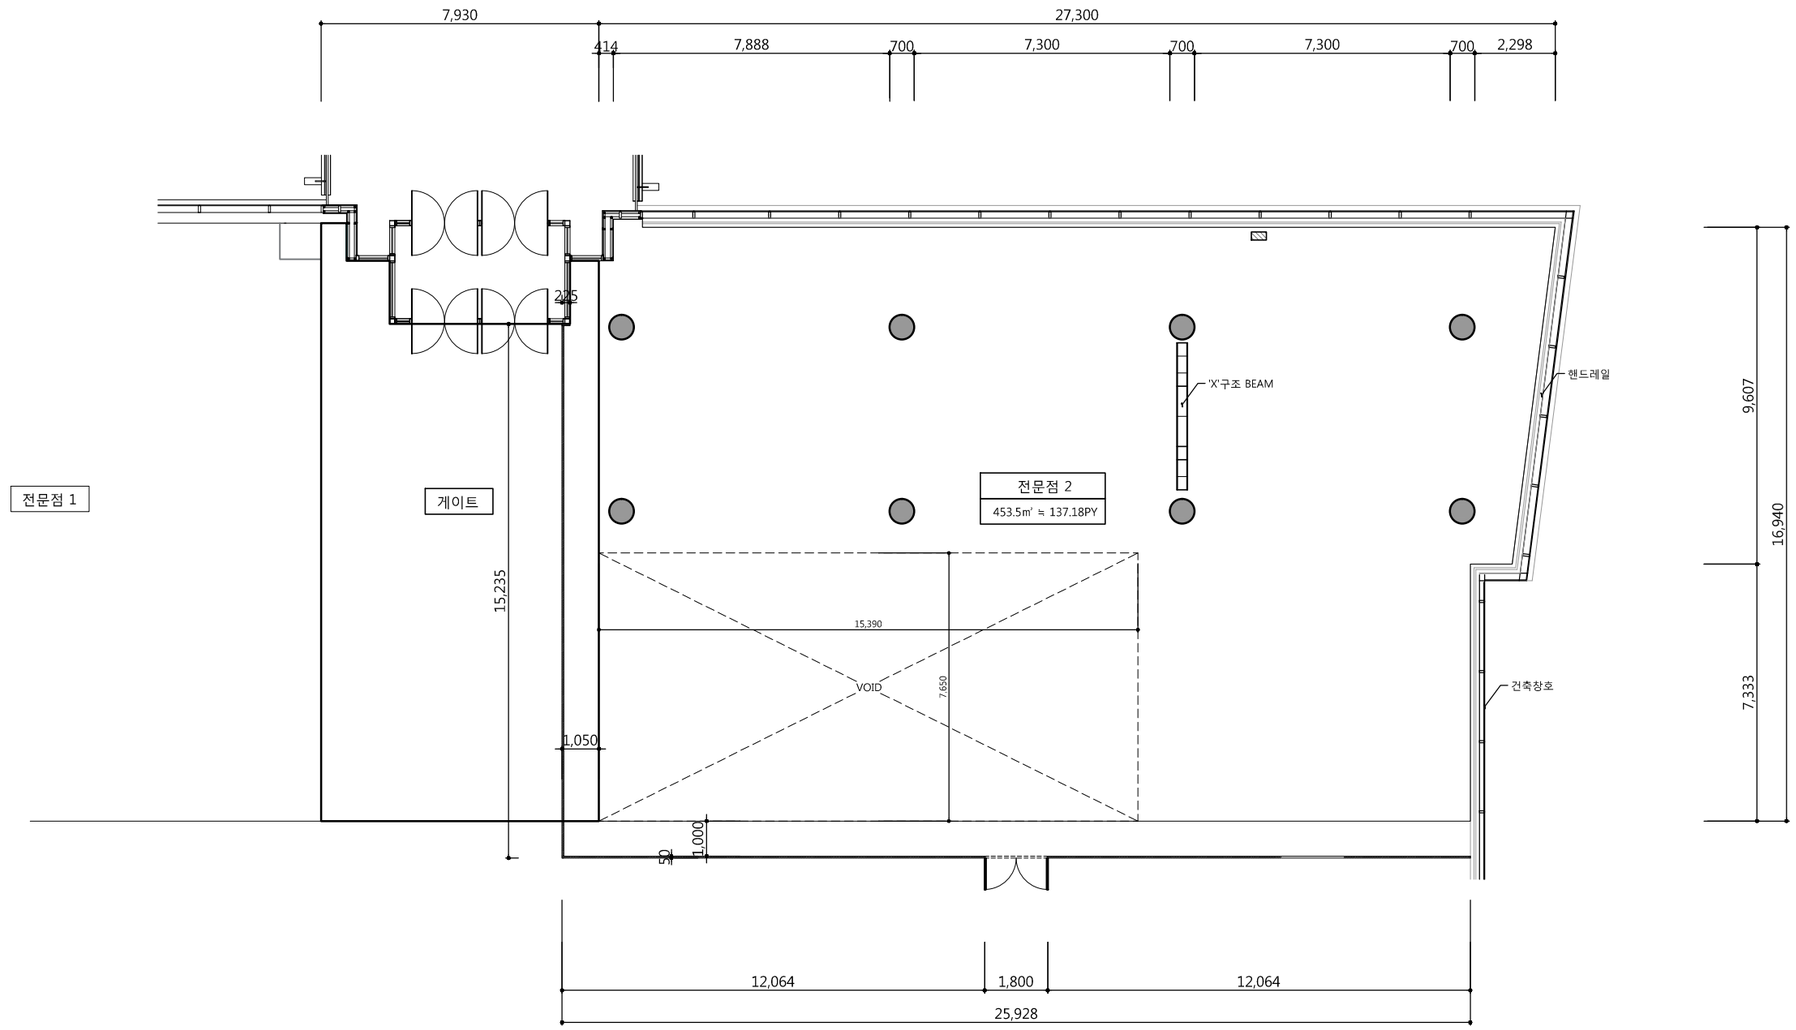

■ LEGEND

	DESCRIPTION	SYMBOL	Q'TY	DESCRIPTION
PT 01	PANTONE COLOR #COOL GRAY 9C			
GL 01	투명 강화유리 THK. 10MM			

■ NOTES

※ 철거범위 : 현재 가설 설치되어 있으나 실제 공사범위가 더 확장되므로 가설 이설 필요.

1 SCALE 1/120 **TEMPORARY WALL PLAN**

KORAIL RETAIL
서울시 영등포구 당산3가 2-7
TEL / 02) 2630-8945
FAX / 02) 2630-8926

StoryWay

NOTE / REVISION

전문점 2 : 453.5㎡ (137.18PY)

NAME OF PROJECT

부산역 3F 맞이방 전문점 2

ARCHITECTURE

STRUCTURE

MECHANIC

ELECTRIC

APPROVED BY

DESIGNED BY

DRAWING BY
Park, Hyeran

CHECKED BY
Choi, Jinha

DATE
2017. 01. 08


SCALE
1 / 120

DRAWING TITLE
TEMPORARY WALL PLAN

PROJECT NO.

SHEET NO.	DRAWING NO.
003	I-001

Greco DESIGNGROUP
Sukjung Bldg. 2F
203-3 Donggyo-dong,
Mapo-gu, Seoul, Korea. 03992
www.grecodesign.co.kr
T.+82-2-336-2082 F.+82-2-336-2297

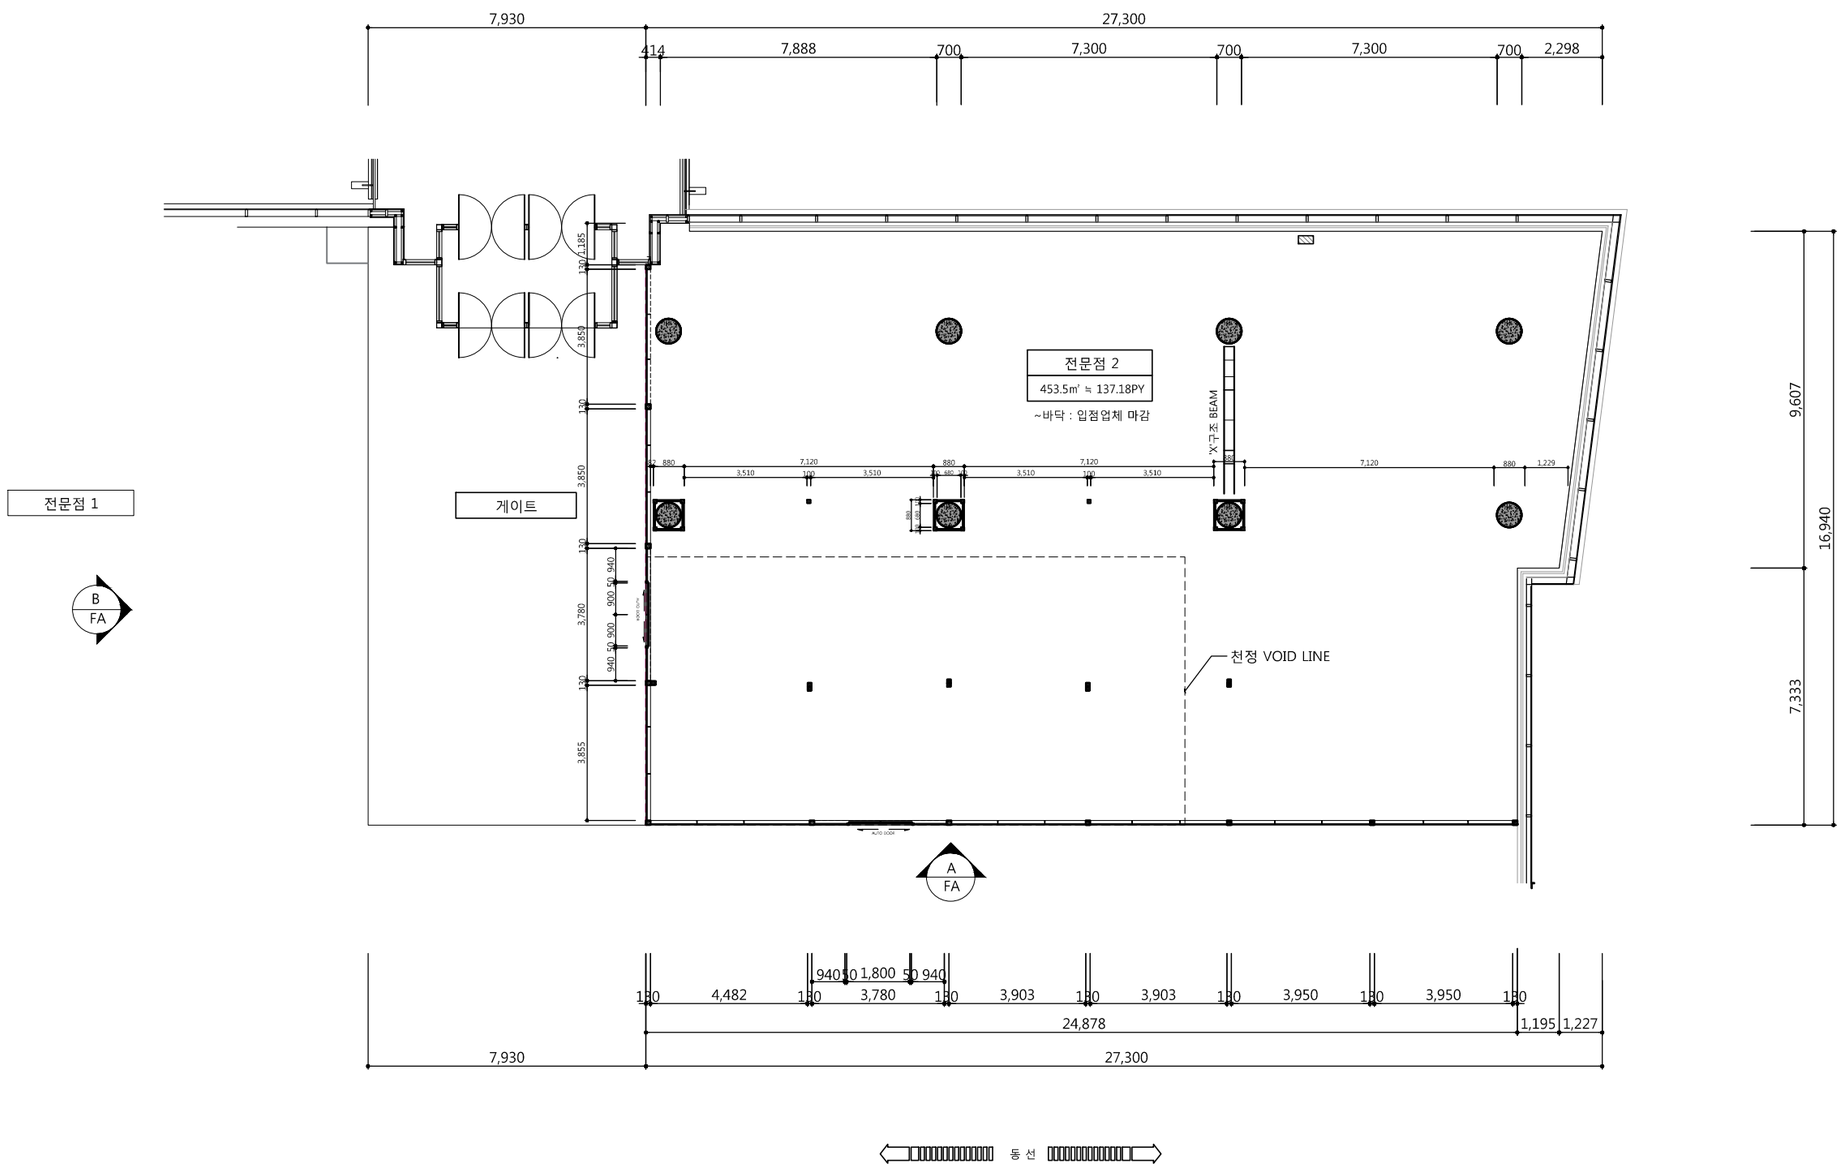

■ LEGEND

	DESCRIPTION	SYMBOL	Q'TY	DESCRIPTION
PT 01	PANTONE COLOR #COOL GRAY 9C			
GL 01	투명 강화유리 THK. 10MM			

■ NOTES

※ 철거범위 :

1 SCALE 1/120 **FLOOR PLAN**

KORAIL RETAIL

서울시 영등포구 당산3가 2-7
TEL / 02) 2630-8945
FAX / 02) 2630-8926

StoryWay

NOTE / REVISION

전문점 2 : 453.5㎡ (137.18PY)

NAME OF PROJECT

부산역 3F 맞이방 전문점 2

ARCHITECTURE

STRUCTURE

MECHANIC

ELECTRIC

APPROVED BY

DESIGNED BY

DRAWING BY
Park, Hyeran

CHECKED BY
Choi, Jinha

DATE
2017. 01. 08

SCALE
1 / 120

DRAWING TITLE
FLOOR PLAN


PROJECT NO.

SHEET NO. **003**

DRAWING NO. **I-001**

Greco DESIGNGROUP

Sukjung Bldg. 2F
203-3 Donggyo-dong,
Mapo-gu, Seoul, Korea, 03992
www.grecodesign.co.kr
T.+82-2-336-2082 F.+82-2-336-2297

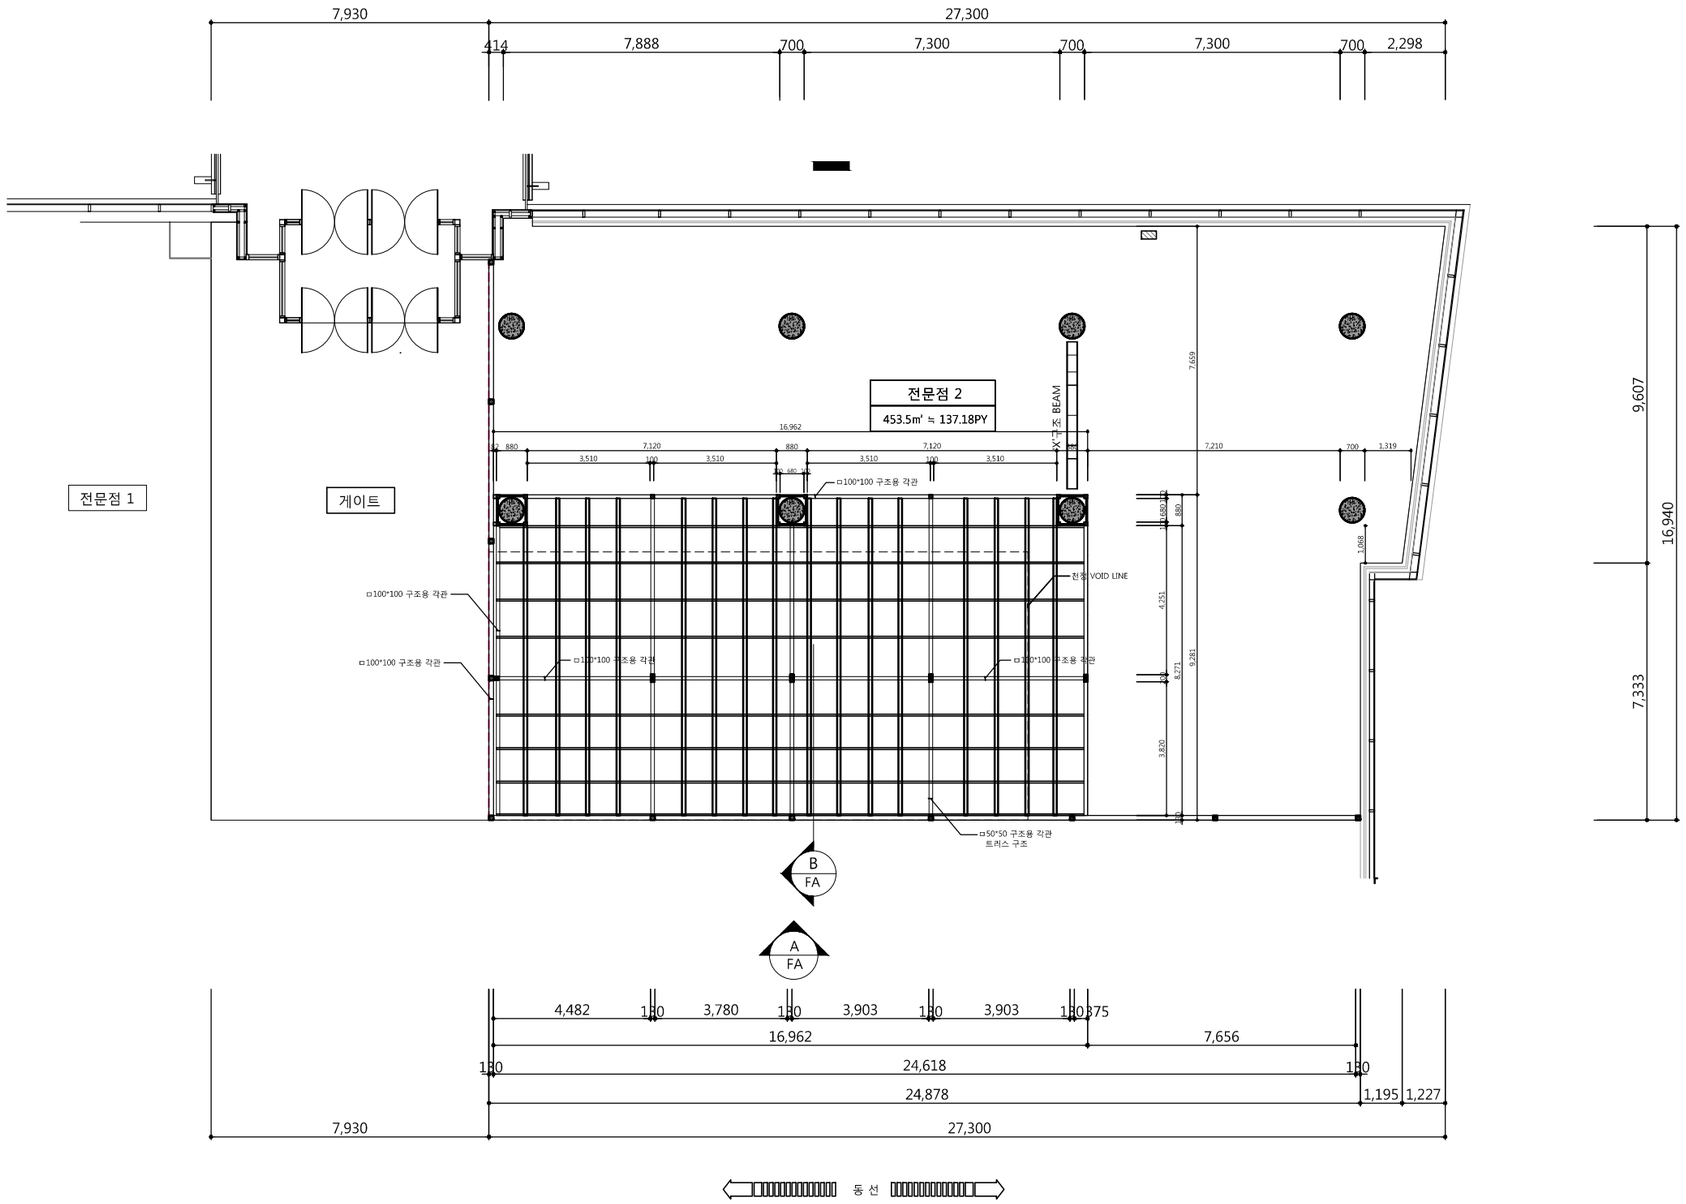

■ LEGEND

	DESCRIPTION	SYMBOL	Q'TY	DESCRIPTION
PT 01	PANTONE COLOR #COOL GRAY 9C			
GL 01	투명 강화유리 THK. 10MM			

■ NOTES

※ 철거범위 : 현재 가설 설치되어 있으나 실제 공사범위가 더 확장되므로 가설 이설 필요.

1 SCALE 1/120 **STRUCTURE CEILING PLAN**

KORAIL RETAIL

서울시 영등포구 당산3가 2-7
TEL / 02) 2630-8945
FAX / 02) 2630-8926

StoryWay

NOTE / REVISION

전문점 2 : 453.5㎡ (137.18PY)

NAME OF PROJECT

부산역 3F 맞이방 전문점 2

ARCHITECTURE

STRUCTURE

MECHANIC

ELECTRIC

APPROVED BY

DESIGNED BY

DRAWING BY
Park, Hyeran

CHECKED BY
Choi, Jinha

DATE
2017. 01. 08

SCALE
1 / 120


DRAWING TITLE
STRUCTURE CEILING PLAN

PROJECT NO.

SHEET NO. 003

DRAWING NO. I-001

Greco DESIGNGROUP
Sukjung Bldg. 2F
203-3 Donggyo-dong,
Mapo-gu, Seoul, Korea, 03992
www.grecodesign.co.kr
T.+82-2-336-2082 F.+82-2-336-2297

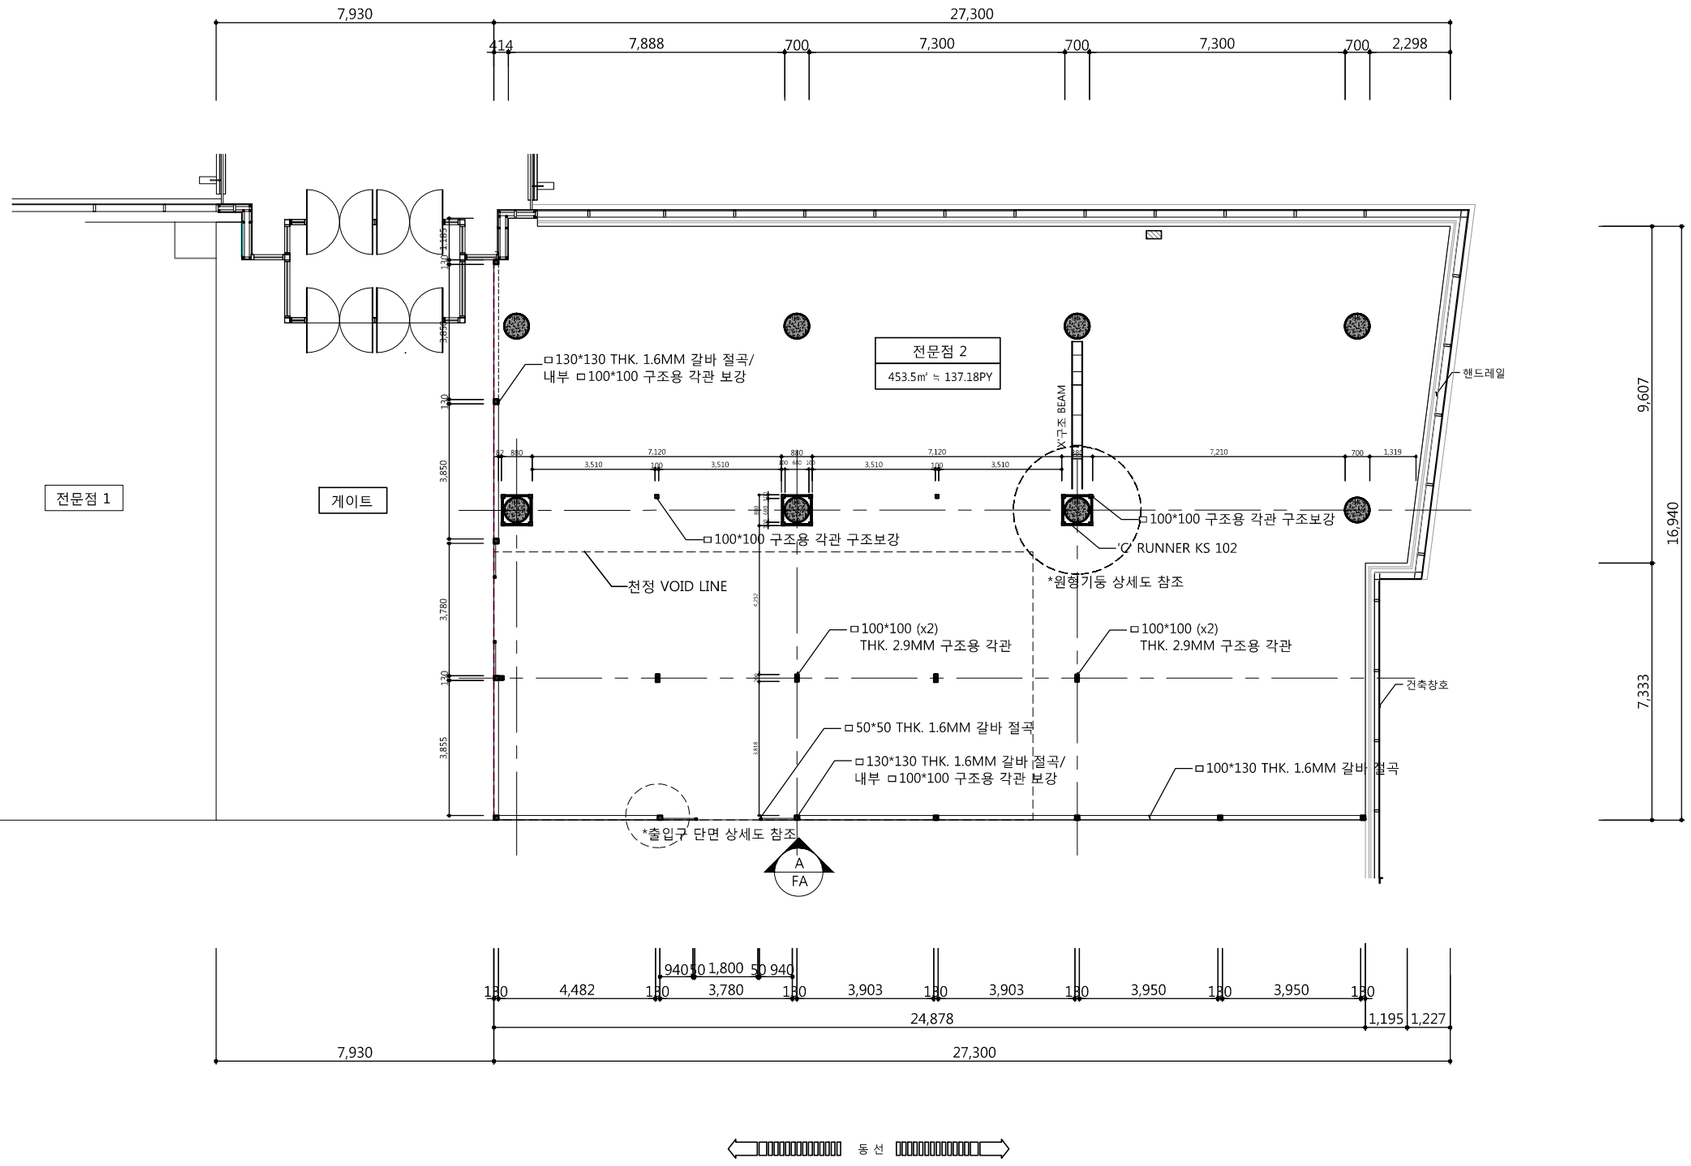

■ LEGEND

	DESCRIPTION	SYMBOL	Q'TY	DESCRIPTION
PT 01	PANTONE COLOR #COOL GRAY 9C			
GL 01	투명 강화유리 THK. 10MM			

■ NOTES

※ 철거범위 : 현재 가설 설치되어 있으나 실제 공사범위가 더 확장되므로 가설 이설 필요.

1 SCALE 1/120 **STRUCTURE PLAN**

KORAIL RETAIL

서울시 영등포구 당산3가 2-7
TEL / 02) 2630-8945
FAX / 02) 2630-8926

StoryWay

NOTE / REVISION

전문점 2 : 453.5㎡ (137.18PY)

NAME OF PROJECT

부산역 3F 맞이방 전문점 2

ARCHITECTURE

STRUCTURE

MECHANIC

ELECTRIC

APPROVED BY

DESIGNED BY

DRAWING BY
Park, Hyeran

CHECKED BY
Choi, Jinha

DATE
2017. 01. 08

SCALE
1 / 120


DRAWING TITLE
STRUCTURE PLAN

PROJECT NO.


SHEET NO. 003

DRAWING NO. I-001

Greco DESIGNGROUP
Sukjung Bldg. 2F
203-3 Donggyo-dong,
Mapo-gu, Seoul, Korea. 03992
www.grecodesign.co.kr
T.+82-2-336-2082 F.+82-2-336-2297

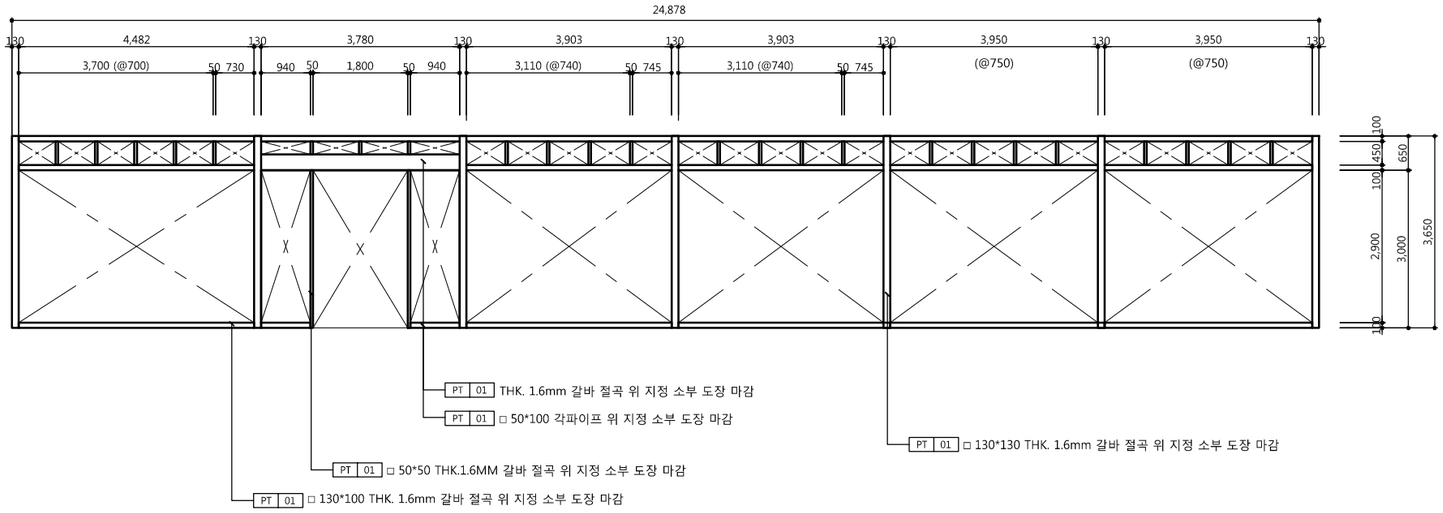

1 SCALE 1/80 **STRUCTURE ELEVATION A**

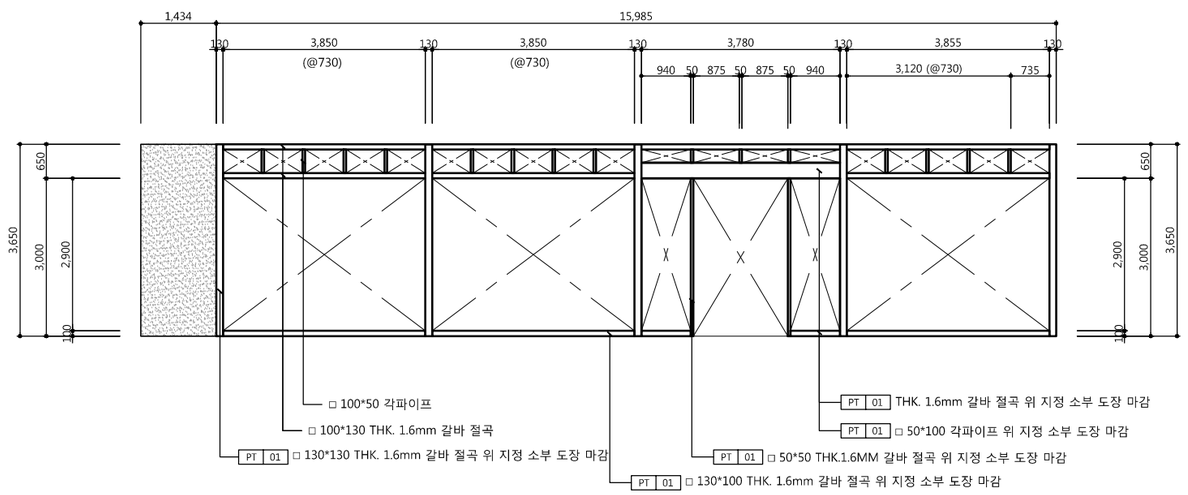

2 SCALE 1/80 **STRUCTURE ELEVATION B**

KORAIL RETAIL
서울시 영등포구 당산3가 2-7
TEL / 02) 2630-8945
FAX / 02) 2630-8926

StoryWay

NOTE / REVISION

전문점 2 : 453.5㎡ (137.18PY)

NAME OF PROJECT

부산역 3F 맞이방 전문점 2

ARCHITECTURE

STRUCTURE

MECHANIC

ELECTRIC

APPROVED BY

DESIGNED BY

DRAWING BY
Park, Hyeran

CHECKED BY
Choi, Jinha

DATE
2017. 01. 08

SCALE
1 / 80


DRAWING TITLE
STRUCTURE ELEVATION A, B

PROJECT NO.

SHEET NO. **003**

DRAWING NO. **I-001**

Greco DESIGNGROUP
Sukjung Bldg. 2F
203-3 Donggyo-dong,
Mapo-gu, Seoul, Korea. 03992
www.grecodesign.co.kr
T.+82-2-336-2082 F.+82-2-336-2297

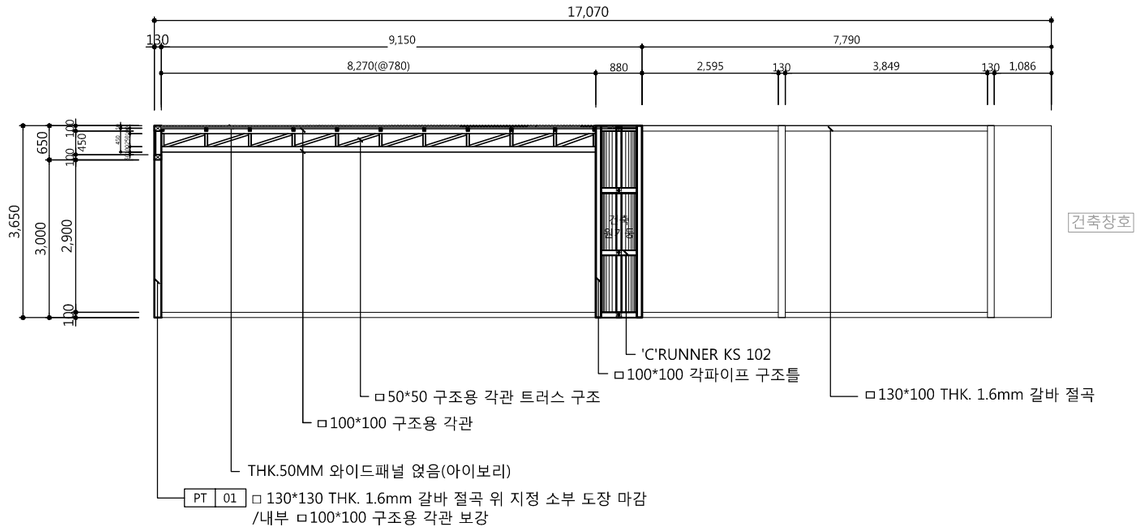

1 SCALE 1/80

STRUCTURE ELEVATION B

KORAIL RETAIL
서울시 영등포구 당산3가 2-7
TEL / 02) 2630-8945
FAX / 02) 2630-8926

StoryWay

NOTE / REVISION

전문점 2 : 453.5㎡ (137.18PY)

NAME OF PROJECT

부산역 3F 맞이방 전문점 2

ARCHITECTURE

STRUCTURE

MECHANIC

ELECTRIC

APPROVED BY

DESIGNED BY

DRAWING BY
Park, Hyeran

CHECKED BY
Choi, Jinha

DATE
2017. 01. 08

SCALE
1 / 80


DRAWING TITLE
STRUCTURE ELEVATION C, D

PROJECT NO.


SHEET NO. 003

DRAWING NO. I-001

Greco DESIGNGROUP
Sukjung Bldg. 2F
203-3 Donggyo-dong,
Mapo-gu, Seoul, Korea. 03992
www.grecodesign.co.kr
T.+82-2-336-2082 F.+82-2-336-2297

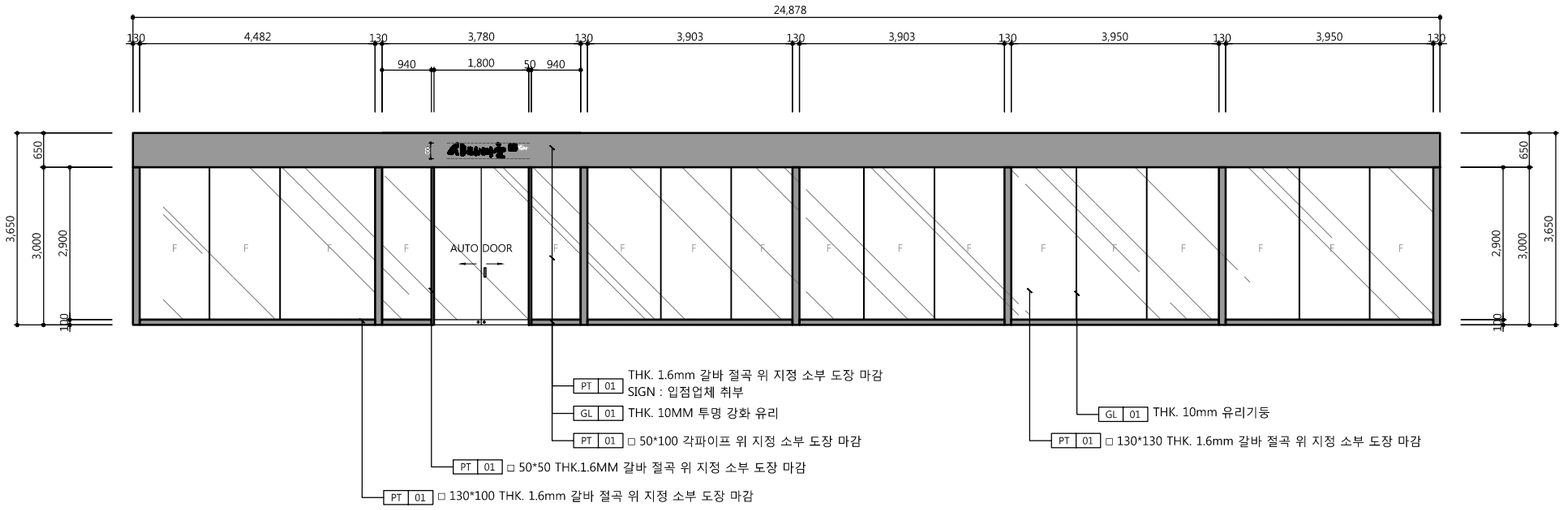

1 SCALE 1/80 **FACADE A**

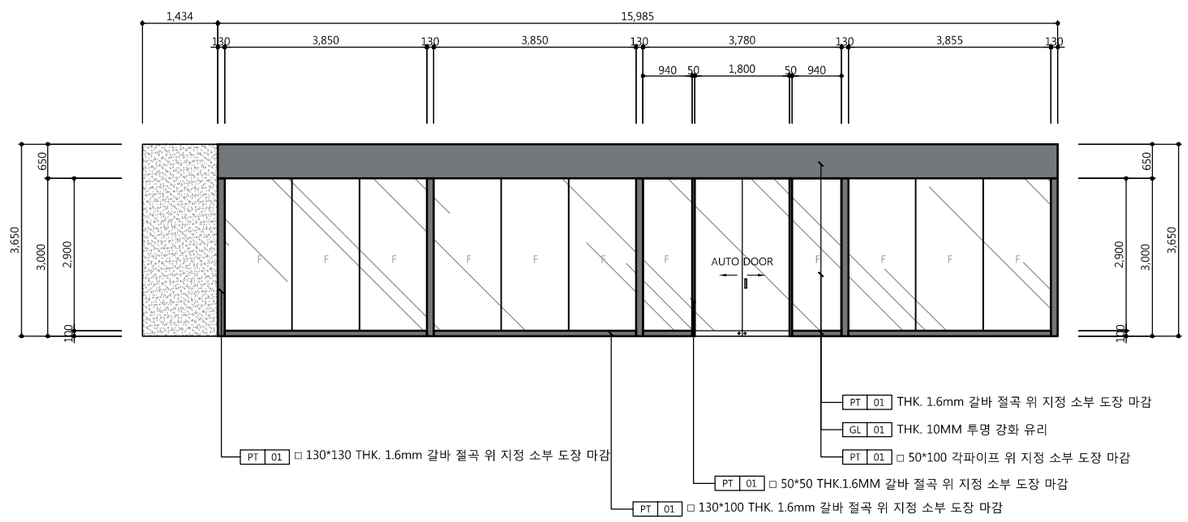

2 SCALE 1/80 **FACADE B**

KORAIL RETAIL
서울시 영등포구 당산3가 2-7
TEL / 02) 2630-8945
FAX / 02) 2630-8926

StoryWay

NOTE / REVISION

전문점 2 : 453.5㎡ (137.18PY)

NAME OF PROJECT

부산역 3F 맞이방 전문점 2

ARCHITECTURE

STRUCTURE

MECHANIC

ELECTRIC

APPROVED BY

DESIGNED BY

DRAWING BY
Park, Hyeran

CHECKED BY
Choi, Jinha

DATE
2017. 01. 08


SCALE
1 / 80

DRAWING TITLE
FACADE


PROJECT NO.

SHEET NO.	DRAWING NO.
003	I-001

Greco DESIGNGROUP
Sukjung Bldg. 2F
203-3 Donggyo-dong,
Mapo-gu, Seoul, Korea. 03992
www.grecodesign.co.kr
T.+82-2-336-2082 F.+82-2-336-2297

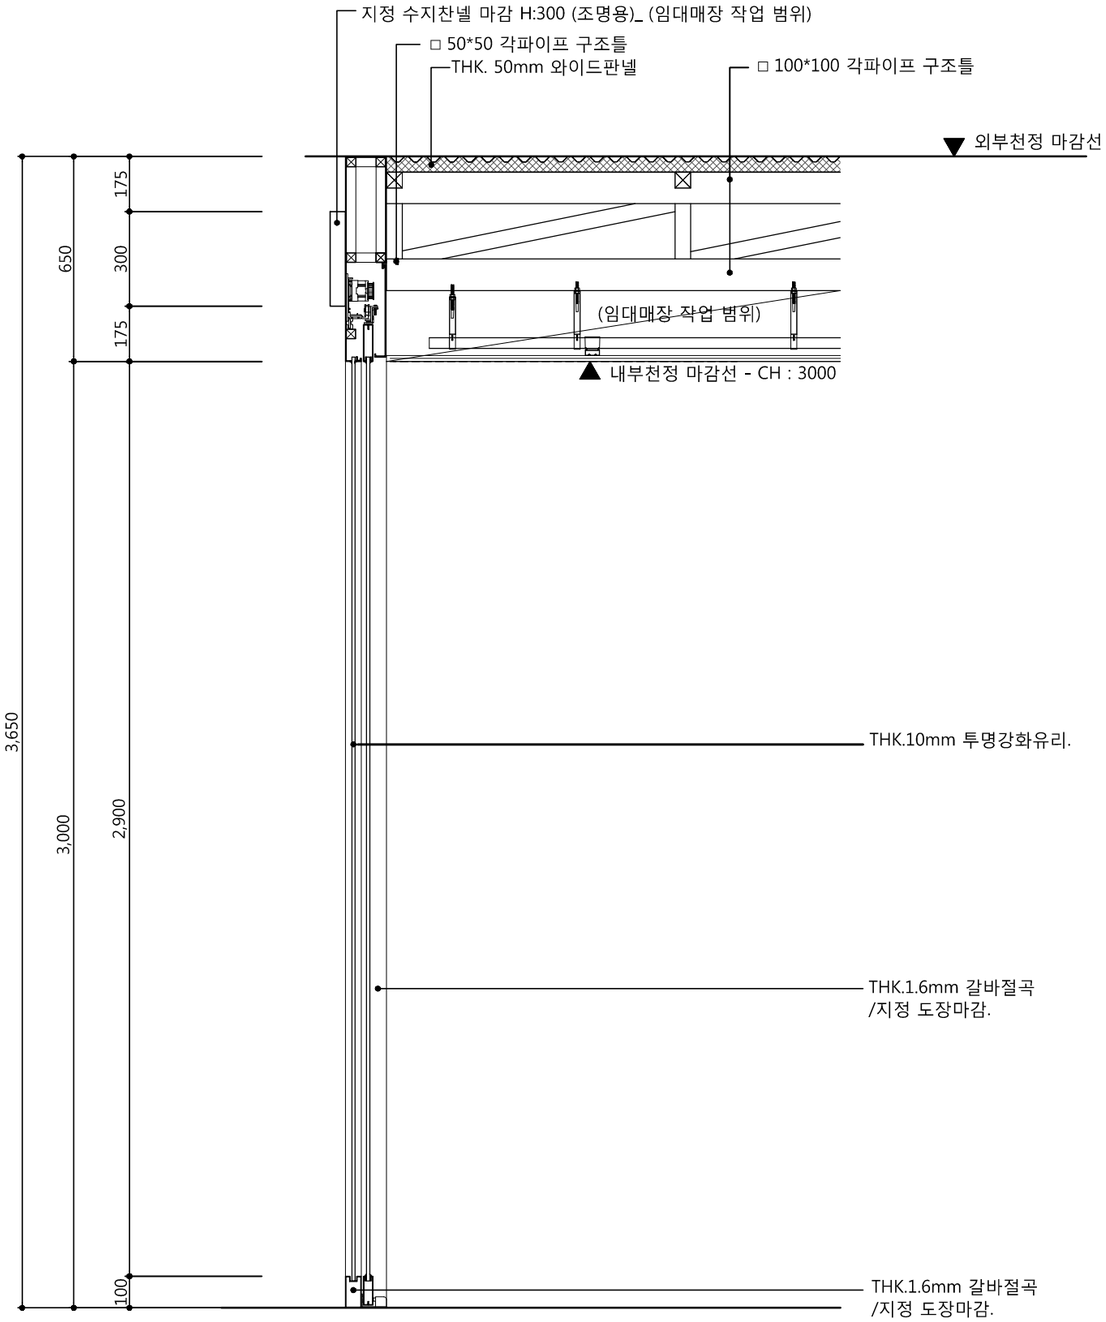

1 SCALE 1/20 **DETAIL1. 출입구 단면 상세도**

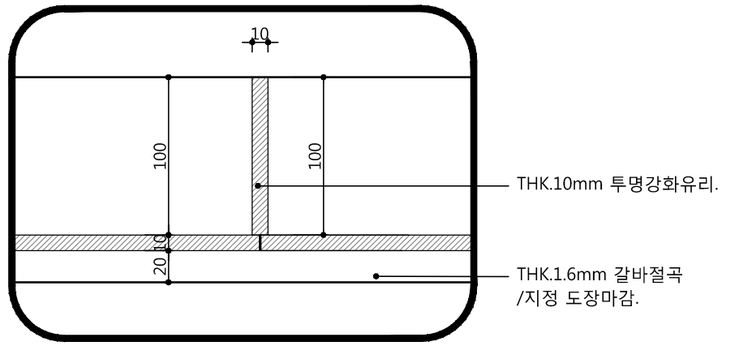

2 SCALE 1/20 **DETAIL 2. 유리 기둥 상세도**

KORAIL RETAIL
서울시 영등포구 당산3가 2-7
TEL / 02) 2630-8945
FAX / 02) 2630-8926

StoryWay

NOTE / REVISION

NAME OF PROJECT
부산역 3F 맞이방 전문점

ARCHITECTURE

STRUCTURE

MECHANIC

ELECTRIC

APPROVED BY

DESIGNED BY

DRAWING BY
Park, Hyeran

CHECKED BY
Choi, Jinha

DATE
2017. 01. 08


SCALE
1 / 20

DRAWING TITLE
DETAILS


PROJECT NO.

SHEET NO.	DRAWING NO.
012	D-001

Greco DESIGNGROUP
Sukjung Bldg. 2F
203-3 Donggyo-dong,
Mapo-gu, Seoul, Korea. 03992
www.grecodesign.co.kr
T.+82-2-336-2082 F.+82-2-336-2297

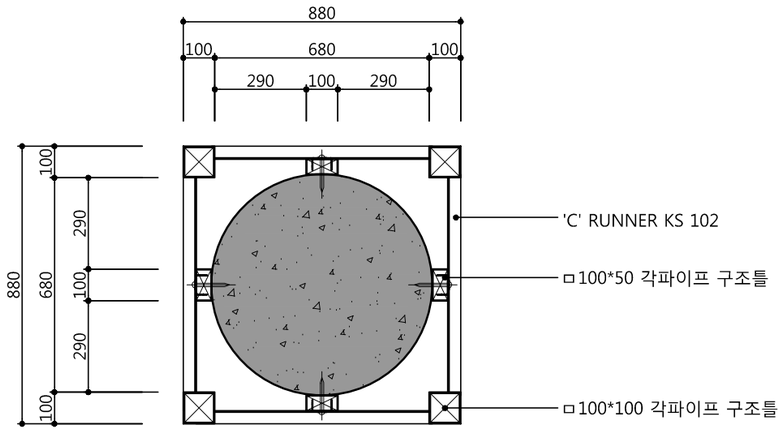

2 SCALE 1/20 **TOP VIEW**

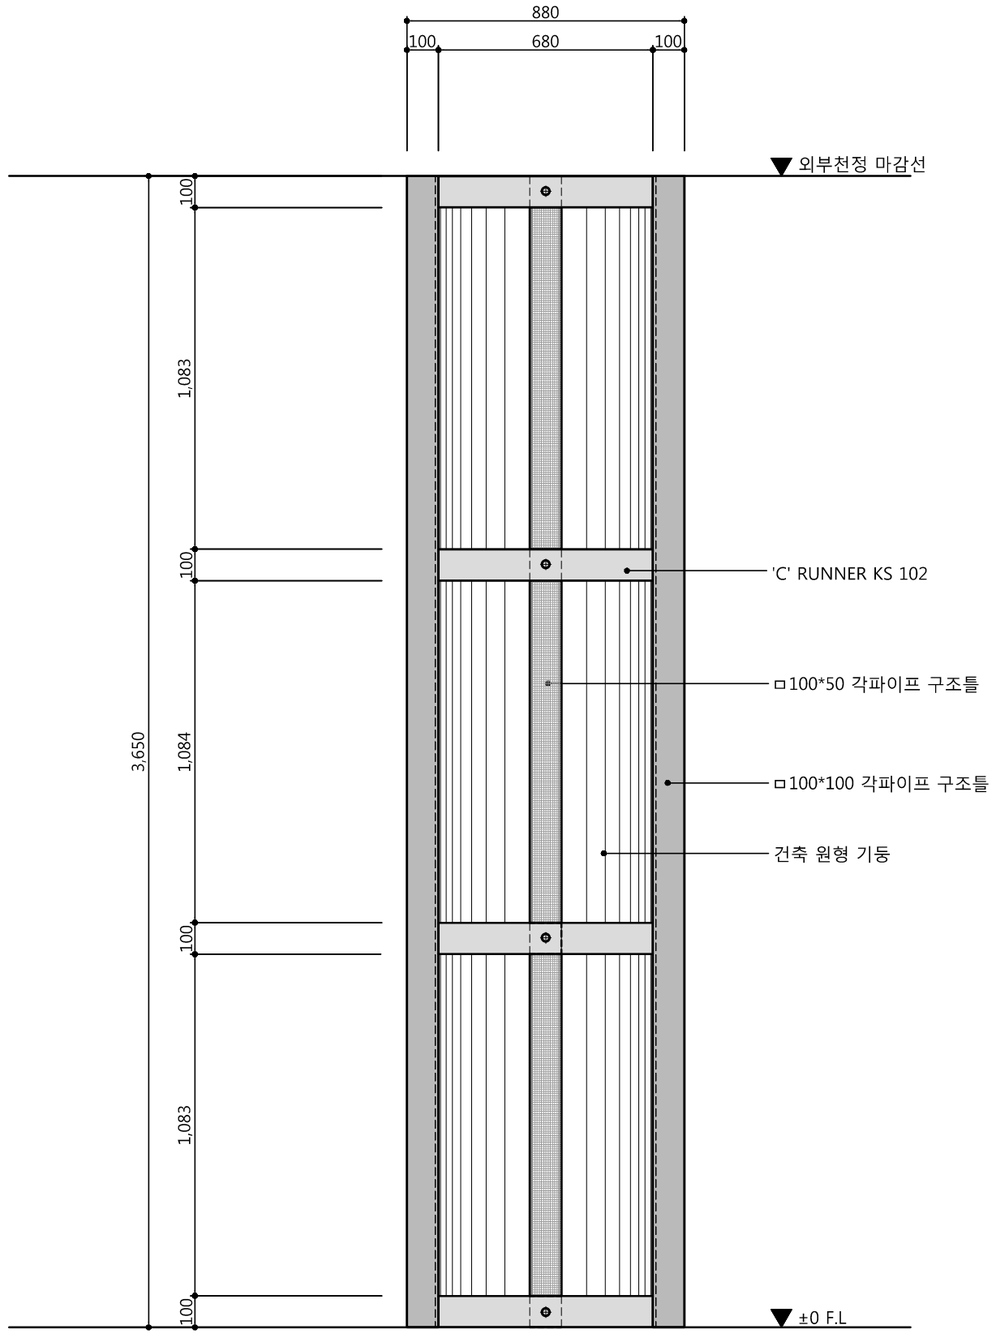

1 SCALE 1/20 **FRONT VIEW**

KORAIL RETAIL
서울시 영등포구 당산3가 2-7
TEL / 02) 2630-8945
FAX / 02) 2630-8926

StoryWay

NOTE / REVISION

NAME OF PROJECT
부산역 3F 맞이방 전문점

ARCHITECTURE

STRUCTURE

MECHANIC

ELECTRIC

APPROVED BY

DESIGNED BY

DRAWING BY
Park, Hyeran

CHECKED BY
Choi, Jinha

DATE
2017. 01. 08

SCALE
1 / 20

DRAWING TITLE
원형기둥 구조틀 상세도

PROJECT NO.

SHEET NO.	DRAWING NO.
012	D-001

Greco DESIGNGROUP
Sukjung Bldg. 2F
203-3 Donggyo-dong,
Mapo-gu, Seoul, Korea. 03992
www.grecodesign.co.kr
T.+82-2-336-2082 F.+82-2-336-2297