KORAIL RETAIL

부산역 3층맞이방 전문점(푸드코트) 소방설비공사

2018 . 12.

코레일유통(주)

DRAWING LIST

NO	DWG.NO	DRAWING NO
		COVER SHEE
1	EF – 00	소방 도면 목록표
2	EF – 01	소방범례
3	EF – 02	3층 소방간선 및 시각경보기 설비 평면도
4	EF – 03	3층 자동화재탐지 설비 평면도
5	EF – 04	3층 유도등 설비 평면도
6	EF – 05	3층 비상조명등 설비 평면도
7	EF – 06	3층 비상방송 설비 평면도
8	EF – 07	3층 다중이용업 소방 설비 평면도
9	EF – 08	소방 일반 상세도

PROJECT TITLE
공 사 명

부산역 3층 전문식당가
소방설비공사

설 계 DESIGNED BY	
심 사 CHECKED BY	
승 인 APPROVED BY	
화 일 명 NAME OF FILE	
일 자 DATE	2018. 12.
축 척 SCALE	A3: 1/NO
도 면 명 NAME OF DRAWING	소방도면 목록표
도 면 번 호 DRAWING NO.	EF -00
일 련 번 호 SHEET NO.	

(주) 장인기술단
JANG IN ENGINEERING GRUP
대표이사 김 인 수
부산광역시 동래구 온천천로 339번길 28
TEL.(051)644-1744
FAX.(051)818-2673

소방도면 목록표

SCAL(A3)
1/NO

기 호	내 용
	화 재 수 신 반 (다중이용업용)
	경 보 기 셋 (다중이용업용)
	소 화 반 경 보 기 셋 (기존)
	차 동 식 감 지 기 (2종)
	정 온 식 감 지 기 (1종)
	시 각 경 보 기
Ω	종 단 저 항
	피 난 구 유 도 등 (대형)
	거 실 통 로 유 도 등 (중형)
	벽 부 비 상 조 명 등 (밧데리)
	천 장 노 출 형 스 피 커 (3 W)
휴	휴 대 용 비 상 조 명 등
□	아 우 트 레 트 B O X
⊠	P U L L B O X (규격은도면참조)
———	벽 체 및 천 장 슬 라 브 매 입 (난연CD 전선관)
—— ——	바 닥 슬 라 브 매 입 (난연CD 전선관)
- - - - -	벽 체 및 천 장 노 출 (플렉시블전선관)

(감지기)

——— F ——— HFIX 1.5sq – 2 (16c)

—//— F ——— HFIX 1.5sq – 4 (16c)

(시각경보기)

——— B ——— HFIX 2.5sq – 2 (16c)

(유도등)

——— E ——— HFIX 2.5sq – 2 (16c)

(비상조명등)

——— E ——— HFIX 2.5sq – 3 (16c)

(스피커)

——— E ——— HFIX 1.5sq – 2 (16c)

<< 주기사항 >>

1. 도면에 별도 표기없는 기기의 설치 높이는 아래에 의함
   - –화재수신반 : 바닥에서 MH800MM이상 MH1500MM이하
   - –경보기셋 : 바닥에서 MH800MM이상 MH1500MM이하
   - –시각경보기 : 바닥에서 MH2000MM이상 MH2500MM이하
   - –휴대용 비상조명등 : 바닥에서 MH800MM이상 MH1500MM이하
   - –피난구 유도등 : 문틀상부
   - –거실 통로유도등 : 바닥에서 MH1500MM이상
   - –벽부비상조명등 : 바닥에서 MH2500MM이상
2. 모든 소방기구류는 공인시험기관의 인정받은 제품을 사용할것.
3. 기존 R형 화재수신반 프로그램 및 CRT 변경할것.

PROJECT TITLE
공 사 명

부산역 3층 전문식당가
소방설비공사


설 계 DESIGNED BY	
심 사 CHECKED BY	
승 인 APPROVED BY	
화 일 명 NAME OF FILE	
일 자 DATE	2018. 12.
축 척 SCALE	A3:1/NO
도 면 명 NAME OF DRAWING	소방 범례
도 면 번 호 DRAWING NO.	EF -01
일 련 번 호 SHEET NO.	

(주) 장인기술단
JANG IN ENGINEERING GRUP
대표이사 감 인 수
부산광역시 동래구 온천천로 339번길 28
TEL.(051)644-1744
FAX.(051)818-2673

소방시설계획서	
시각경보기	
◘	9EA

PROJECT TITLE
공 사 명

부산역 3층 전문식당가 소방설비공사

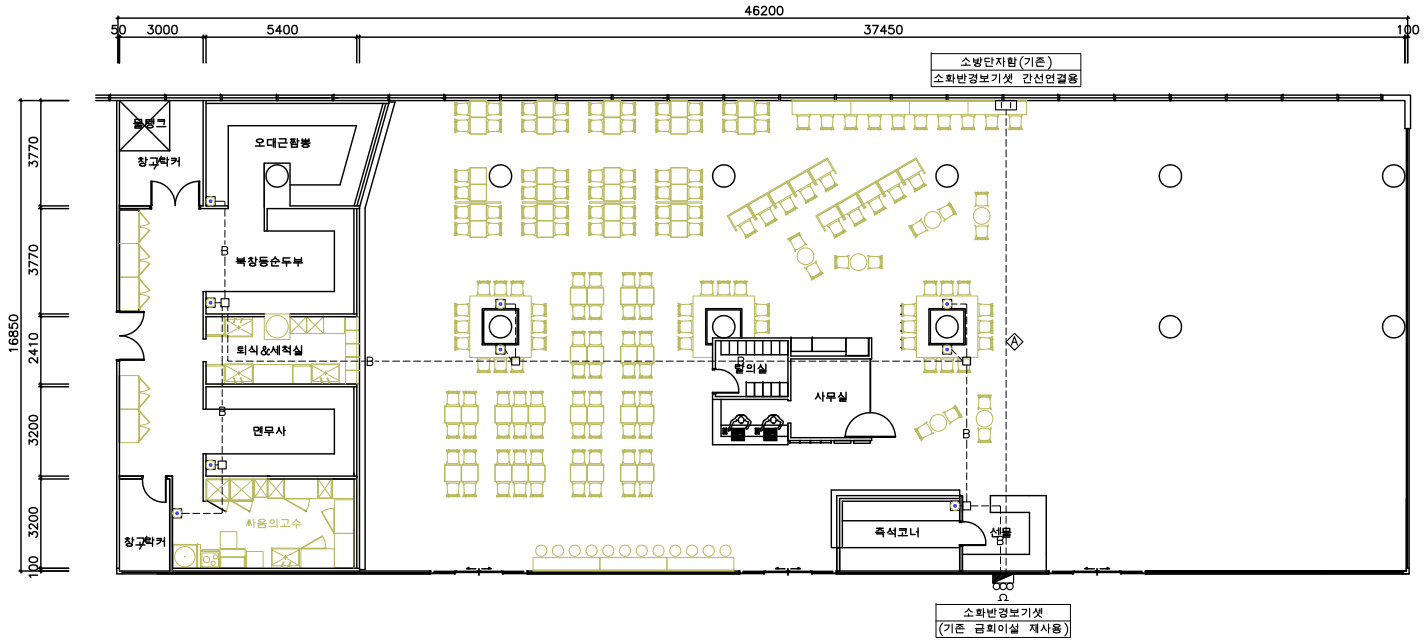

주기사항

1. 도면에 별도 표기없는 시각경보기 배관배선은 아래에 의함.
   ---B--- HFIX 2.5sq - 2 (16c)

Ⓐ	HCW-SB 2.5sq/2c-1 (22c)	신호전송선2
	HFIX 2.5sq - 10 (36c)	중계기 및 부하전원2,시각경보기2, 소화전기동확인2,전화,응답,표시등,공통

설 계 DESIGNED BY	
심 사 CHECKED BY	
승 인 APPROVED BY	
화 일 명 NAME OF FILE	
일 자 DATE	2018. 12.
축 척 SCALE	A3:1/200
도 면 명 NAME OF DRAWING	3층 소방간선 및 시각경보기 설비 평면도
도 면 번 호 DRAWING NO.	EF 02
일 련 번 호 SHEET NO.	

(주) 장인기술단
JANG IN ENGINEERING GRUP
대표이사 김 인 수
부산광역시 동래구 온천천로 339번길 28
TEL.(051)644-1744
FAX.(051)818-2673


3층 소방간선 및 시각경보기 설비 평면도

SCALE(A3) 1/200

소방시설계획서		
감지기		
ㅁ	차동식	24EA
ㅁ	정온식	7EA

PROJECT TITLE
공 사 명

부산역 3층 전문식당가 소방설비공사

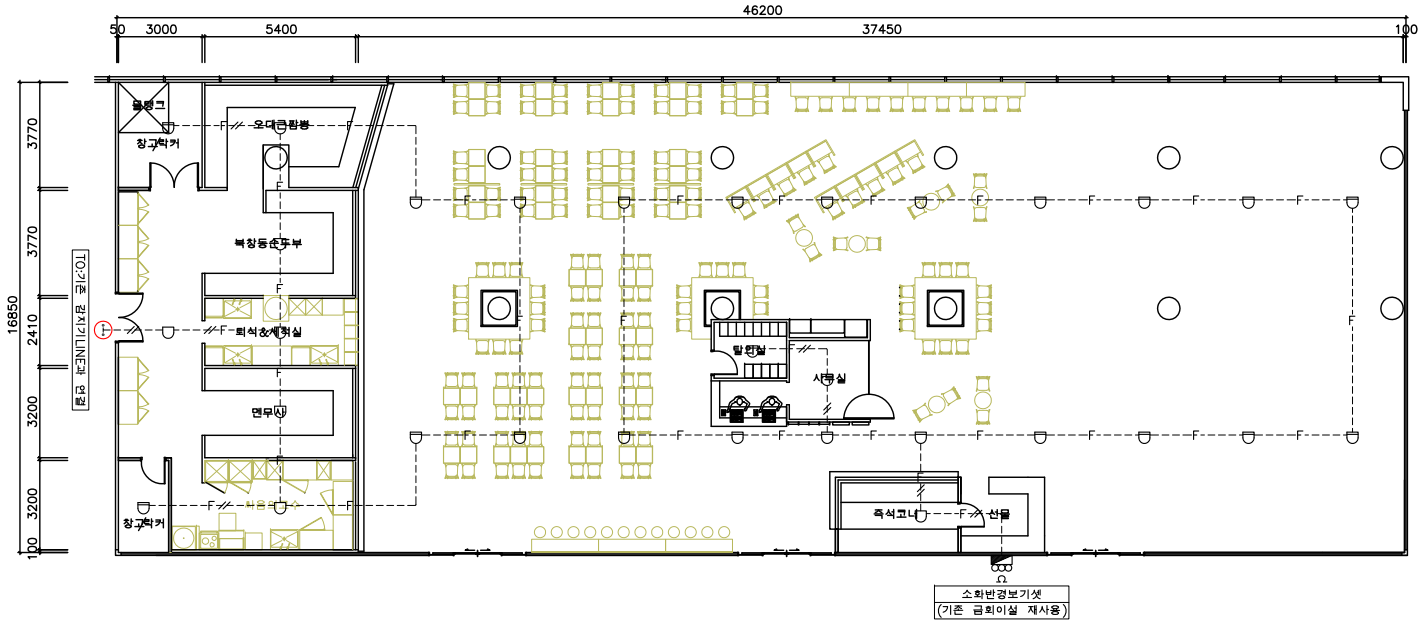

주기사항

1. 도면에 별도 표기없는 감지기 배관배선은 아래에 의함.
   ---F--- HFIX 1.5sq – 2 (16c)
   ---F-//- HFIX 1.5sq – 4 (16c)

설 계 DESIGNED BY	
심 사 CHECKED BY	
승 인 APPROVED BY	
화 일 명 NAME OF FILE	
일 자 DATE	2018. 12.
축 척 SCALE	A3:1/200
도 면 명 NAME OF DRAWING	3층 자동화재탐지 설비 평면도
도 면 번 호 DRAWING NO.	EF 03
일 련 번 호 SHEET NO.	

(주) 장인기술단
JANG IN ENGINEERING GRUP
대표이사 김 인 수
부산광역시 동래구 온천천로 339번길 28
TEL.(051)644-1744
FAX.(051)818-2673


3층 자동화재탐지 설비 평면도

SCALE(A3) 1/200

소방시설계획서		
유도등		
	피난구유도등(대형)	4EA
	거실통로유도등(중형)	2EA

PROJECT TITLE
공 사 명

부산역 3층 전문식당가 소방설비공사

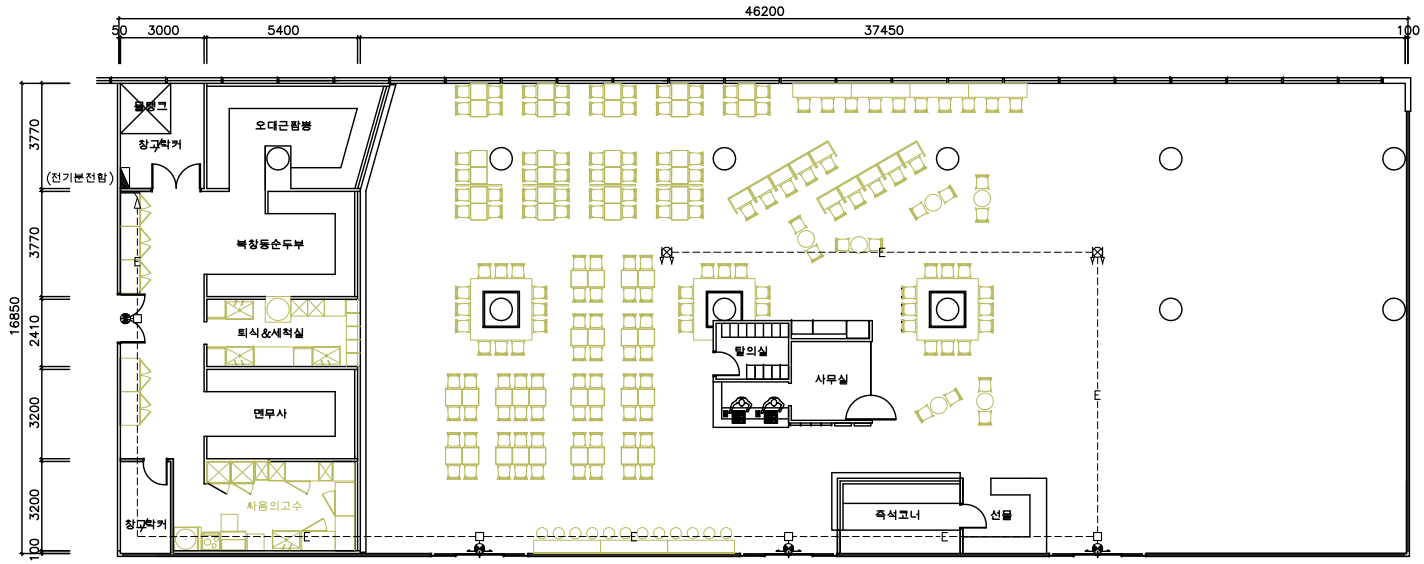

주기사항

1. 도면에 별도 표기없는 유도등설비 배관배선은 아래에 의함.
---E--- HFIX 2.5sq – 2 (16c)

설 계 DESIGNED BY	
심 사 CHECKED BY	
승 인 APPROVED BY	
화 일 명 NAME OF FILE	
일 자 DATE	2018. 12.
축 척 SCALE	A3:1/200
도 면 명 NAME OF DRAWING	3층 유도등 설비 평면도
도 면 번 호 DRAWING NO.	EF 04
일 련 번 호 SHEET NO.	

(주) 장인기술단
JANG IN ENGINEERING GRUP
대표이사 김 인 수
부산광역시 동래구 온천천로 339번길 28
TEL.(051)644-1744
FAX.(051)818-2673


3층 유도등 설비 평면도

SCAL(EA3) 1/200

소방시설계획서		
비상조명등		
	벽부비상조명등	6EA

PROJECT TITLE
공 사 명

부산역 3층 전문식당가 소방설비공사

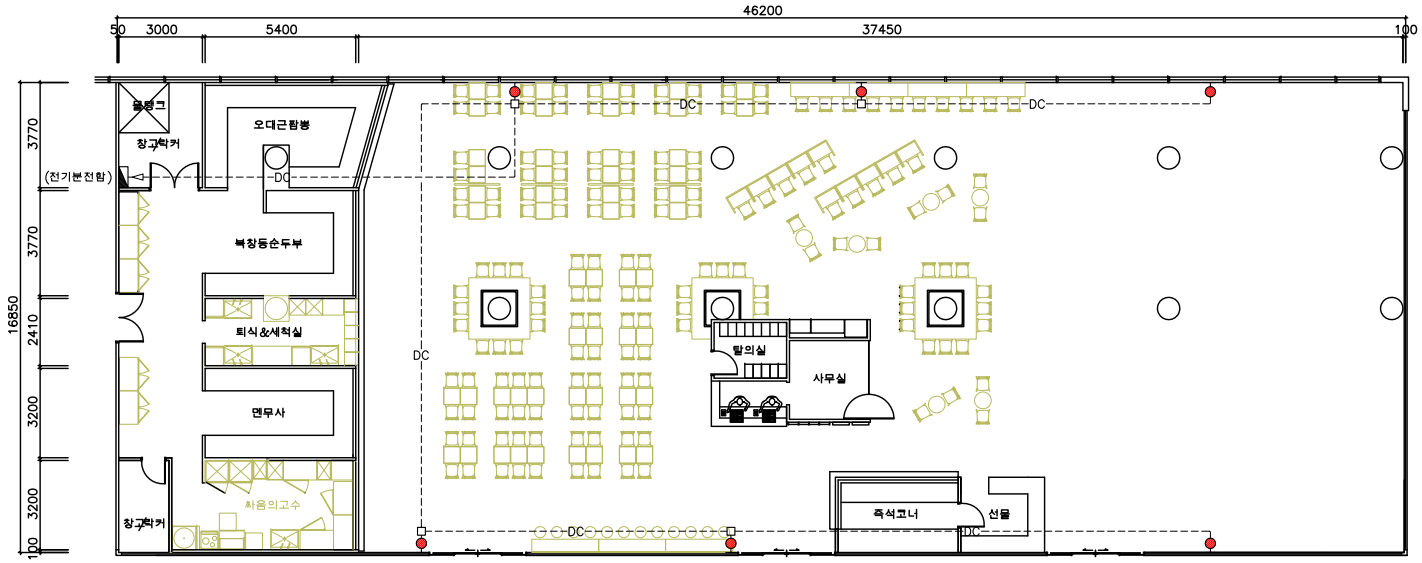

주기사항

1. 도면에 별도 표기없는 비상조명설비 배관배선은 아래에 의함.
   ---DC--- HFIX 2.5sq – 3 (16c)

설 계 DESIGNED BY	
심 사 CHECKED BY	
승 인 APPROVED BY	
와 일 명 NAME OF FILE	
일 자 DATE	2018. 12.
축 척 SCALE	A3:1/200
도 면 명 NAME OF DRAWING	3층 비상조명등 설비 평면도
도 면 번 호 DRAWING NO.	EF 05
일 련 번 호 SHEET NO.	

(주) 장인기술단
JANG IN ENGINEERING GRUP
대표이사 김 인 수
부산광역시 동래구 온천천로 339번길 28
TEL.(051)644-1744
FAX.(051)818-2673


3층 비상조명등 설비 평면도

SCALE(A3) 1/200

소방시설계획서	
천장노출형 스피커(3W)	
▲	6EA

PROJECT TITLE
공 사 명

부산역 3층 전문식당가 소방설비공사

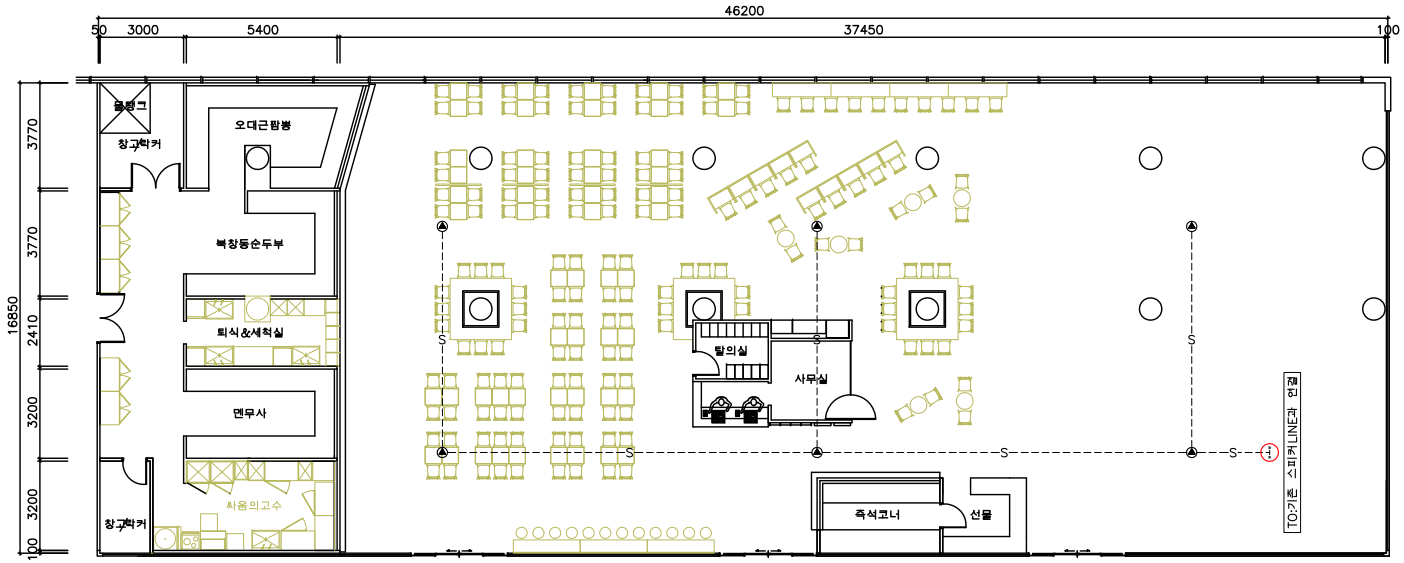

주기사항

1. 도면에 별도 표기없는 비상방송설비 배관배선은 아래에 의함.
   ---S--- HFIX 1.5sq – 2 (16c)

설 계 DESIGNED BY	
심 사 CHECKED BY	
승 인 APPROVED BY	
화 일 명 NAME OF FILE	
일 자 DATE	2018. 12.
축 척 SCALE	A3:1/200
도 면 명 NAME OF DRAWING	3층 비상방송 설비 평면도
도 면 번 호 DRAWING NO.	EF 06
일 련 번 호 SHEET NO.	

(주) 장인기술단
JANG IN ENGINEERING GRUP
대표이사 김 인 수
부산광역시 동래구 온천천로 339번길 28
TEL.(051)644-1744
FAX.(051)818-2673


3층 비상방송 설비 평면도

SCALE(A3) 1/200

소방시설계획서		
㉮	휴대용 비상조명등	10EA
BOPs	경보기셋	9EA

PROJECT TITLE
공 사 명

부산역 3층 전문식당가 소방설비공사

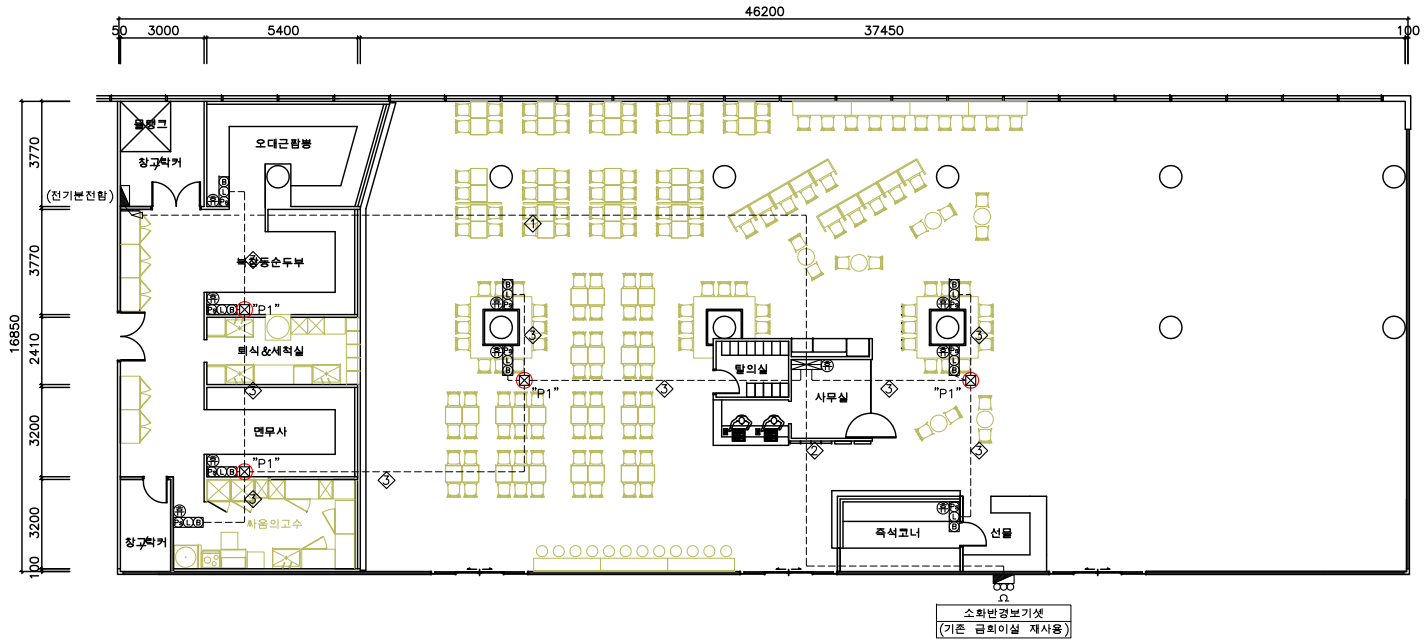

주기사항

번호	배관&배선	비고
①	HFIX 2.5sq – 3 (16c)	
②	HFIX 2.5sq – 4 (16c)	
③	HFIX 2.5sq – 5 (22c)	

화재수신반(다중이용업용)
–P형1급 5회로
–NI–CD 축전지내장
–오동작방지 기능 내장

"P1" PULL BOX (SIZE: 200x200x200)

설 계 DESIGNED BY	
심 사 CHECKED BY	
승 인 APPROVED BY	
화 일 명 NAME OF FILE	
일 자 DATE	2018. 12.
축 척 SCALE	A3: 1/200
도 면 명 NAME OF DRAWING	3층 다중이용업 소방 설비 평면도
도 면 번 호 DRAWING NO.	EF 07
일 련 번 호 SHEET NO.	


(주) 장인기술단
JANG IN ENGINEERING GRUP
대표이사 김 인 수
부산광역시 동래구 온천천로 339번길 28
TEL.(051)644–1744
FAX.(051)818–2673

3층 다중이용업 소방 설비 평면도

SCAL(EA3) 1/200

PROJECT TITLE
공 사 명


부산역 3층 전문식당가 소방설비공사

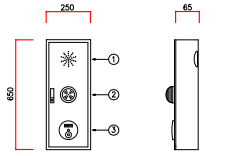

① 음향장(158mm BELL 내장) ③ P형 1급 수동발신기
② 위치 표시등


* 외함 : STEEL 1.2mmT이상, 카바 : SUS 1.6mmT이상

02 경보기셋

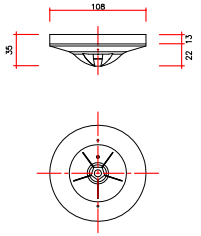


(반도체식)

04 정온식 스포트형 감지기

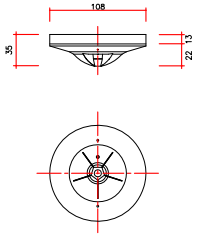


(반도체식)

05 차동식 스포트형 감지기

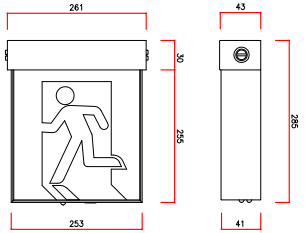


종별 구분	피난구유도등 대형
설치방구분	벽직부형-단면형
소비전력	상용 6.7~6.8[W] 비상 0.6[W]
광 원	LED(고효율에너지기자재 인증제품)
유효점등시간	60 [분] 용
예비전원	Ni-cd, DC3.6[V] 600[mAh]

07 피난구 유도등 (대형)

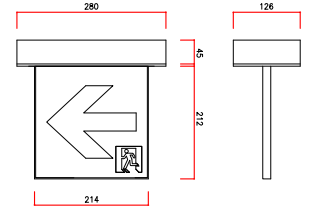


종별 구분	거실통로유도등 중형
설치방구분	천장노출형-단,양면형
소비전력	상용 3.5[W] 비상 0.5[W]
광 원	LED (고효율에너지기자재 인증제품)
유효점등시간	60 [분] 용
예비전원	Ni-cd, DC3.6[V] 600[mAh]

08 거실통로 유도등 (중형)

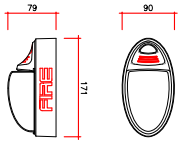


정격전압	D.C 24V
광 도	15 Cd
소비전류	80mA
렌즈색상	투명,크세논
몸체색상	백 색

12형각장애인용 시각경보장치

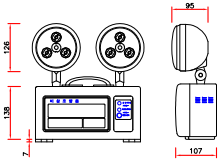

정격전압	AC 220V 60HZ
예비전원	니켈카드뮴 12V/1,300mA
램 프	백색 LED-1Wx8
유효점등시간	60분

13 벽부 비상조명 (LED 1Wx8)

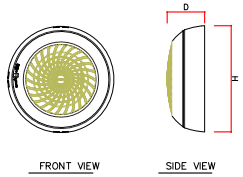

주파수특성	250Hz ~ 10KHz
정격입력	3W
음 압	88dB
규 격	212(H) x 75(D)

10 천장노출형 스피커(3W)

설 계 DESIGNED BY	
심 사 CHECKED BY	
승 인 APPROVED BY	
와 일 명 NAME OF FILE	
일 자 DATE	2018. 12.
축 척 SCALE	A3:1/NO
도 면 명 NAME OF DRAWING	소방 일반 상세도
도 면 번 호 DRAWING NO.	EF 08
일 련 번 호 SHEET NO.	


(주) 장인기술단
JANG IN ENGINEERING GRUP
대표이사 김 인 수
부산광역시 동래구 온천천로 339번길 28
TEL.(051)644-1744
FAX.(051)818-2673

소방 일반 상세도


SCAL(EA3)
1/NO

소 화 범 례

도 시 기 호	명 칭	비 고
SP	스프링클라 배관	1.2Mpa 이하 일반배관용 탄소강관 1.2Mpa 이상 압력배관용 탄소강관
X	연결 송수구 배관	1.2Mpa 이하 일반배관용 탄소강관 1.2Mpa 이상 압력배관용 탄소강관
H	옥내소화전 배관	1.2Mpa 이하 일반배관용 탄소강관 1.2Mpa 이상 압력배관용 탄소강관
D	스프링클라 배수관	1.2Mpa 이하 일반배관용 탄소강관 1.2Mpa 이상 압력배관용 탄소강관
	옥 내 소 화 전 함	전면SUS1.5T, 후면STEEL1.6T
	스프링클러 헤드	상향식
	스프링클러 헤드	하향식
	티 엘 보	
	엘 보 , 티 이	
소	A.B.C.분말소화기	ABC 3.3KG
K	K급 분말소화기	3.0 LIT

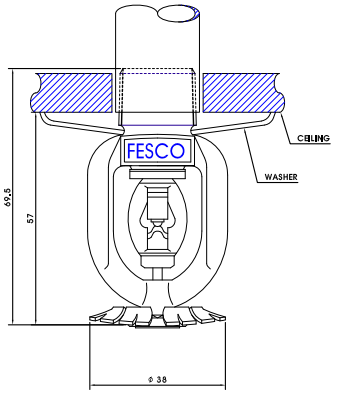

스프링클러헤드(하향식)

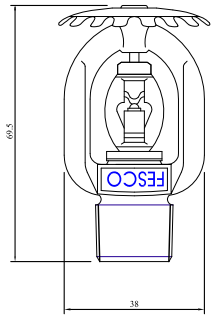

스프링클러헤드(상향식)

NOTE / REVISION

NAME OF PROJECT

부산역 3층 맞이방
전문점2 소방설비공사

ARCHITECTURE

STRUCTURE

MECHANIC

ELECTRIC

APPROVED BY

DESIGNED BY

DRAWING BY

CHECKED BY

DATE
2018. 10

SCALE
A3 – 1 / NO

DRAWING TITLE

소화 범례 및
헤드 상세도

PROJECT NO.


SHEET NO.	SHEET NO.
000	MF-01

KORAIL RETAIL

서울시 영등포구 당산3가 2–
TEL / 02) 2630–8945
FAX / 02) 2630–8926

1 기계소방 평면도


SCALE
1 / 200

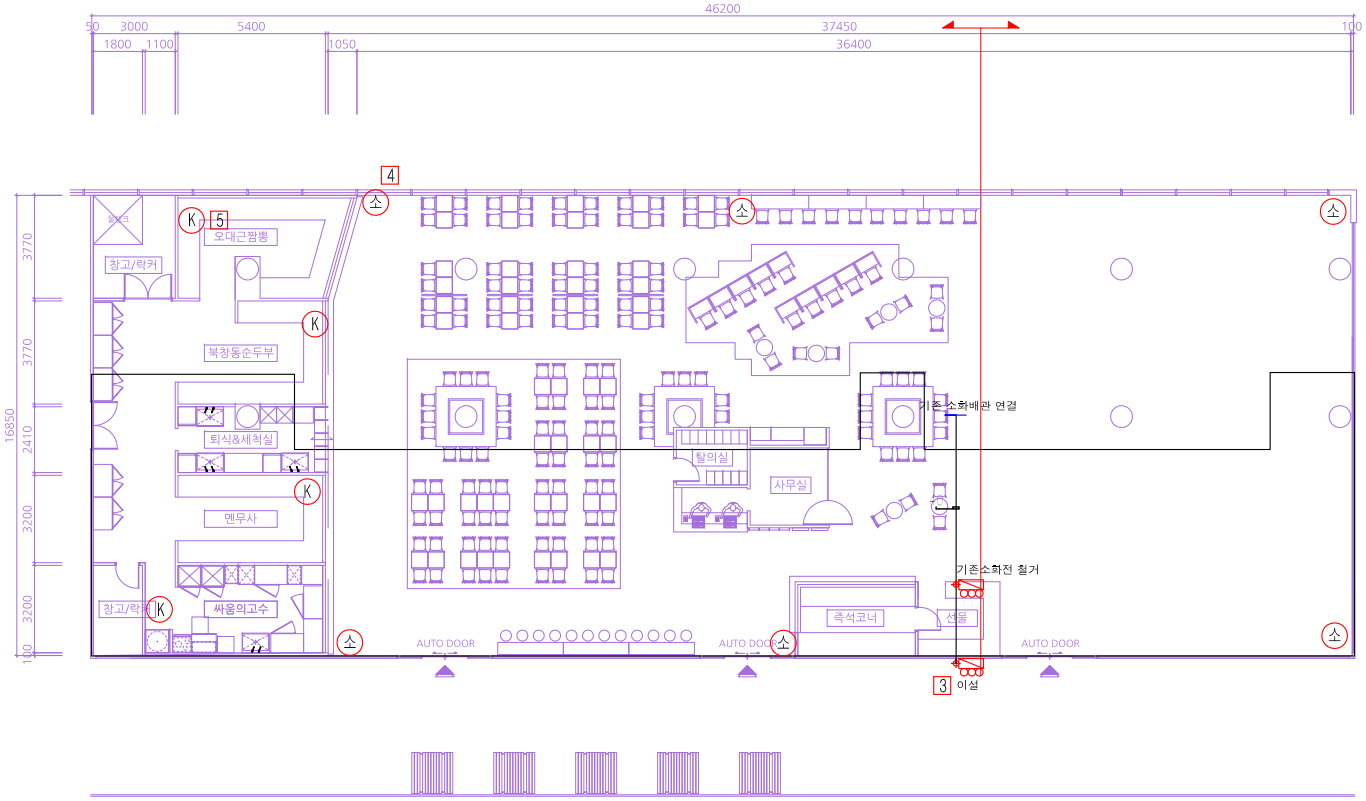


NOTES

심벌번호	심벌	명 칭 (내용)	개수
3		옥내소화전 노출 스텐	1EA
		앵글밸브 40mm	1EA
		노즐 40mm	1EA
		소방호스(단일피) 40mm	2EA
4	소	분말소화기(A.B.C.급) 3.3KG/3단위 A급기준	6 EA
5	K	분말소화기(K급) 3.0L	4 EA

** 철거부분

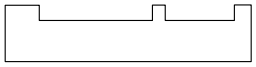

- 상기표시부분 철거 후 신설배관
- 나머지부분 주름관 철거 및 헤드부분 신설 하향배관

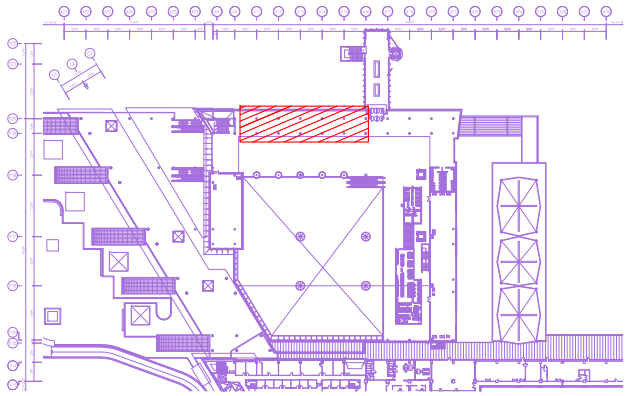

KEY PLAN

2
MF

지상3층 전문식당가 기계소방 평면도 - 1

SCALE : 1 / 200

1 기계소방 평면도

SCALE 1 / 200

NOTE / REVISION

NAME OF PROJECT
부산역 3층
전문식당가 소방설비공사

ARCHITECTURE

STRUCTURE

MECHANIC

ELECTRIC

APPROVED BY

DESIGNED BY

DRAWING BY

CHECKED BY

DATE
2018. 10

SCALE
A3 – 1 / 200


DRAWING TITLE
지상3층 전문식당가
기계소방 평면도 - 1

PROJECT NO.

SHEET NO.
000

SHEET NO.
MF-02


KORAIL RETAIL
서울시 영등포구 당산3가 2–
TEL / 02) 2630–8945
FAX / 02) 2630–8926

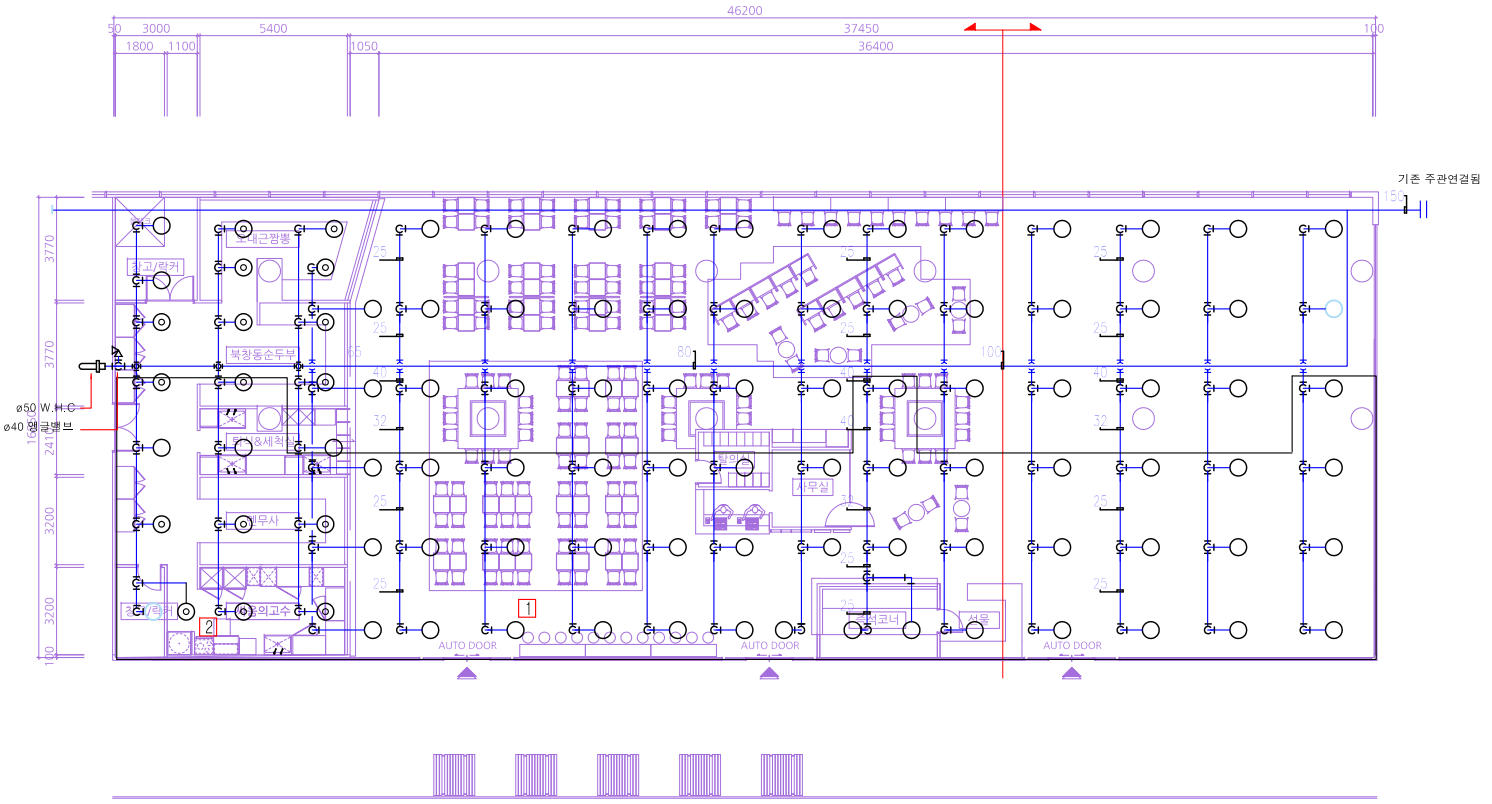


NOTES

심벌번호	심벌	명 칭 (내용)	개수
1		스프링클러 헤드(폐쇄형) 하향식 103° C 15A	16EA
2		스프링클러 헤드(폐쇄형) 하향식 72° C 15A	84EA

** 철거부분

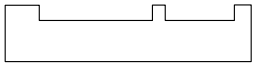

- 상기표시부분 철거 후 신설배관
- 나머지부분 주름관 철거 및 헤드부분 신설 하향배관

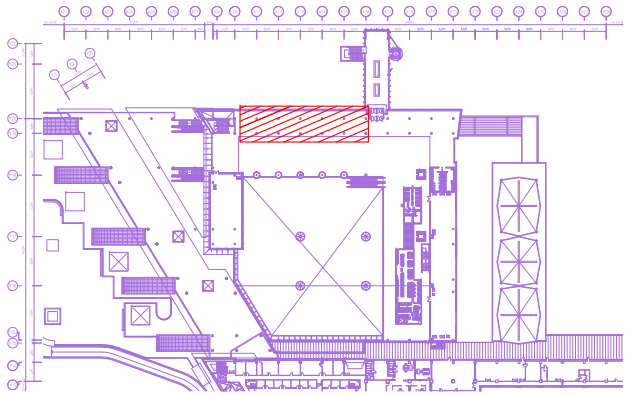

KEY PLAN

2
MF

지상3층 전문식당가 기계소방 평면도 - 2

SCALE : 1 / 200

1 기계소방 평면도

SCALE
1 / 200

NOTE / REVISION

NAME OF PROJECT
부산역 3층
전문식당가 소방설비공사

ARCHITECTURE

STRUCTURE

MECHANIC

ELECTRIC

APPROVED BY

DESIGNED BY

DRAWING BY

CHECKED BY

DATE
2018. 12

SCALE
A3 – 1 / 200


DRAWING TITLE
지상3층 전문식당가
기계소방 평면도 - 2

PROJECT NO.

SHEET NO.
000

SHEET NO.
MF-03


KORAIL RETAIL
서울시 영등포구 당산3가 2–
TEL / 02) 2630–8945
FAX / 02) 2630–8926

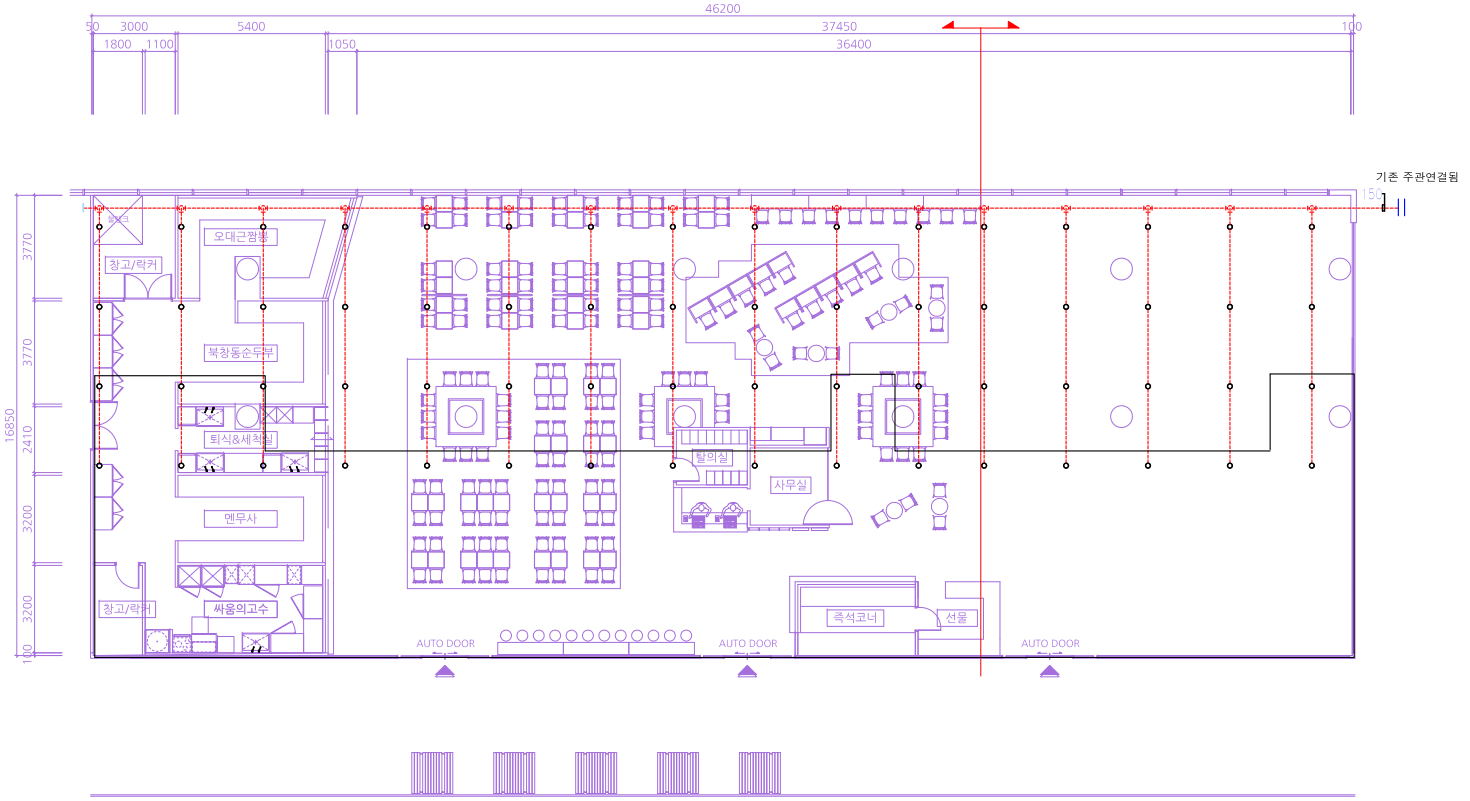

NOTES

심벌번호	심벌	명 칭 (내용)	개수
1	—○—	스프링클러 헤드(폐쇄형) 상향식 72° C 15A	64 EA

- 주름관 철거 및 하향식 헤드철거후 신설 상향식 헤드

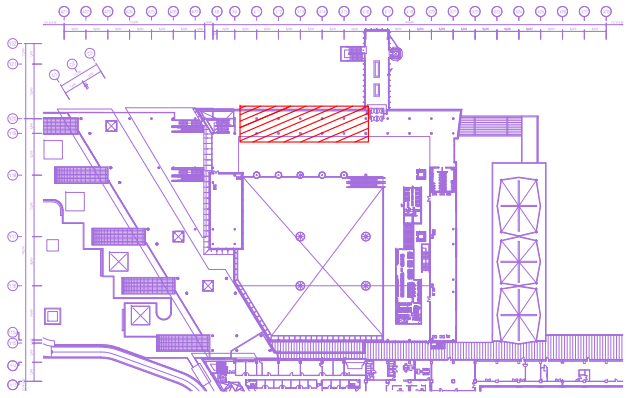

KEY PLAN

2
MF

지상3층 전문식당가 기계소방 평면도 - 3

SCALE : 1 / 200

1 기계소방 평면도

SCALE
1 / 200

NOTE / REVISION

NAME OF PROJECT
부산역 3층
전문식당가 소방설비공사

ARCHITECTURE

STRUCTURE

MECHANIC

ELECTRIC

APPROVED BY

DESIGNED BY

DRAWING BY

CHECKED BY

DATE
2018. 10

SCALE
A3 – 1 /200

DRAWING TITLE
지상3층 전문식당가
기계소방 평면도 - 3

PROJECT NO.

SHEET NO.	SHEET NO.
000	MF-04

KORAIL RETAIL

서울시 영등포구 당산3가 2–
TEL / 02) 2630–8945
FAX / 02) 2630–8926